


功能区布局

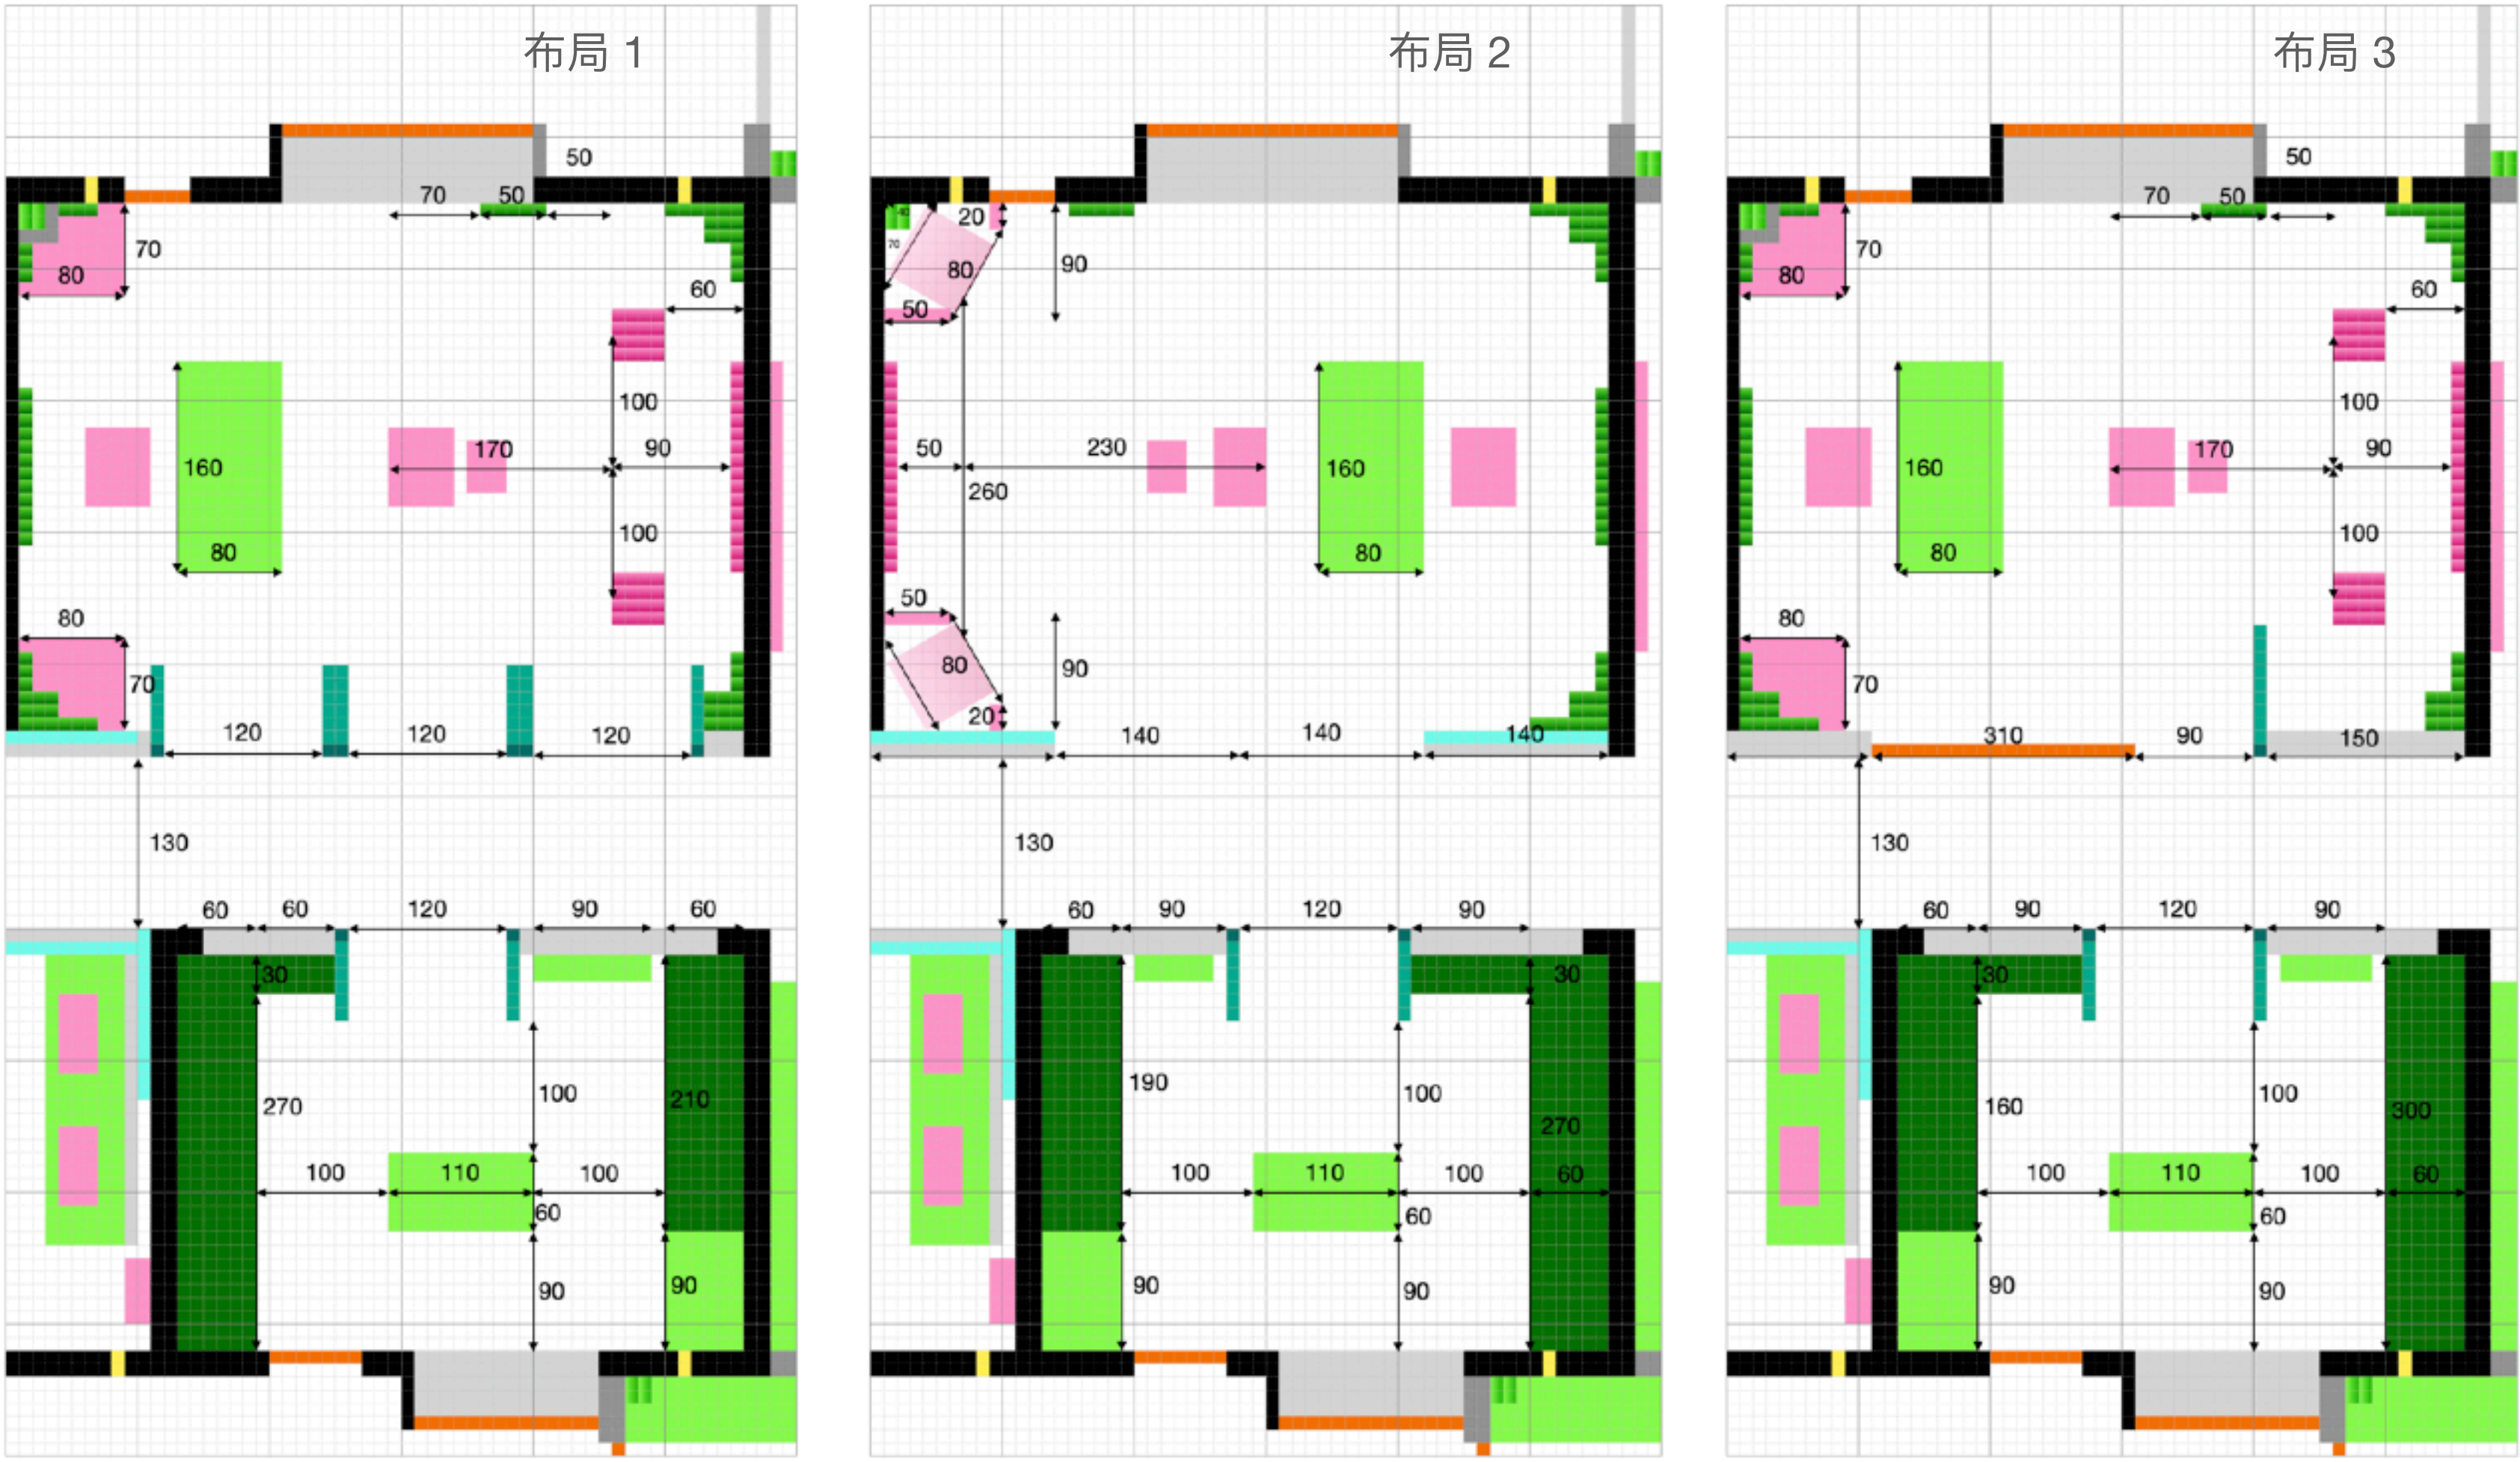

书房:

方案一：偏轴门，中式气韵

- 亮点：单扇 120 cm，三扇叠合可形成 360 cm 的“全景开口”，书房与更衣室门洞可精准对位，仪式感拉满。
- 隐忧：门扇间留缝，隔音是软肋。

方案二：双拉门，稳妥之选

- 亮点：两扇 140 cm 拉门，总开口 280 cm，施工简单、造价友好。
- 隐忧：轨道间缝隙仍在，隔音依旧打折。

方案三：玻璃实墙，别墅“轻中式”

- 亮点：整面落地玻璃替代实墙，保留中式格栅或夹绢纹样，空间通透却仍有东方意韵；中空玻璃一关，隔音不再是痛点。
- 隐忧：玻璃需勤擦拭才能常保清透；格栅比例、色温、金属收边需与全屋木作、硬装细节反复校色，否则易显突兀。

更衣室

梳妆台与全身镜的位置, 可以放在同一边, 或是相反方向. 另外根据书房门的选择, 更衣室的门可能需要偏一边, 或是居中. 全身镜的大小与相对短进深的饰品装饰柜(如包包) 可以放在长边或是短边. 另外衣柜可以选择壁挂系统, 或是立柱系统. 衣柜的照明也可以是由上往下, 或是直接用背光系统. (如衣柜背板使用宣纸灯箱)

音箱可以用音响架放在客厅方向, 或是利用柜子然后放在柜子上(优先考虑)




布局 1

布局 2
(纯示意)

布局 3
(纯示意)



特殊区域布局 (目前选择)

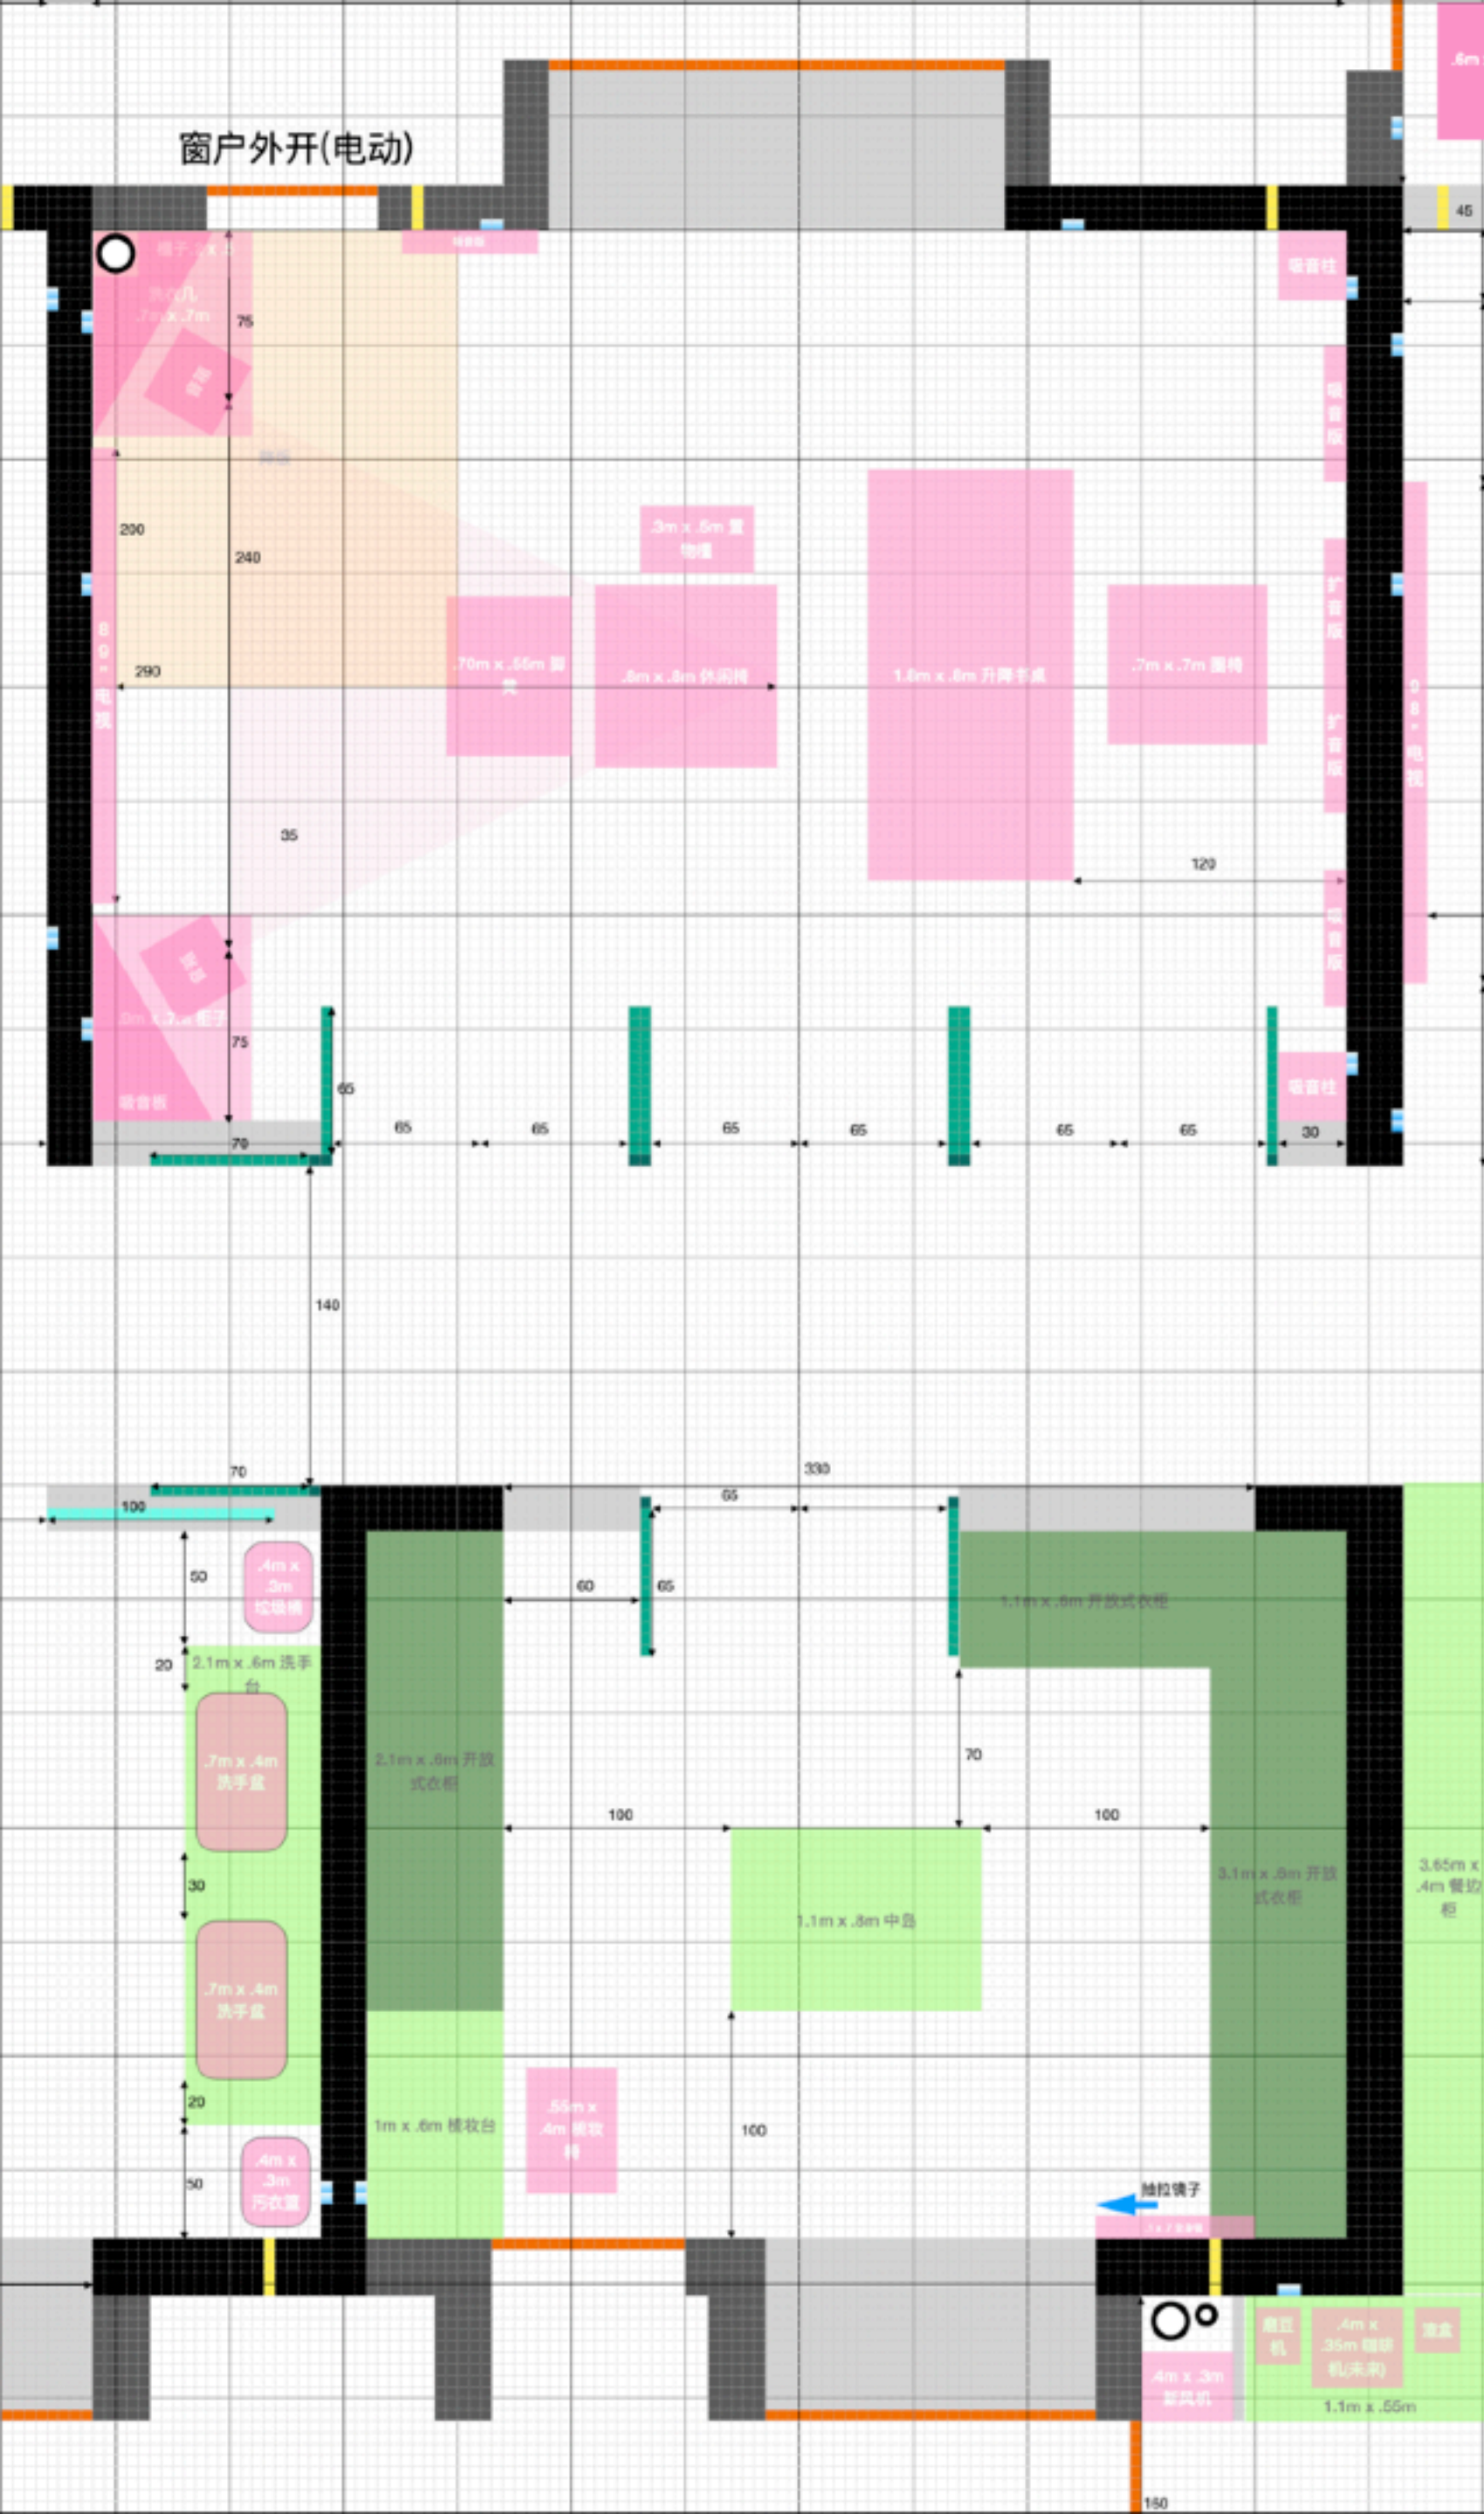

- 重点:
- 书房主要为单人使用
- 需要舒适的休闲椅
- 需要升降书桌(不需要对应的人体工学椅, 只要漂亮就行)
- 洗烘一体机放在柜子里, 另外一边的柜子内可以是空的, 事后再找置物架. 另外柜子需要门. (封闭或开放都可以)
- 使用洗烘一体的原因是烘的功能主要服务于梅雨季, 其他时间以晾晒为主.
- 注意柜子上还会在角落安装三角形吸音柱来盖住下水管

- 更衣室
- 需要中岛, 走道应该尽可能宽敞
- 需要梳妆台, 注意尽可能不要台面下的抽屉, 腿会比较好放, 且扶手不会与抽屉发生冲突. 梳妆台收纳可以坐在旁边的抽屉
- 中岛两侧应该做成开放格, 抽屉做在飘窗方向, 朝走道应该以美观为主
- 大型物件, 如冬季棉被, 优先考虑放在中岛. 四周全部都是开放式衣柜. 吊衣服为主, 可以有少量抽屉. 注意下面最好为开放式, 允许扫地机进入