

次卧佈局

次卧:

方案一：酒店配置

- 亮点：淋浴房与厕所在次卫的两侧, 理论上互不影响
- 隐忧：次卫镜子对房间

方案二：原始配置





- 亮点：床不会对着镜子, 次卫可以有多个独立分区
- 隐忧：次卫空间一部分用做柜子. (净衣或储藏室) 整体次卫可用空间较小. 另外洗脸盆太小了. 整体尺寸需要调整

方案三：

- 亮点：次卫入口与次卧入口不互相遮挡
- 隐忧：整体动线是最长的, 排水有疑问

方案四:

- 亮点: 套房最开放布置
- 隐忧: 次卧与次卫没有分隔, 床头直视镜子

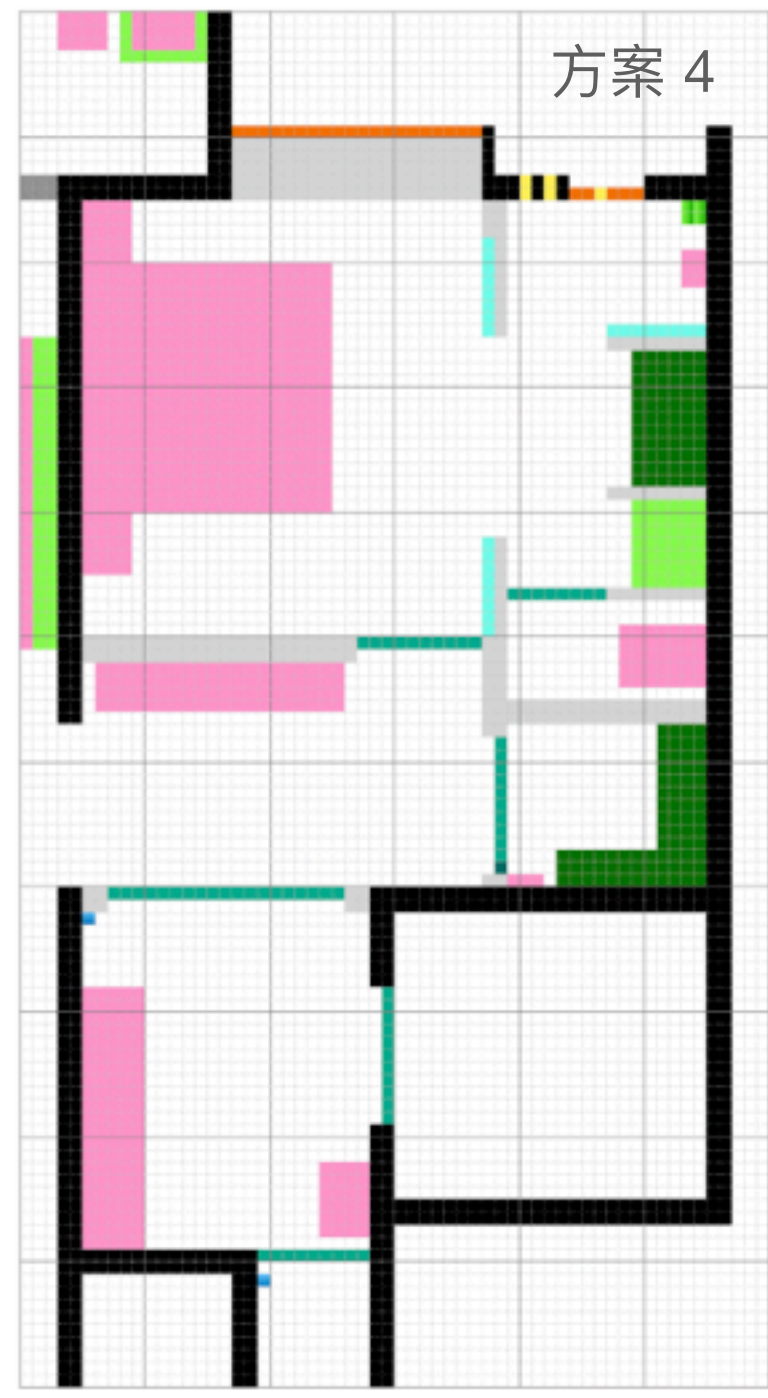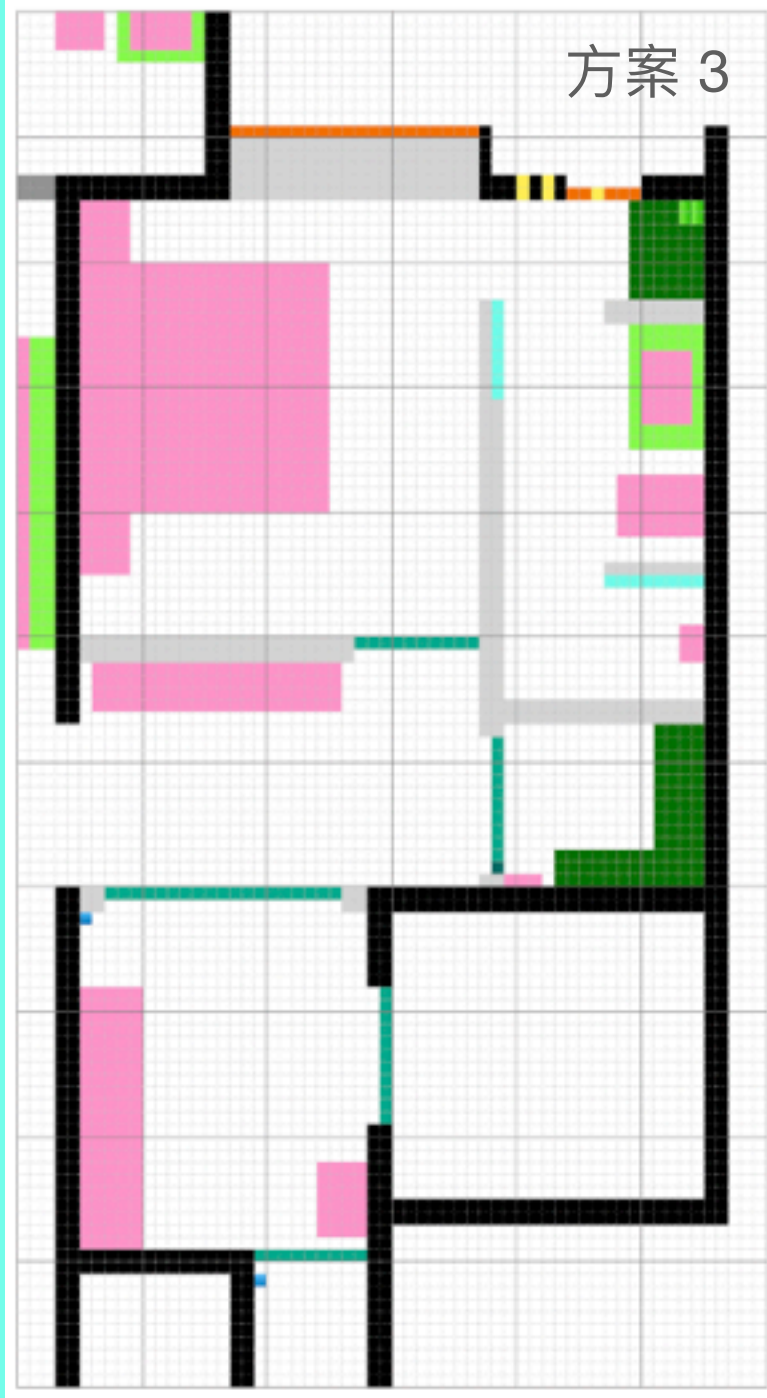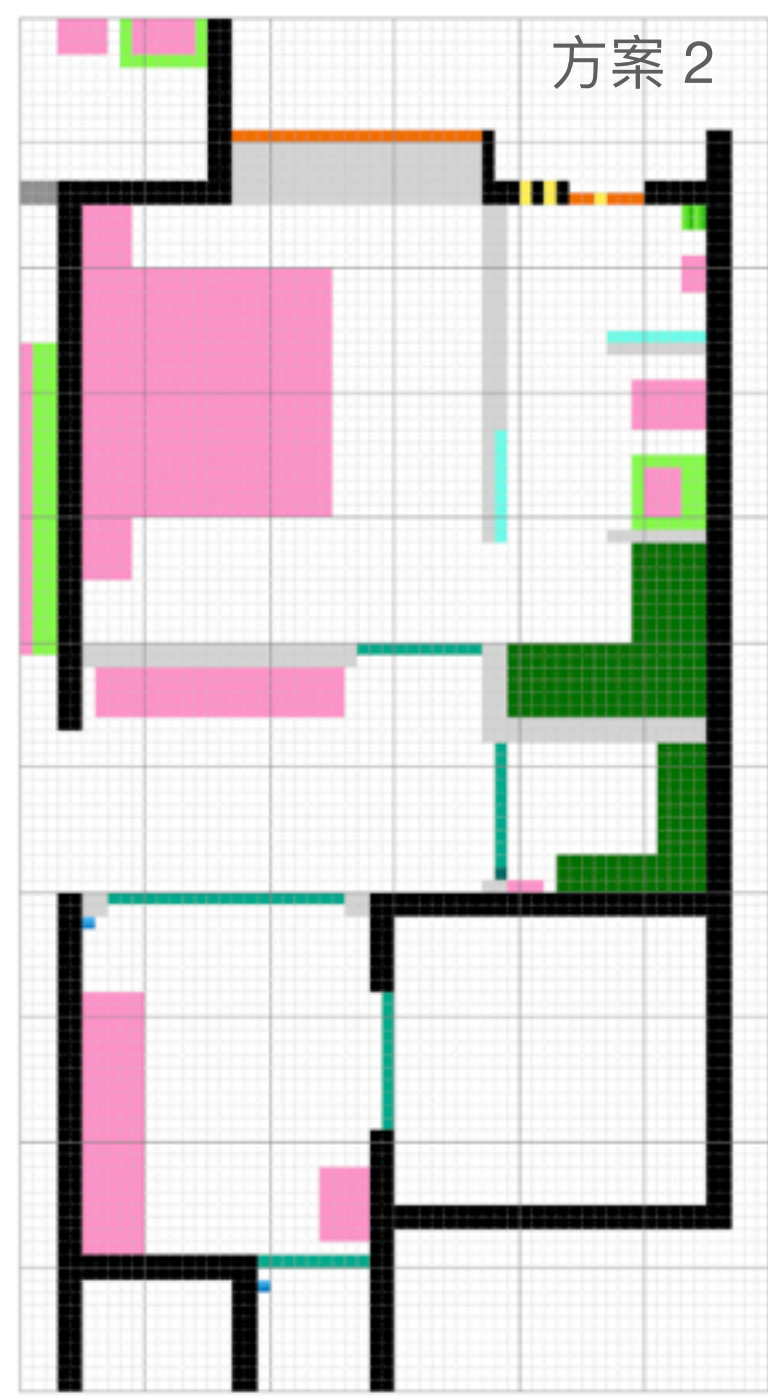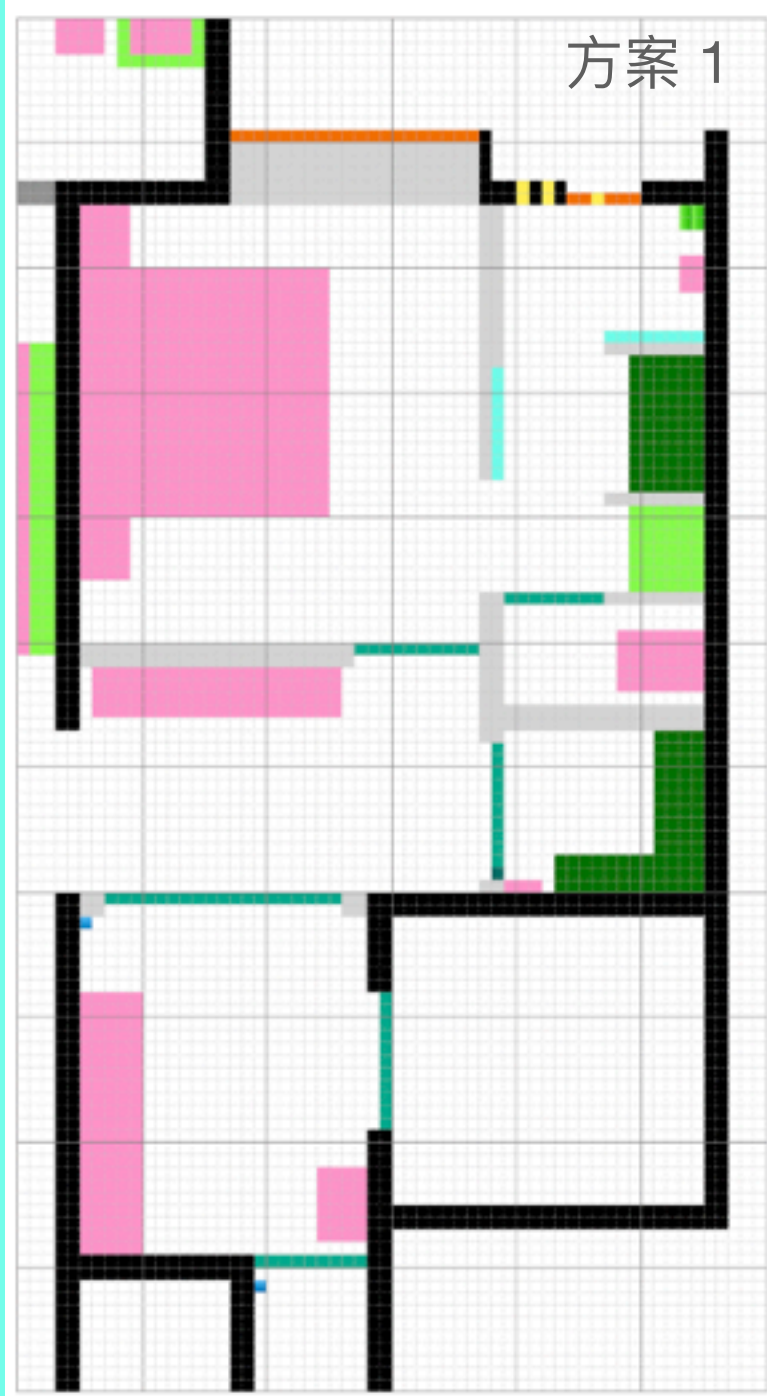

从大门玄关右转是行李室, 注意镜子两边有走道, 内侧(图片上方) 是浴室, 外侧 (图片下方) 是卧室, 类似于方案 1 加 3 的开门模式 (洄游动线)




从次卧到次卫可以参考红珠山的拉门. (右边电视后面是拉门)



另一种卧室与浴室的开放方式: 两片对开的推拉门 (方案四, 床头转向飘窗方向)

次卧布局 (目前选择)

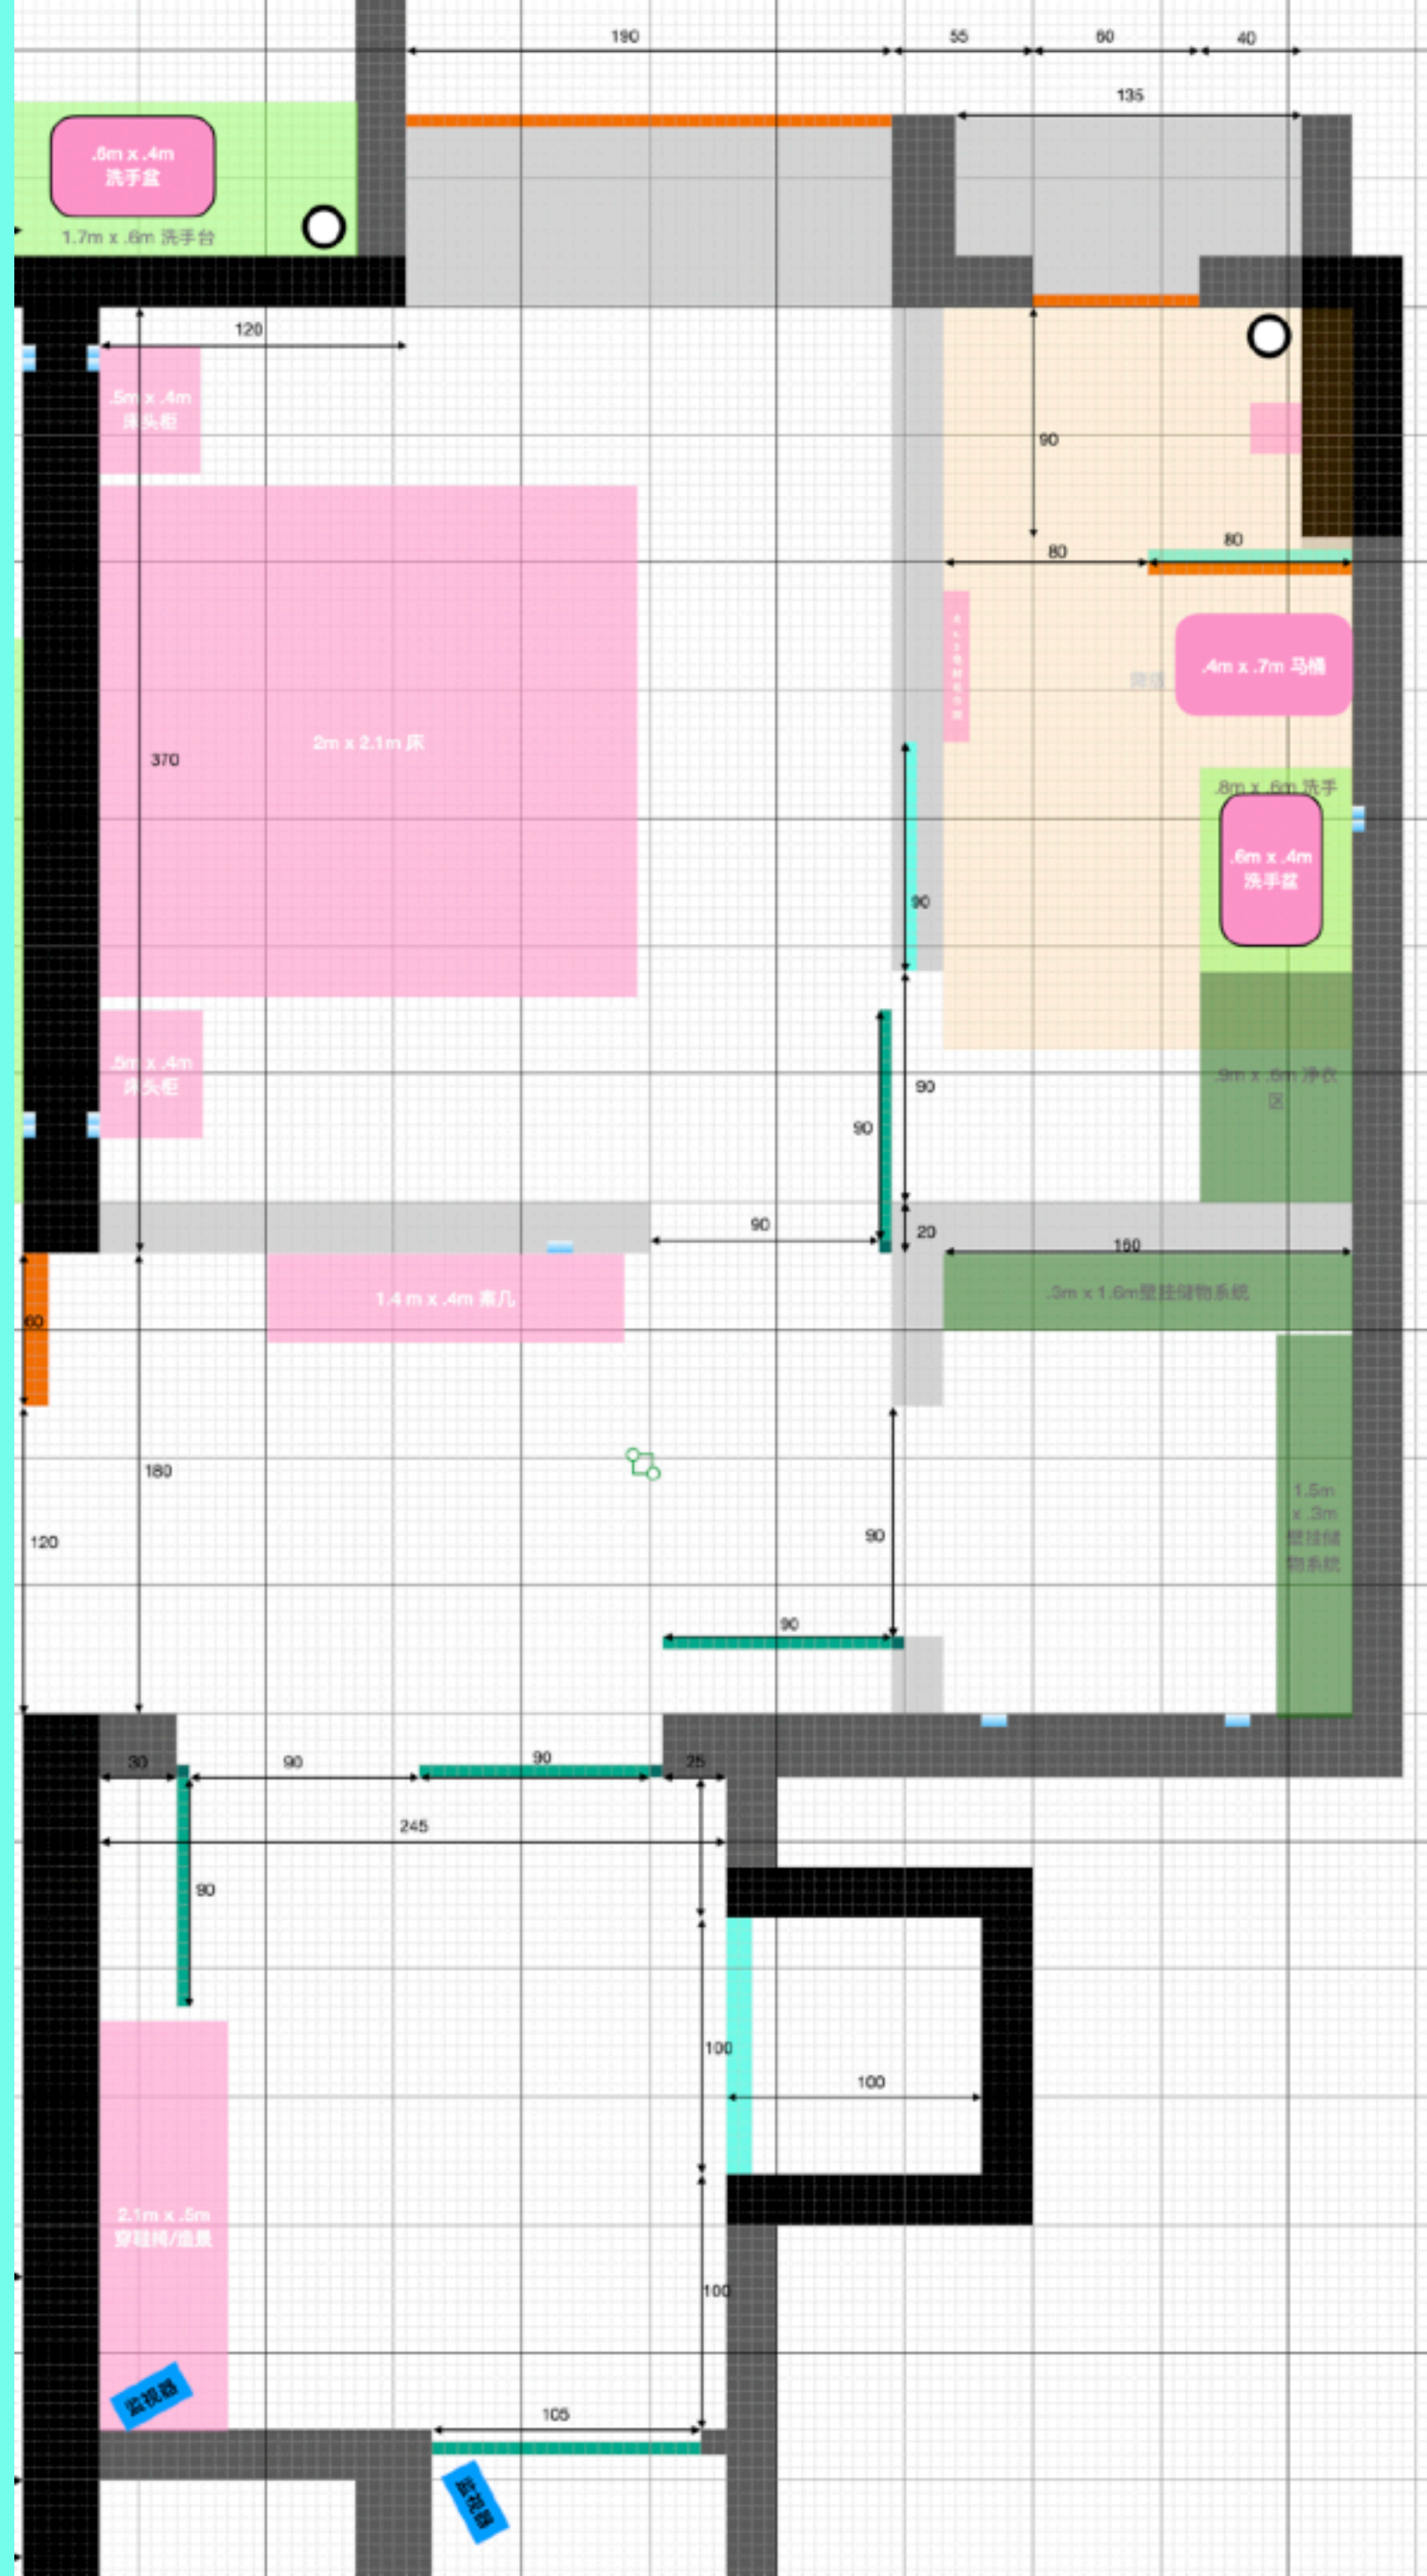

重点:

换回样板房布局, 另外次卧与次卫优先考虑华为智能家居, 如:

使用箭牌淋浴器做无冷水

使用慕斯智能床

如果不使用中央空调, 优先考虑使用美的智能空调(注意他只有传统吊机) 有半高的外机可以放在浴室窗户外而不会遮挡开窗

其他:

优先考虑在淋浴房使用中央集水器, 然后加上长条地漏作为淋浴房隔断



长条地漏可以跟淋浴门做在一起, 门是上吊滑门, 地面是与地漏整合的限位器