

次卧空间

次卧佈局

次卧:

方案一：酒店配置

- 亮点：淋浴房与厕所在次卫的两侧, 理论上互不影响
- 隐忧：次卫镜子对房间

方案二：原始配置





- 亮点：床不会对着镜子, 次卫可以有多个独立分区
- 隐忧：次卫空间一部分用做柜子. (净衣或储藏室) 整体次卫可用空间较小. 另外洗脸盆太小了. 整体尺寸需要调整

方案三：

- 亮点：次卫入口与次卧入口不互相遮挡
- 隐忧：整体动线是最长的, 排水有疑问

方案四:


- 亮点: 套房最开放布置
- 隐忧: 次卧与次卫没有分隔, 床头直视镜子

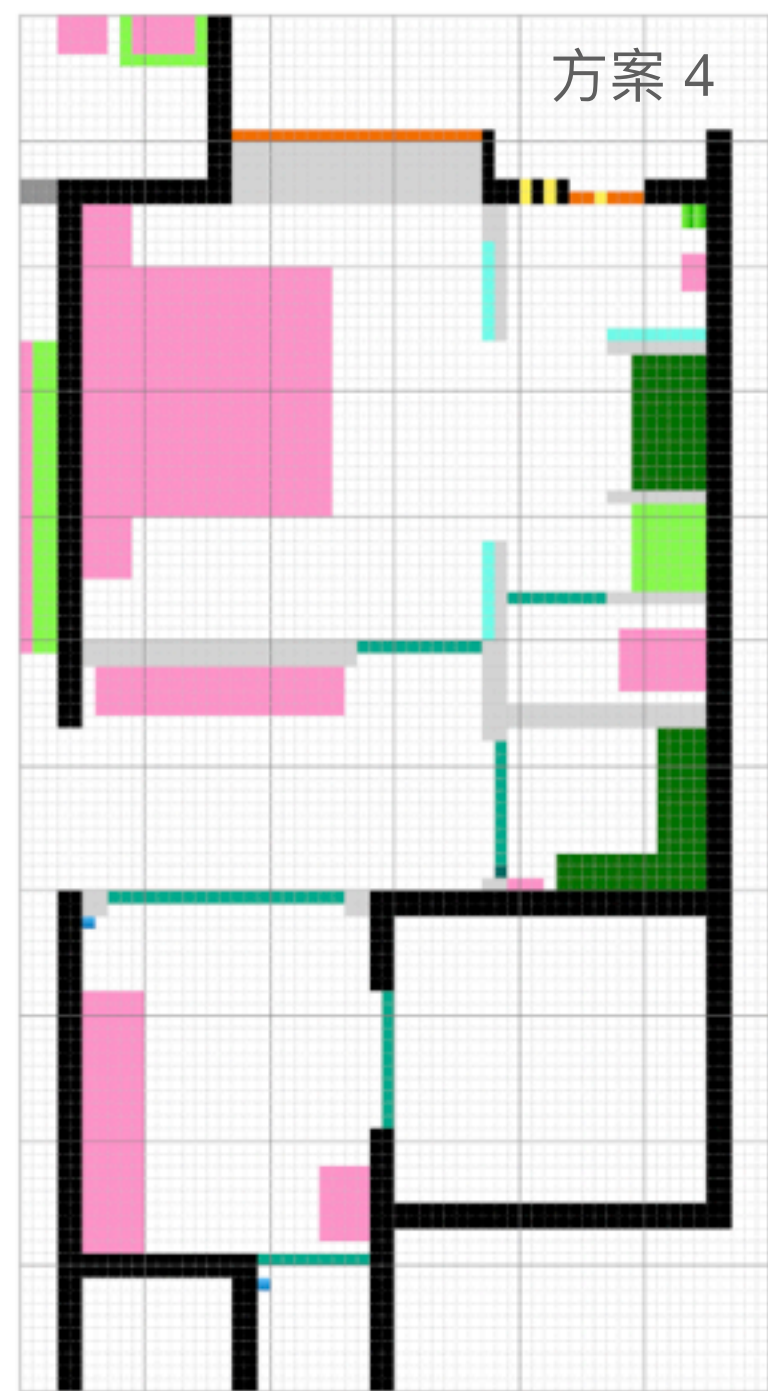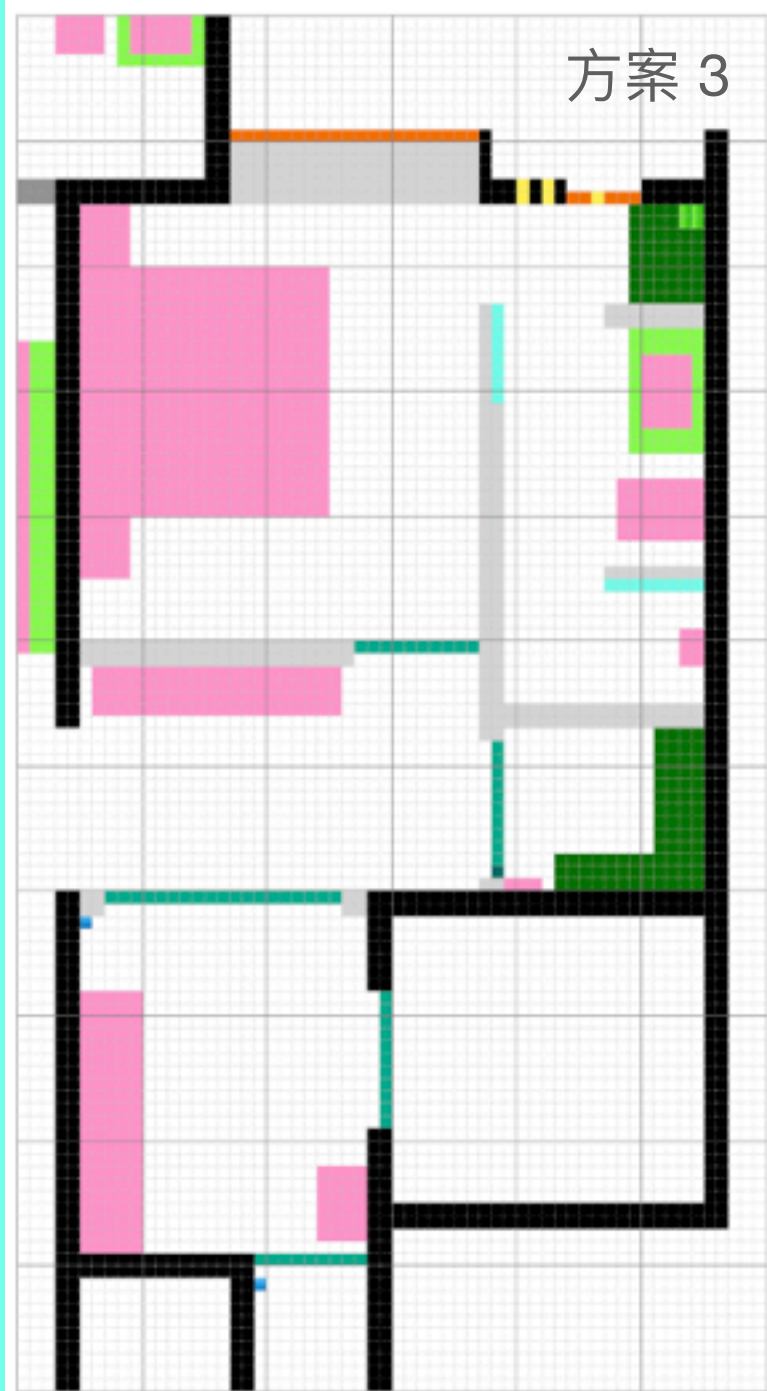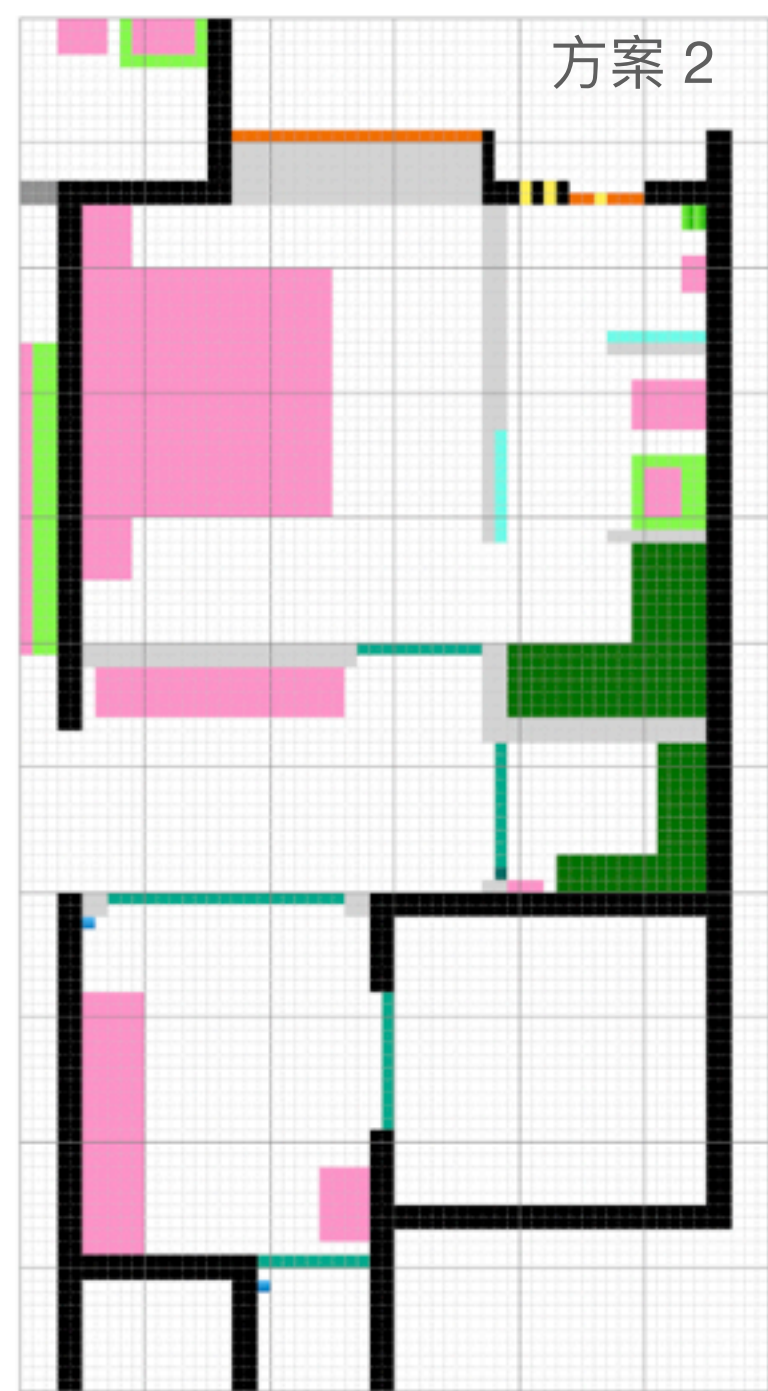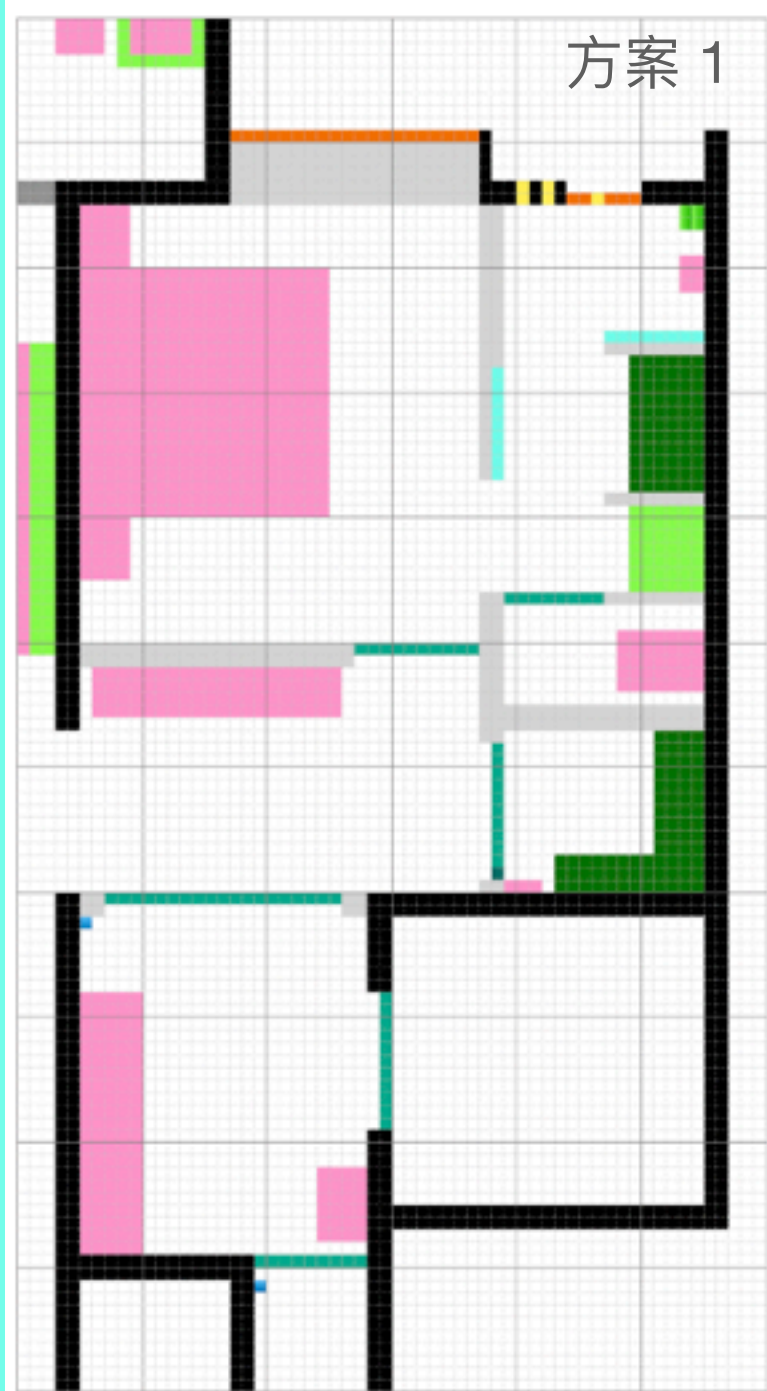

从大门玄关右转是行李室, 注意镜子两边有走道, 内侧(图片上方) 是浴室, 外侧 (图片下方) 是卧室, 类似于方案 1 加 3 的开门模式 (洄游动线)



从次卧到次卫可以参考红珠山的拉门. (右边电视后面是拉门)

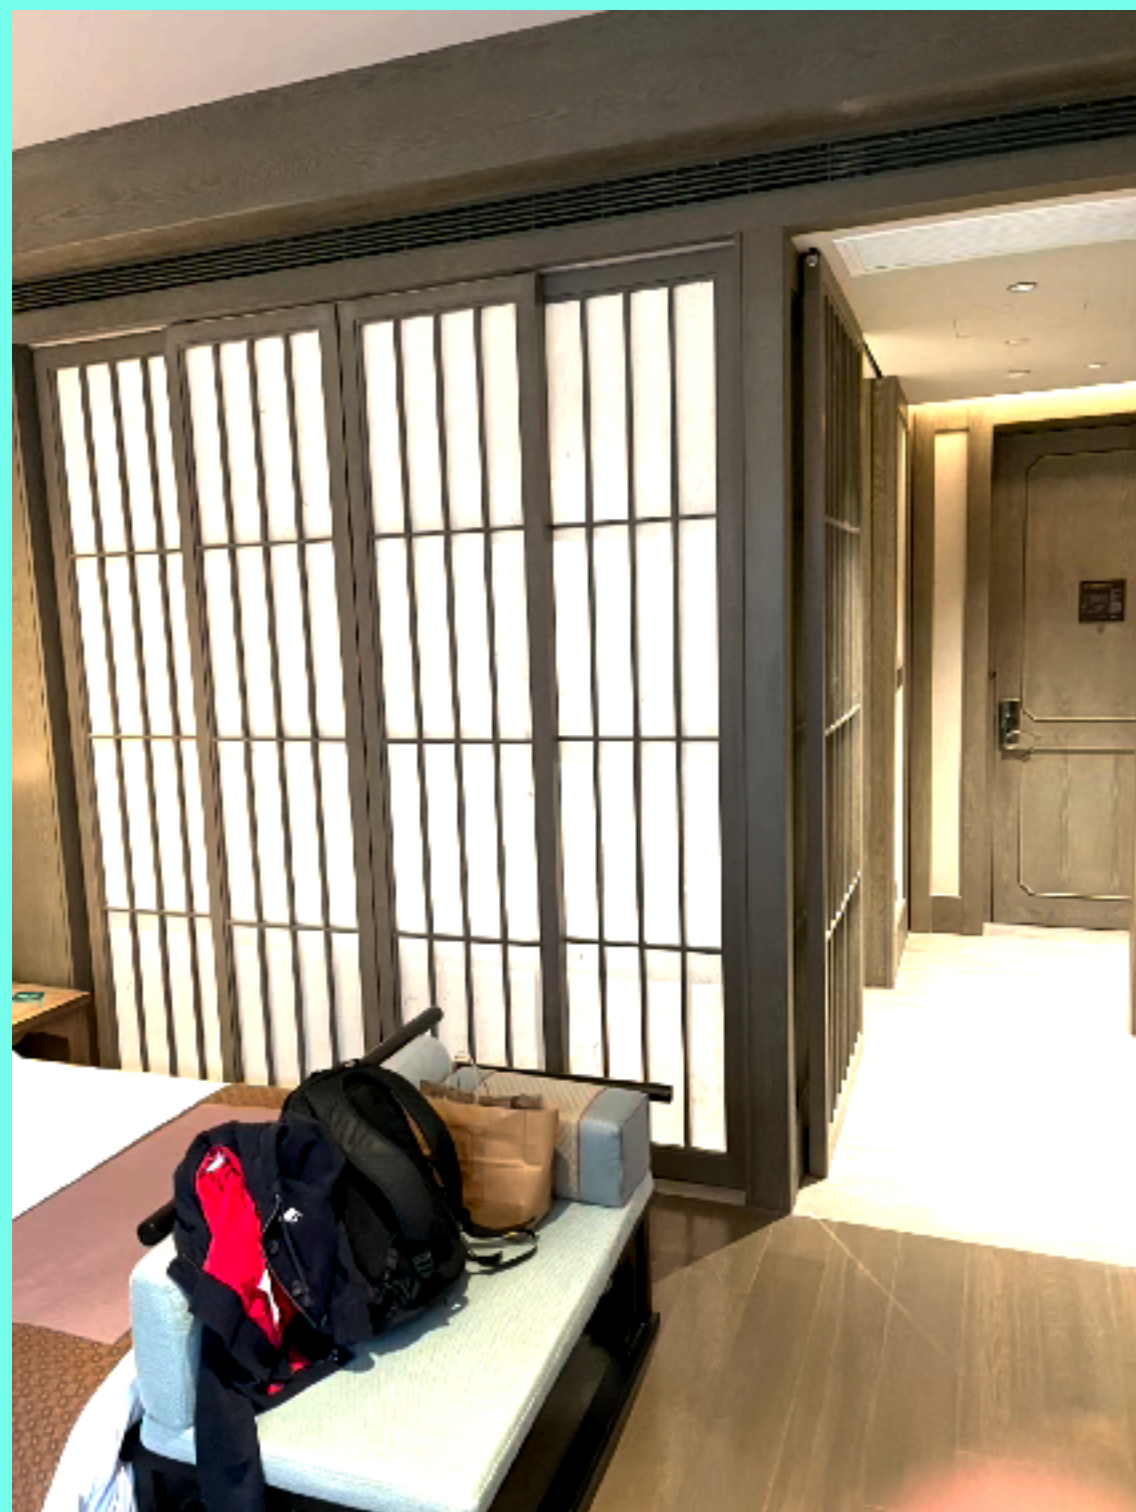

另一种卧室与浴室的开放方式: 两片对开的推拉门 (方案四, 床头转向飘窗方向)