


主卧佈局




我们还是用了中国传统的人字顶

靠近主卫玻璃墙可以放中式衣架做造型 (图左)

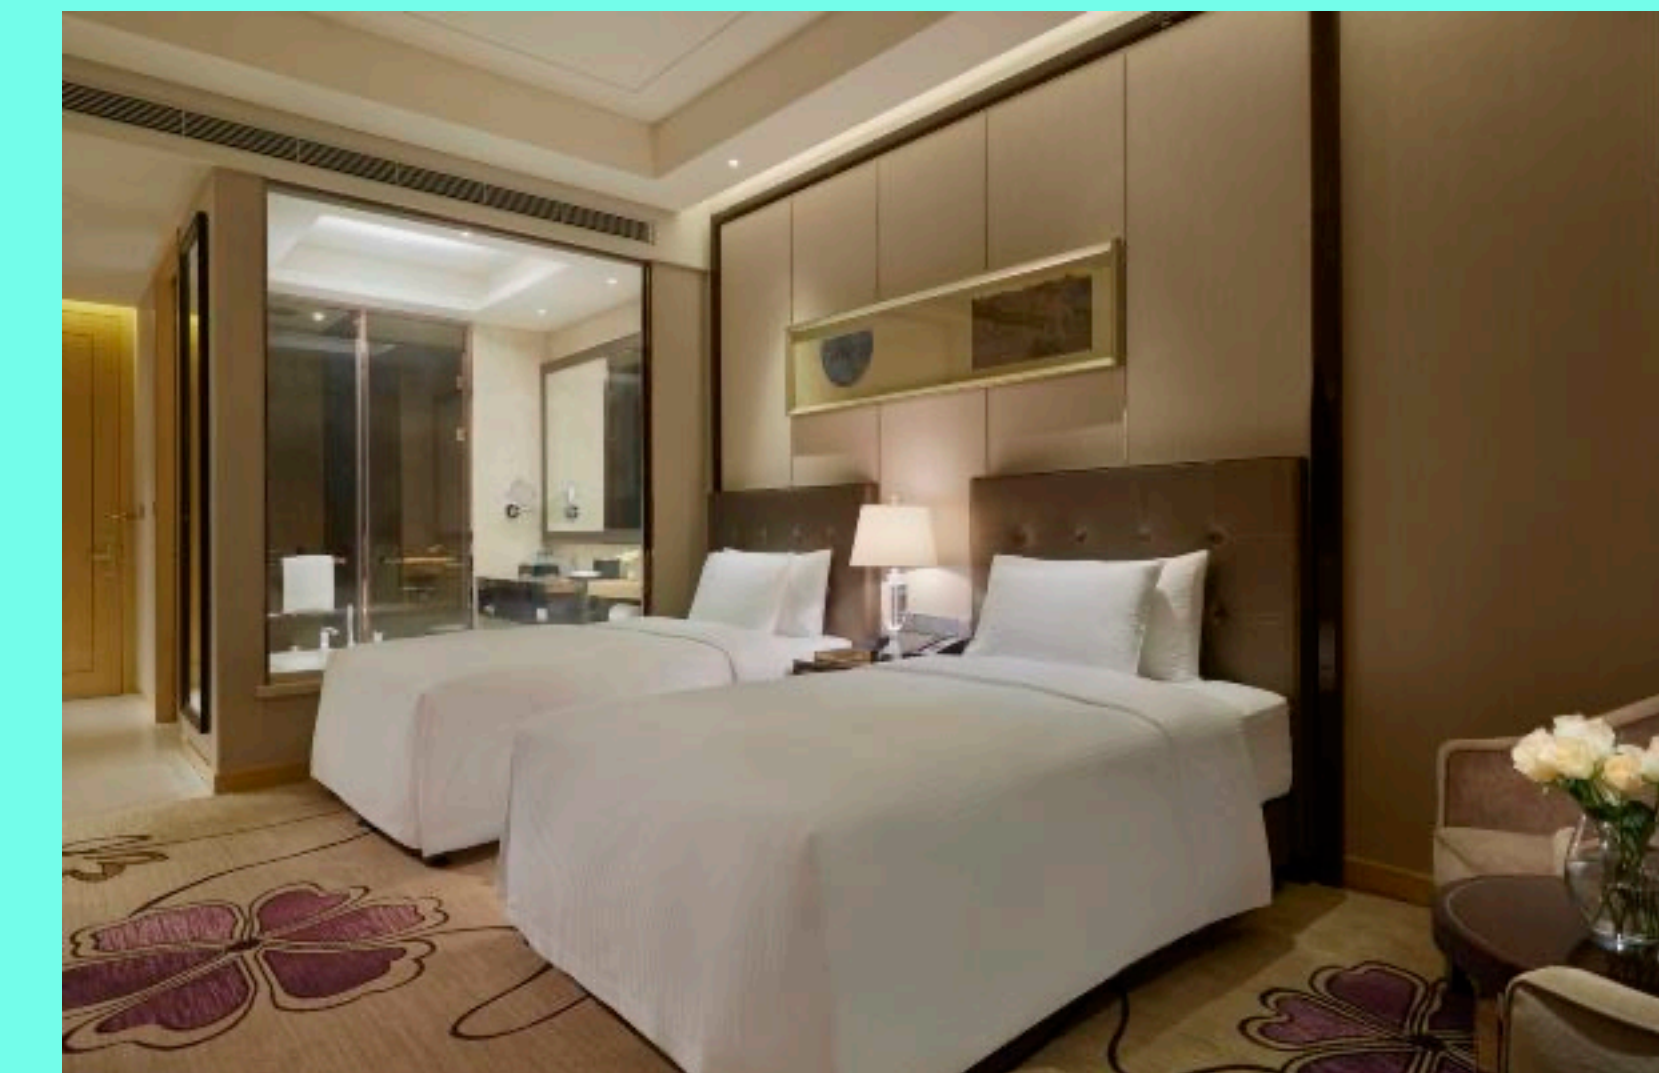

标准酒店玻璃隔墙

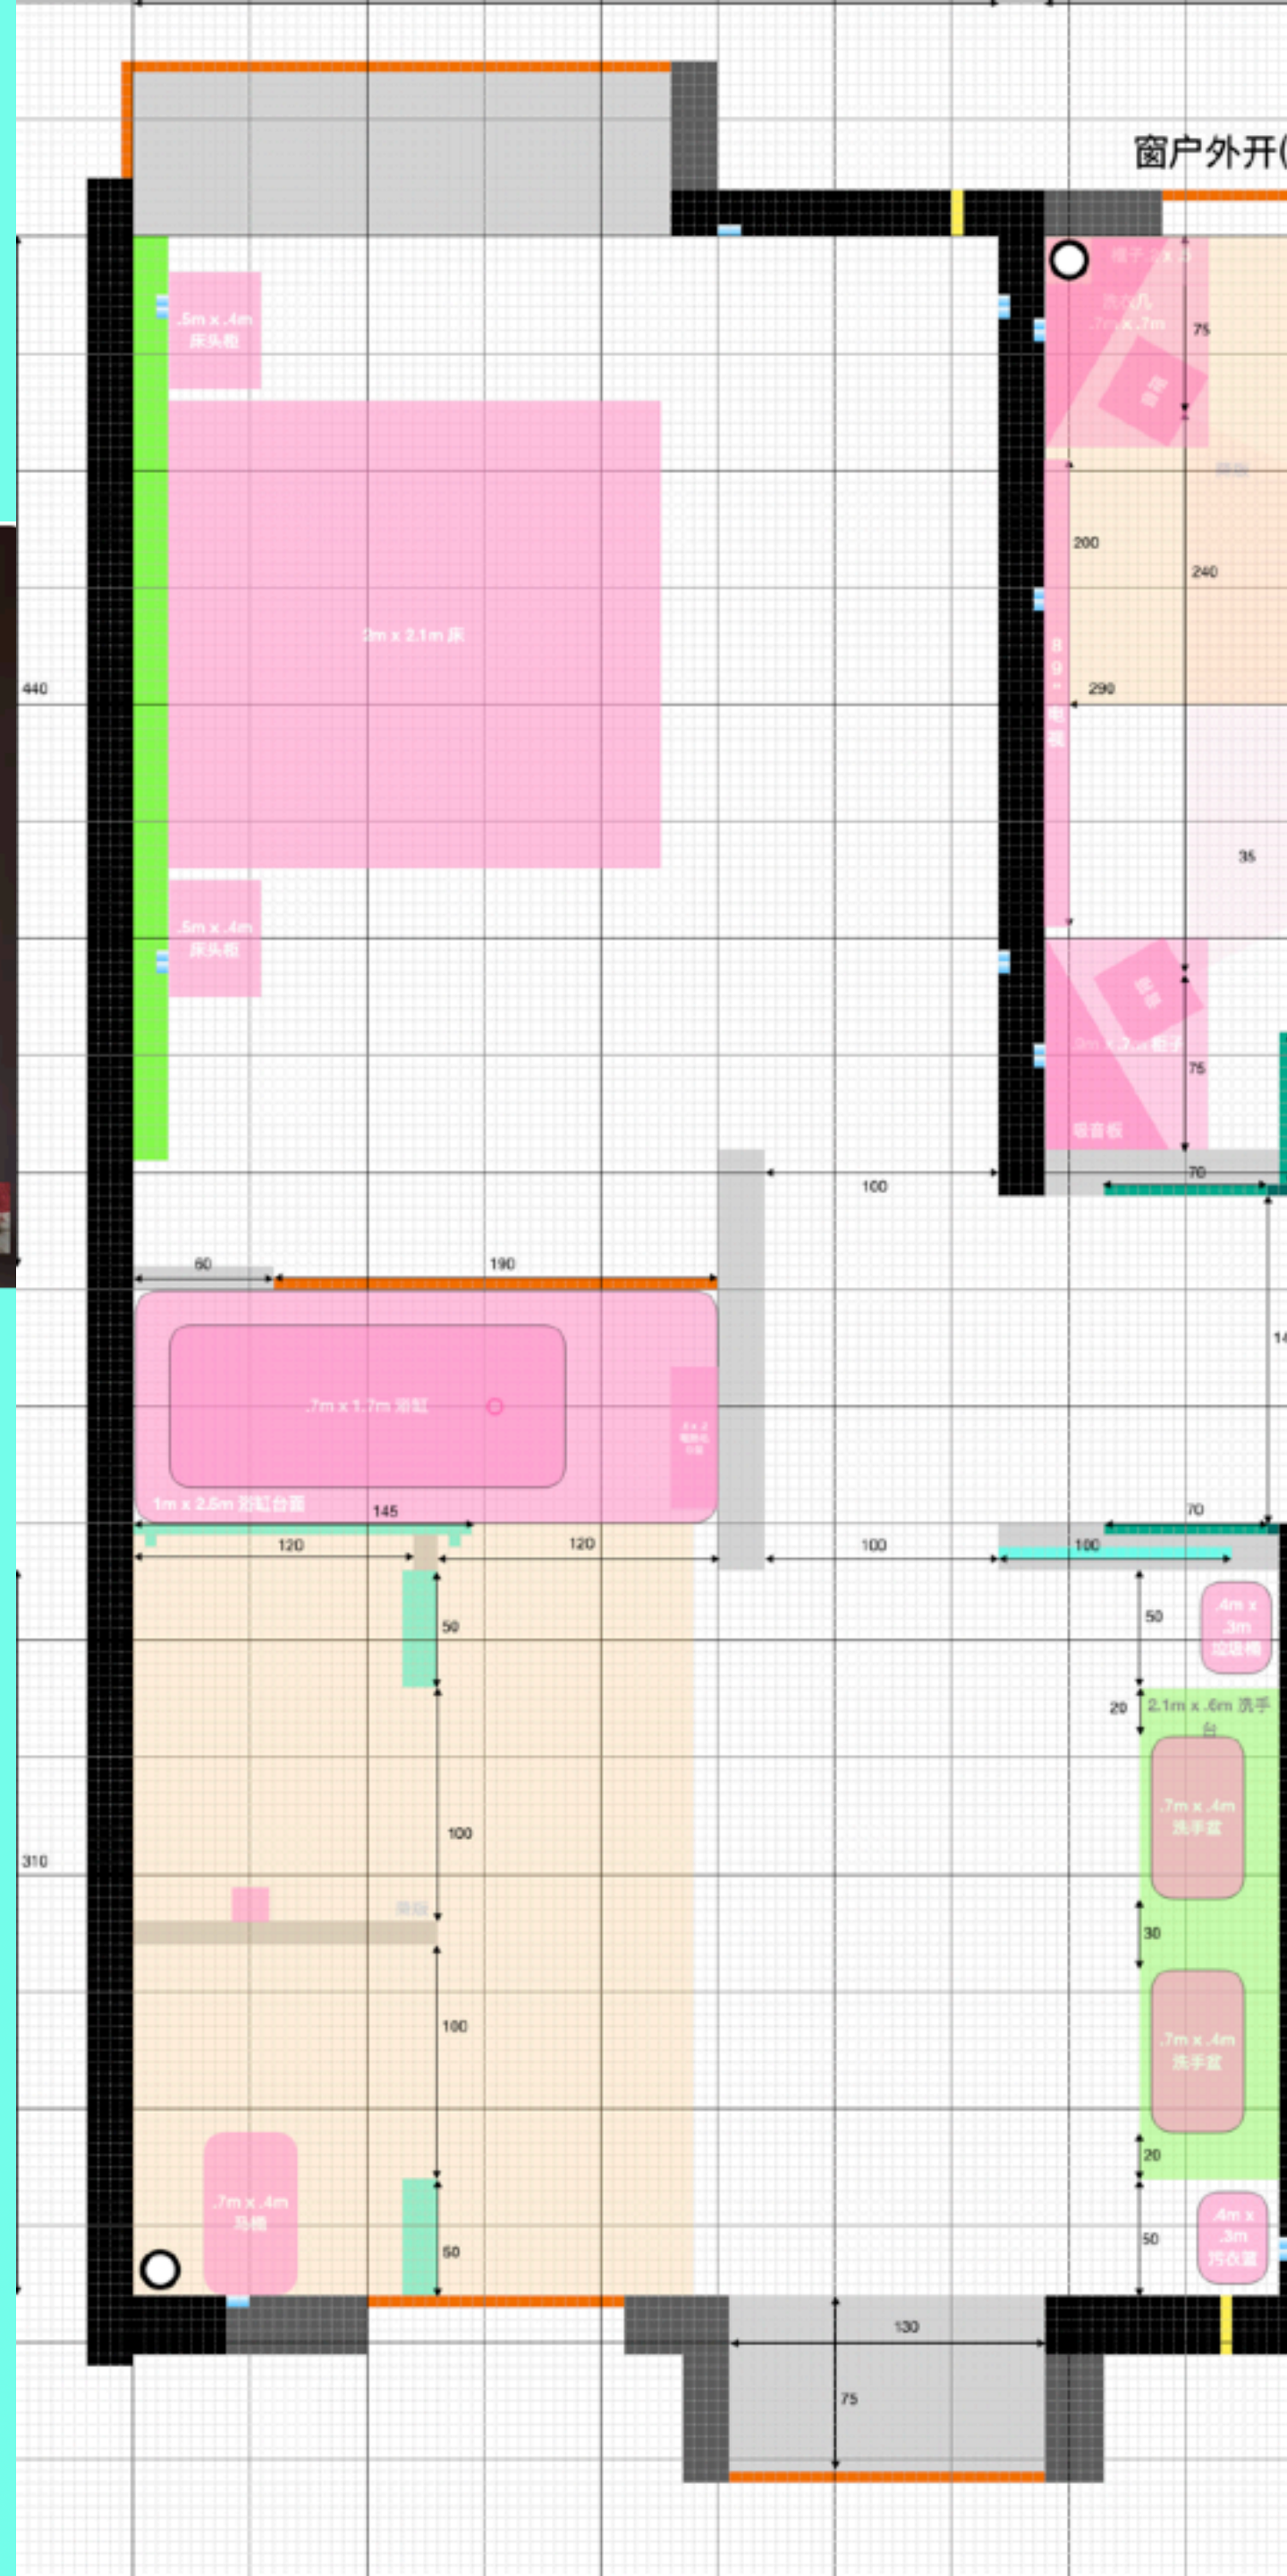

使用酒店布局, 将浴缸布置余原走廊位置, 这样能有最完整的主卫布局, 另外因为浴缸不会占用原走道宽度, 剩下的还可以加回主卧, 增大主卧宽度



除了玻璃外, 我也住过完全开放式设计. 不过这种实用度存疑

主卧 - 15

主卧求静，须兼顾邻户(上/下)隔音。 可以直接参考酒店房间布局

- 15a: 高优先度
 - 需要有好的隔音
 - 需要有感应起夜小夜灯
 - 需要有智慧家庭康养传感器 (防跌倒, 呼救)
- 15b: 中高优先度 (倾向安装)
 - 动线需要考虑未来轮椅进出
 - 尽可能使用拉门
- 15c: 一般优先度 (有疑问)
 - 希望能有架子床
 - 有考虑使用华为合作的智慧床(不需电动骨架, 但床垫本身的软硬自动调整与监控可以考虑)
- 15d: 低优先度 (倾向不安装)
 - 无
- 15e: 黑名单
 - 主卧不要电视
 - 主卧不要床尾凳