

客厅前阳台-实景-6a2

前面邻居加看向我们家 (对方后阳台也是封好的)





南北两个阳台可



从邻居看向北方的景色. (注意实际上看得很清楚, 这只是示意邻居布置与可能使用的方式.)


客厅前阳台-其它-6c0

示意图, 格栅, 防风卷帘, 晾衣架与落地窗的关系

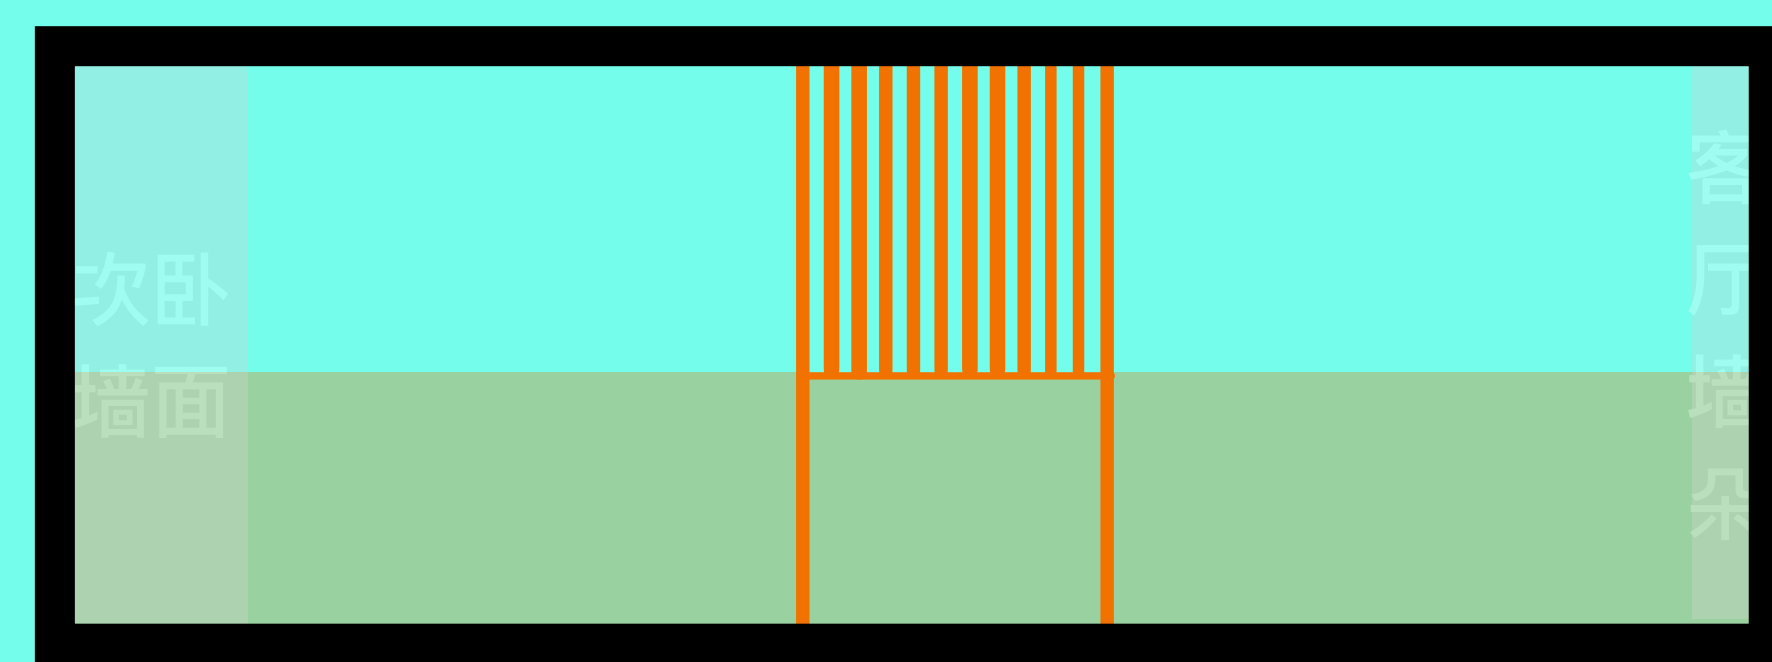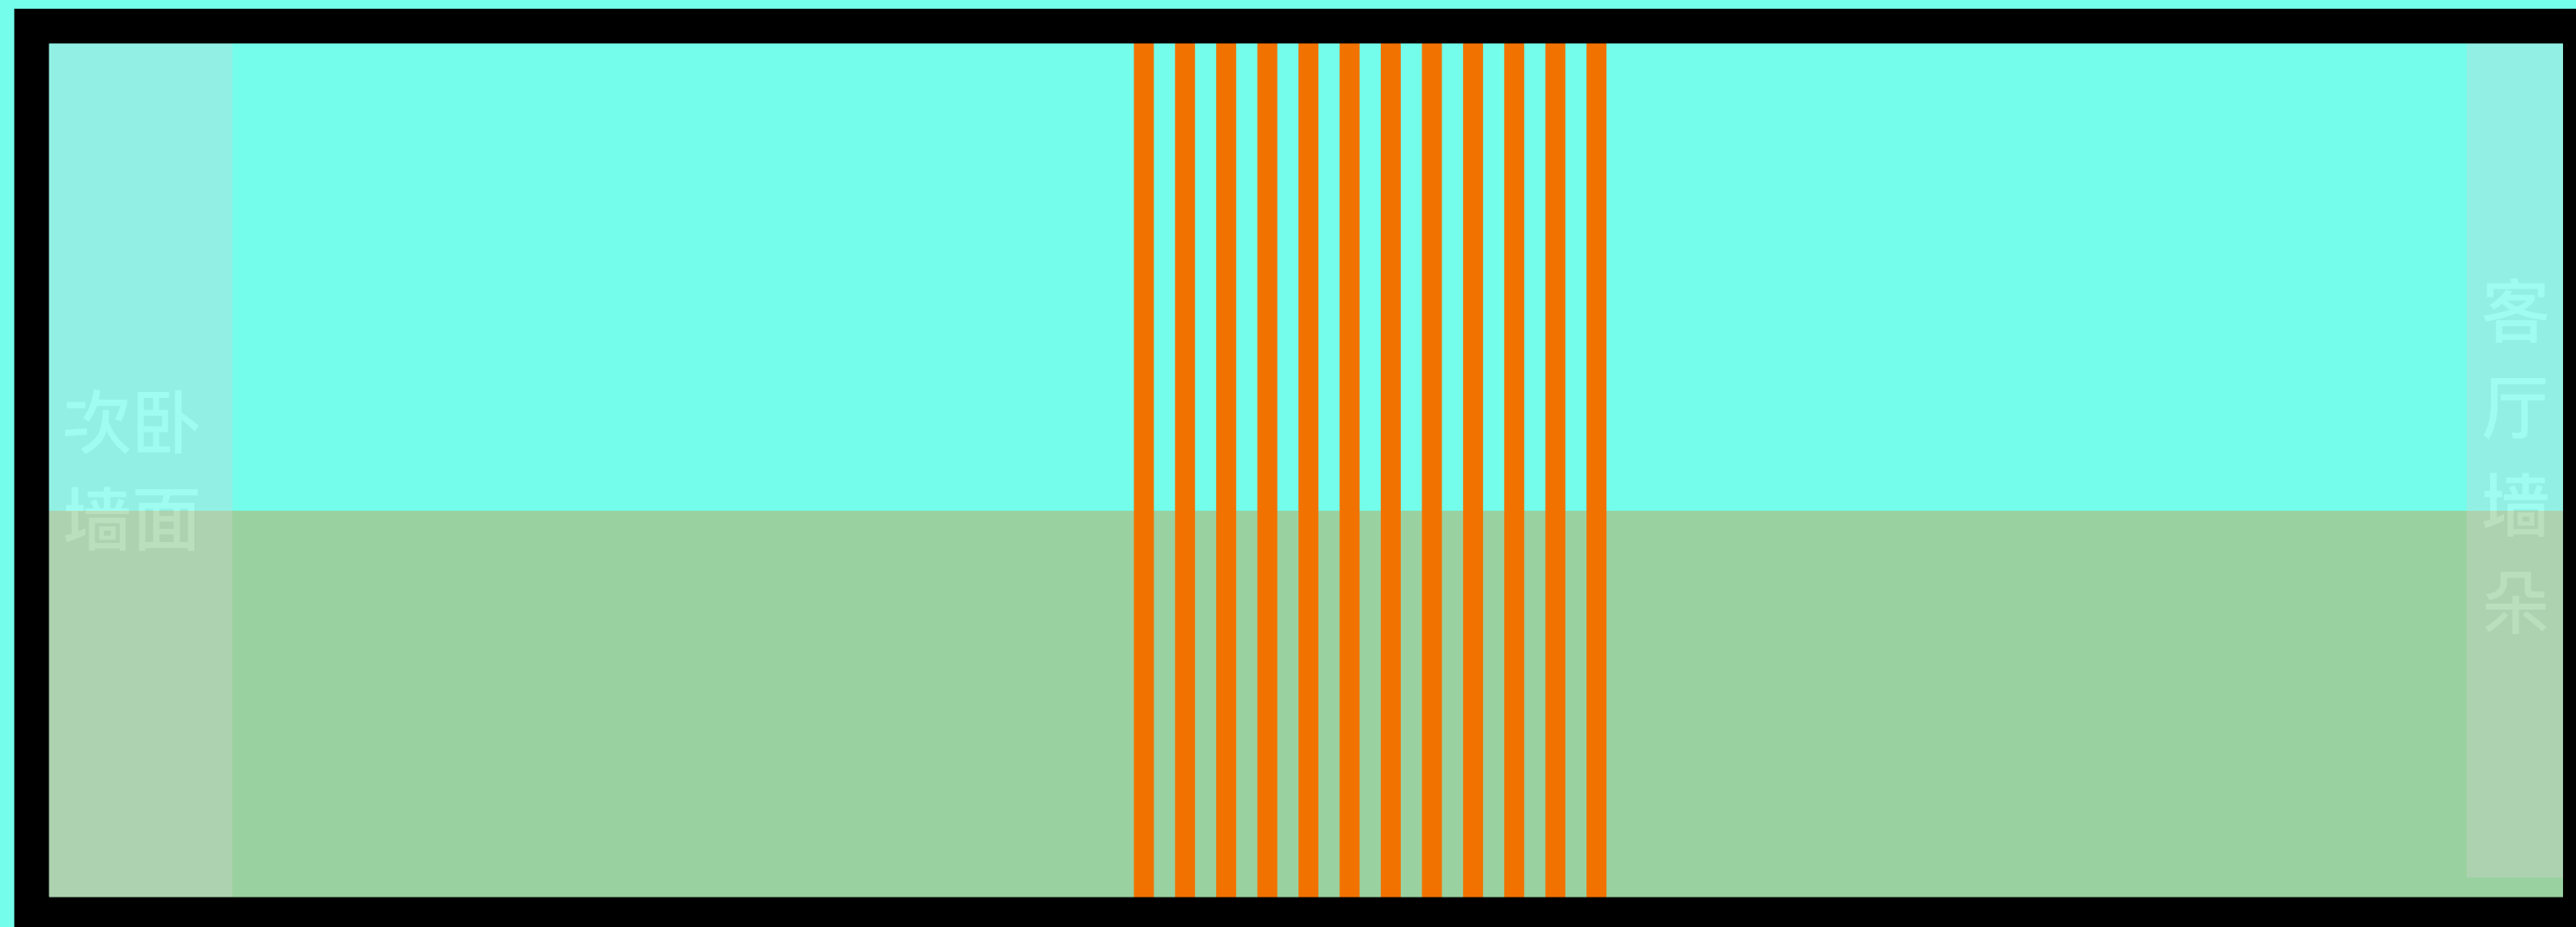

扶手高度示意图, 注意左右两侧还是落地的且内含防风卷帘轨道

由前栋楼看向我们房子, 格栅可以落地, 也可以只做到扶手高度

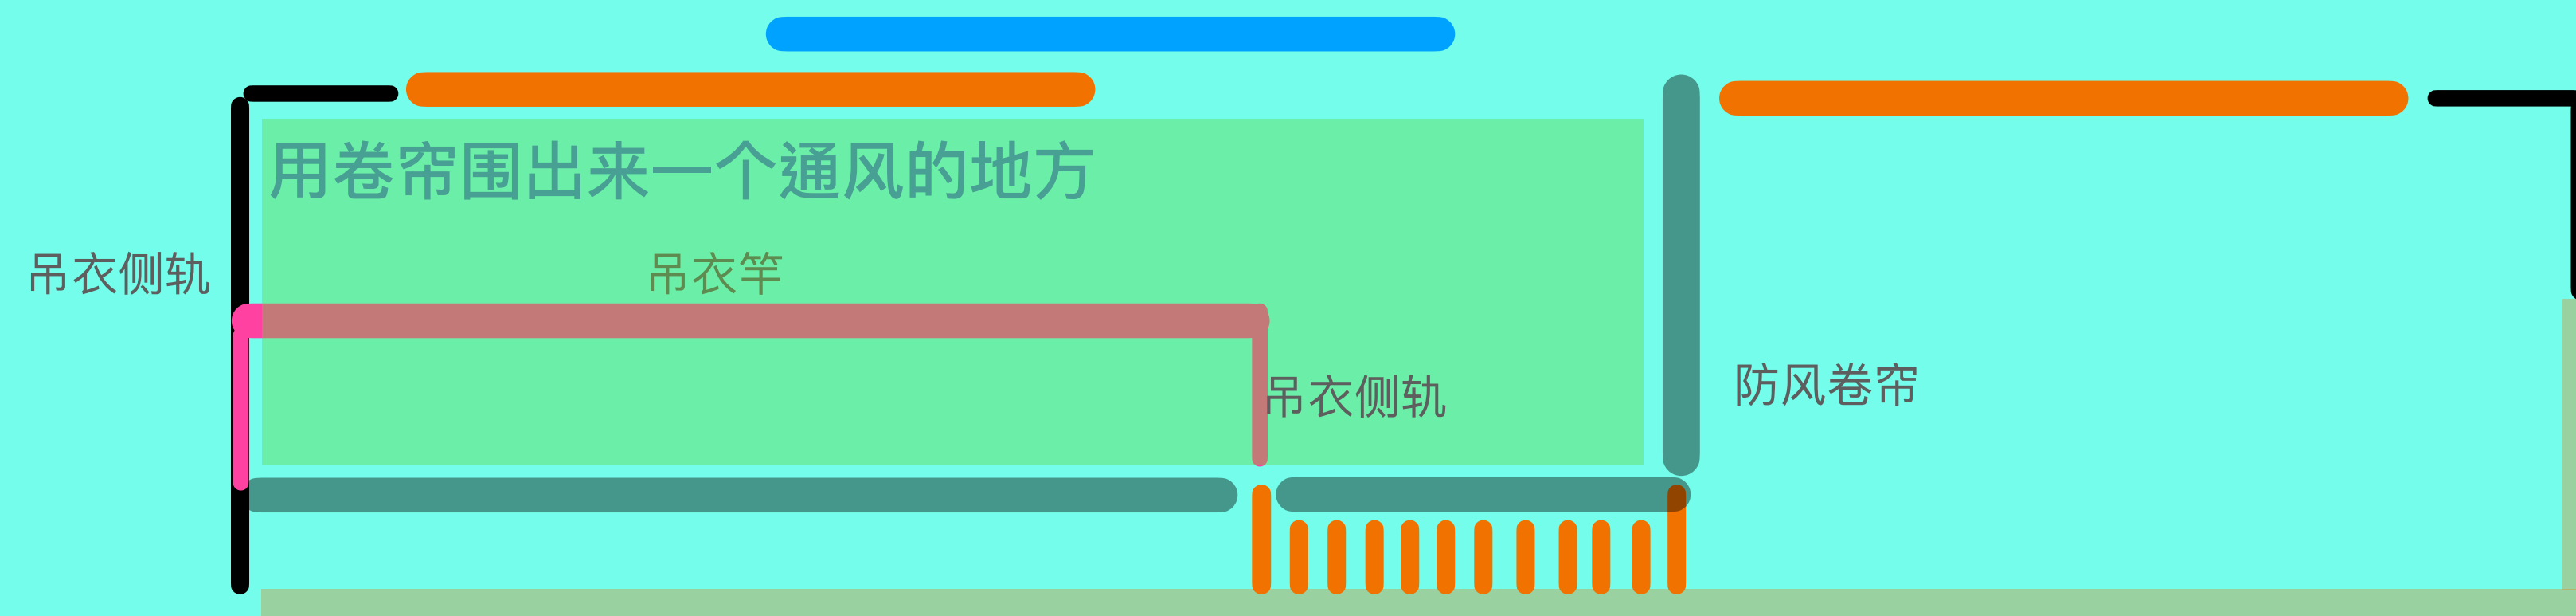

由上往下看, 格栅, 防风卷帘与吊衣竿的关系

将吊衣竿立柱跟扶手装一起

