


## 特殊区域布局 (目前选择)

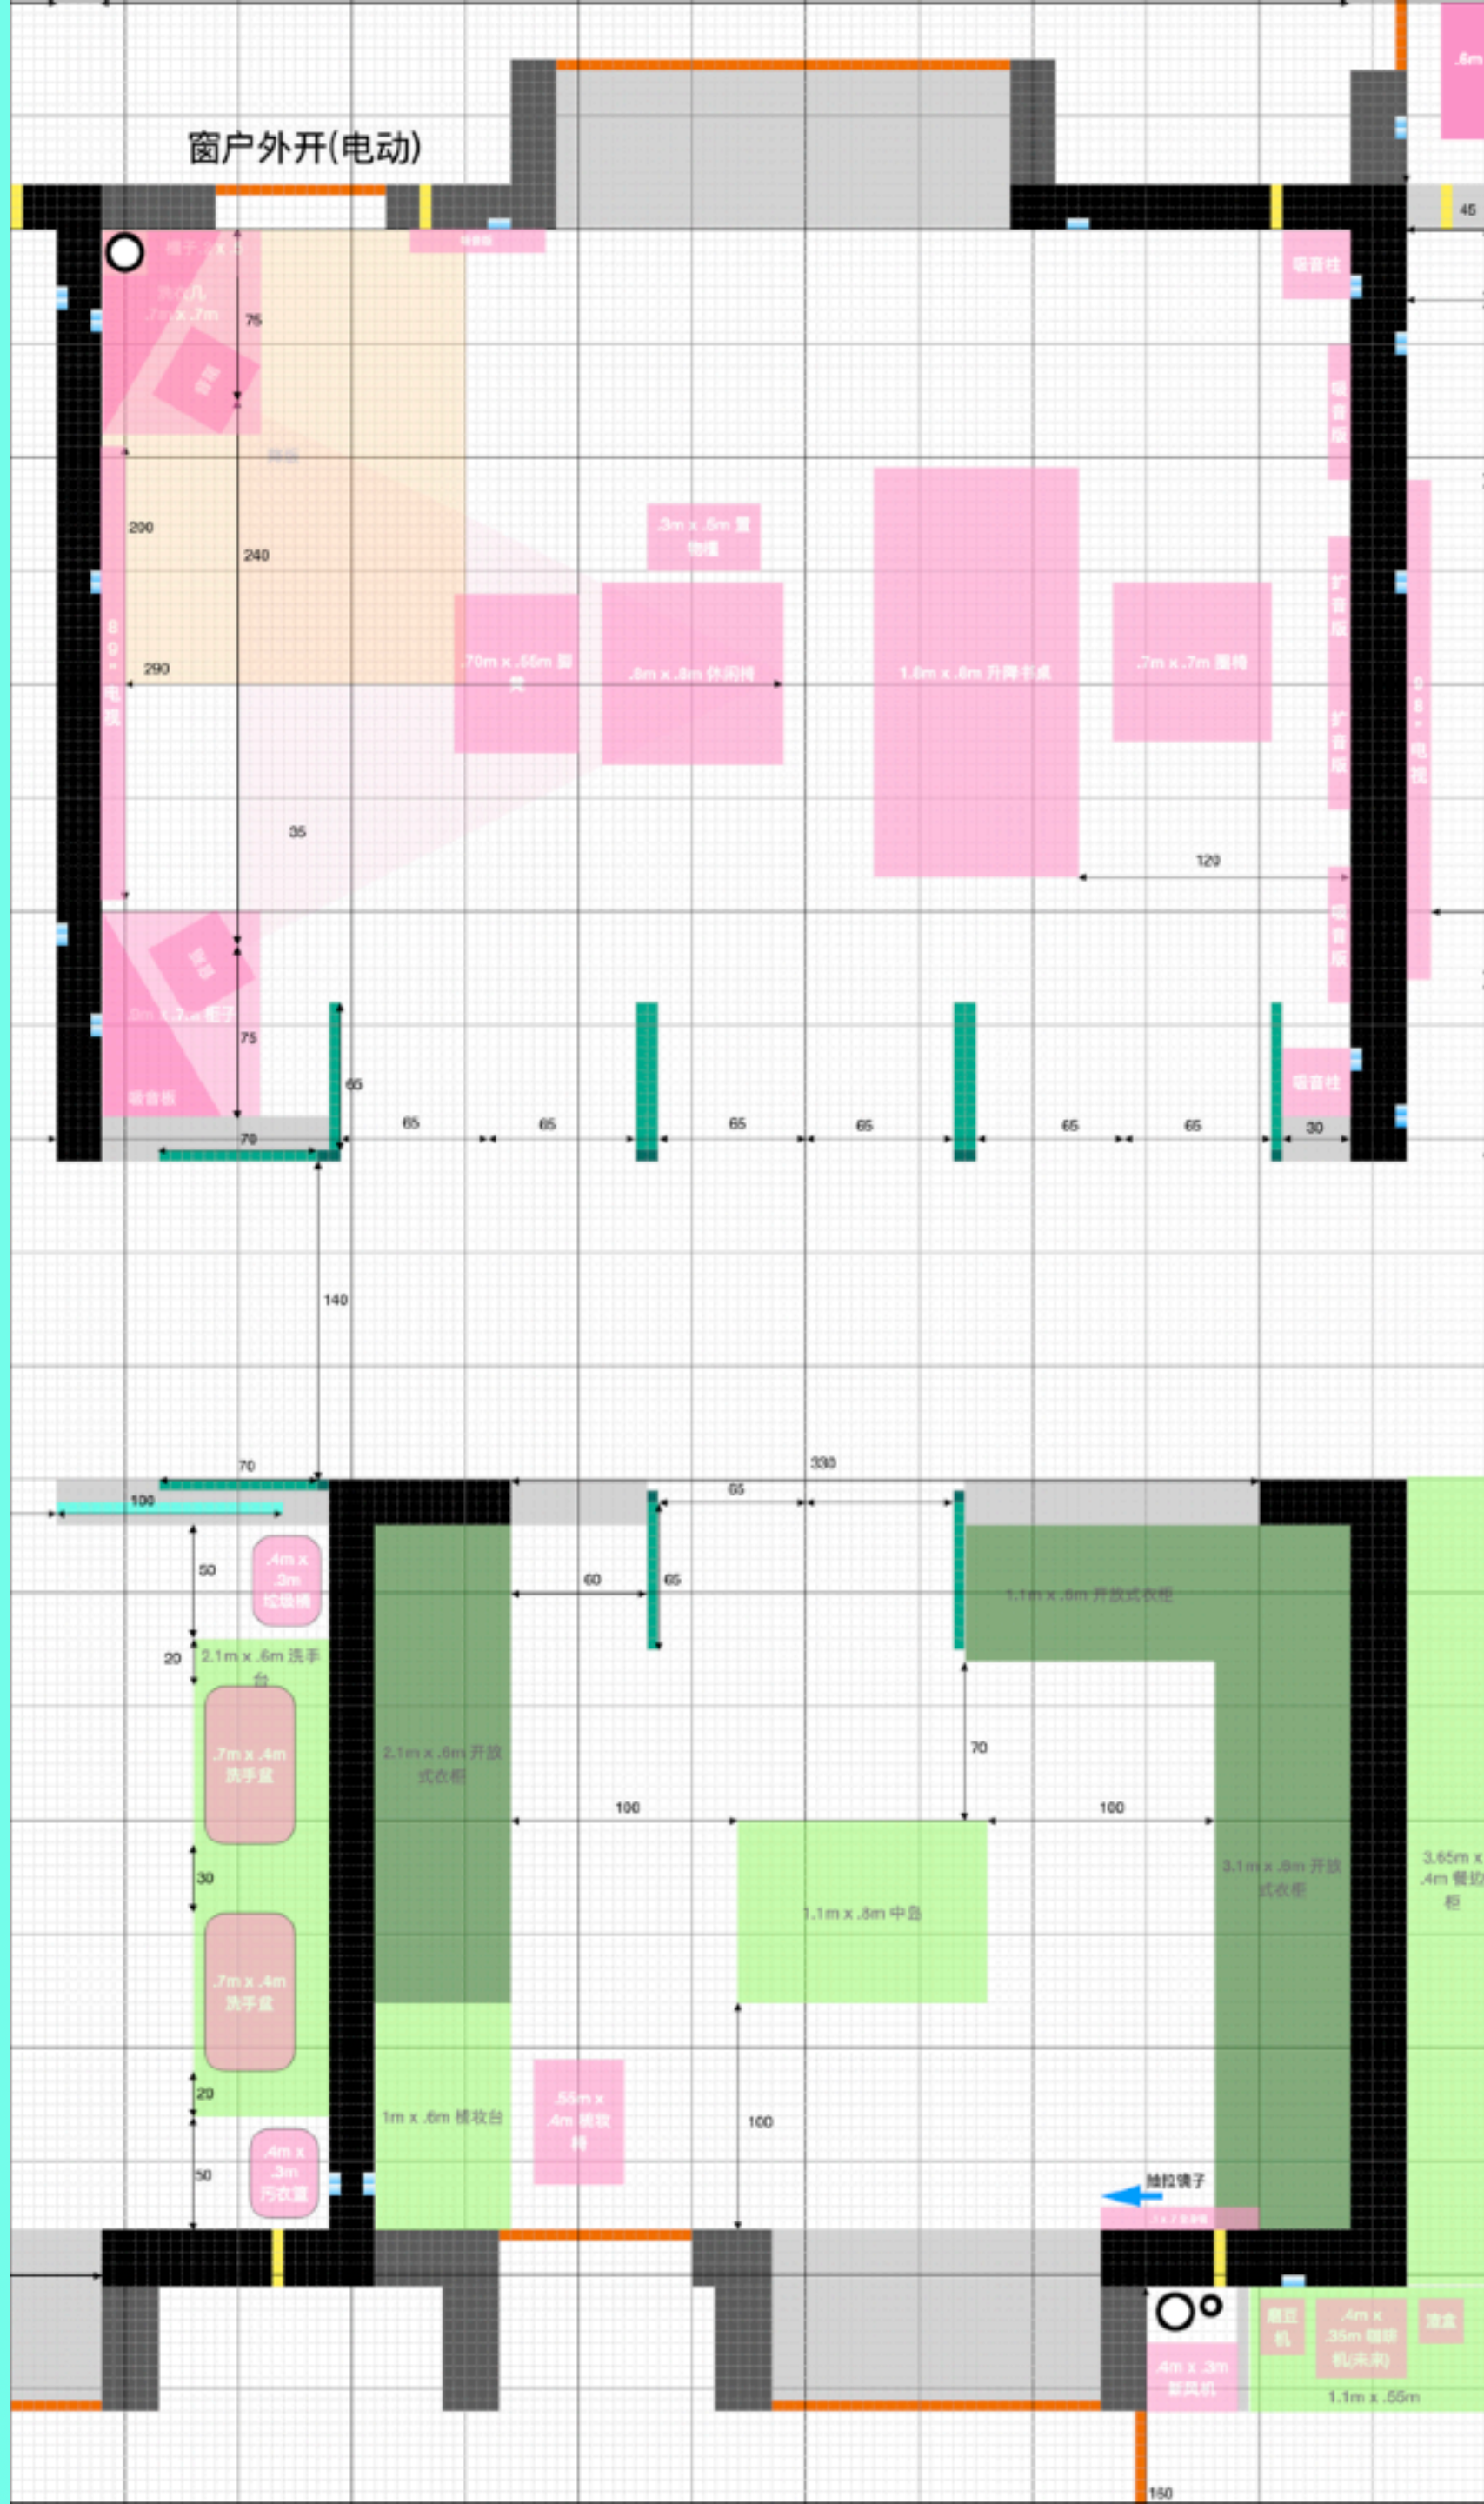

### 重点:

书房主要为单人使用

## 需要舒适的休闲椅

需要升降书桌(不需要对应的人体工学椅, 只要漂亮就行)

洗烘一体机放在柜子里, 另外一边的柜子内可以是空的, 事后再找置物架. 另外柜子需要门. (封闭或开放都可以)

使用洗烘一体的原因是烘的功能主要服务于梅雨季, 其他时间以晾晒为主.

注意柜子上还会在角落安装三角形吸音柱来盖住下水管

## 更衣室

需要中岛,走道应该尽可能宽敞

需要梳妆台, 注意尽可能不要台面下的抽屉, 腿会比较好放, 且扶手不会与抽屉发生冲突. 梳妆台收纳可以坐在旁边的抽屉

中岛两侧应该做成开放格, 抽屉做在飘窗方向, 朝走道应该以美观为主

大型物件, 如冬季棉被, 优先考虑放在中岛. 四周全部都是开放式衣柜. 吊衣服为主, 可以有少量抽屉. 注意下面最好为开放式, 允许扫地机进入

# 书房/影音室 - 12

未来儿子专用书房兼双声道听音室，需预留 5.0.4 管道, 但很大概率只会使用 2.0 声道；2030 年前暂不购入影音设备，先作洗衣房使用。空间配置仅需考虑单人听音。

- 12a: 高优先度
  - 洗烘一体机放置在半高的柜子里, 音箱会放在柜子上.
    - 注意!! 音箱可能重达 80kg (每只). 必须考虑承重与震动. (最少 20kg 每只, 计划是约 60kg 每只)
  - 需要有声学处理(吸音为主)
  - 家具安排上以单人使用为主, 不需两个位置. 不过听音位置旁应该有小矮凳来放电子产品 (如遥控器/平板)
  - 书桌, 小矮凳, 与两个柜子应有管道互通. 方便拉线
  - 需要预留喇叭信号线与电源的管道(主动式喇叭)
- 12b: 中高优先度（倾向安装）
  - 需要有一张升降书桌
  - 需要有与书桌配套的椅子（不需人体工学椅, 大部分会站着使用书桌）
  - 需要有一张带头枕的休闲椅(可以躺下与含脚蹬的那种, 如伊姆斯躺椅, 可寻求中式款式) 不要皮制或布艺, 竹或藤制品更好
- 12c: 一般优先度（有疑问）
  - 无
- 12d: 低优先度（倾向不安装）
  - 无
- 12e: 黑名单
  - 无
- 12f: 未來設備（2030 年後）
  - 音响设备 (两声道), 需要房间其他配套在这次装修就完成. 2030 买音箱放上后就可以直接使用. 其余声道是更久远的事. 只需留管线就好. (需留信号与电源, 如果未来使用也会使用主动式音响)