


次卧布局 (目前选择)

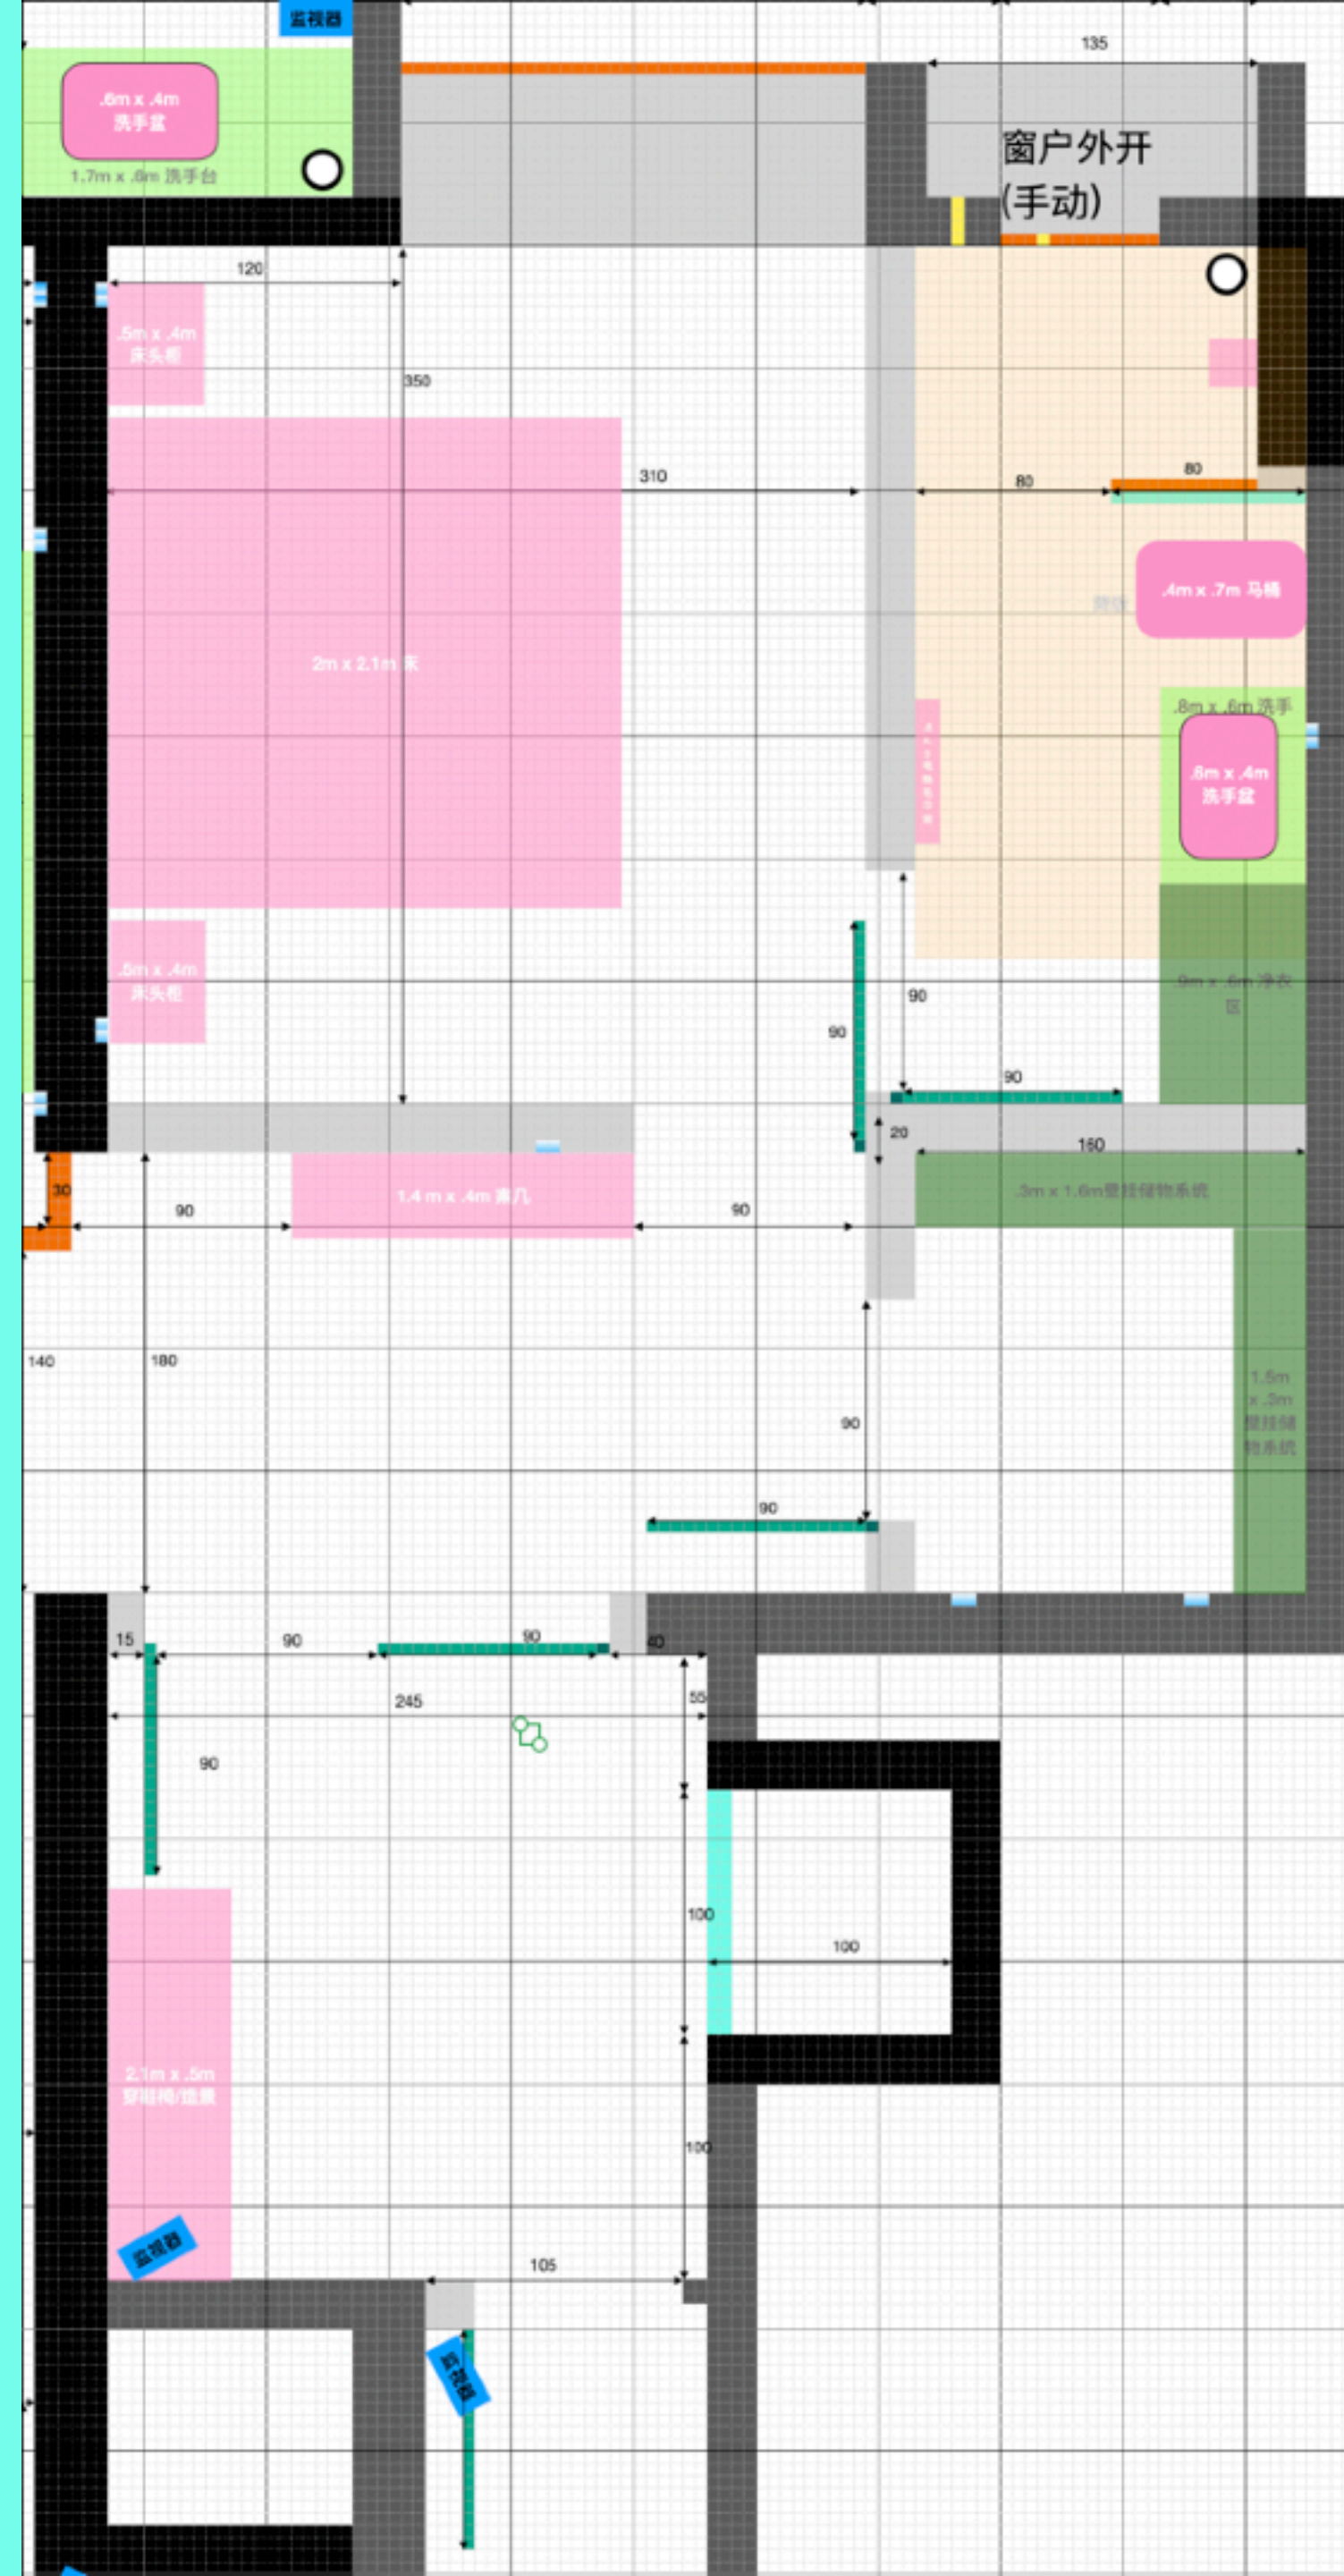

重点:

换回样板房布局, 另外次卧与次卫优先考虑华为智能家居,如:

使用箭牌淋浴器做无冷水


使用慕斯智能床(可与主卧的蓝盒子对换)

如果不使用中央空调, 优先考虑使用美的智能空调(注意他只有传统吊机)有半高的外机可以放在浴室窗户外而不会遮挡开窗

其他:

优先考虑在淋浴房使用中央集水器, 然后加上长条地漏作为淋浴房隔断. 空调排水可以排到中央集水器

次卫的顶天立地衣柜可以适当收窄, 多出来的空间加宽洗手台面.

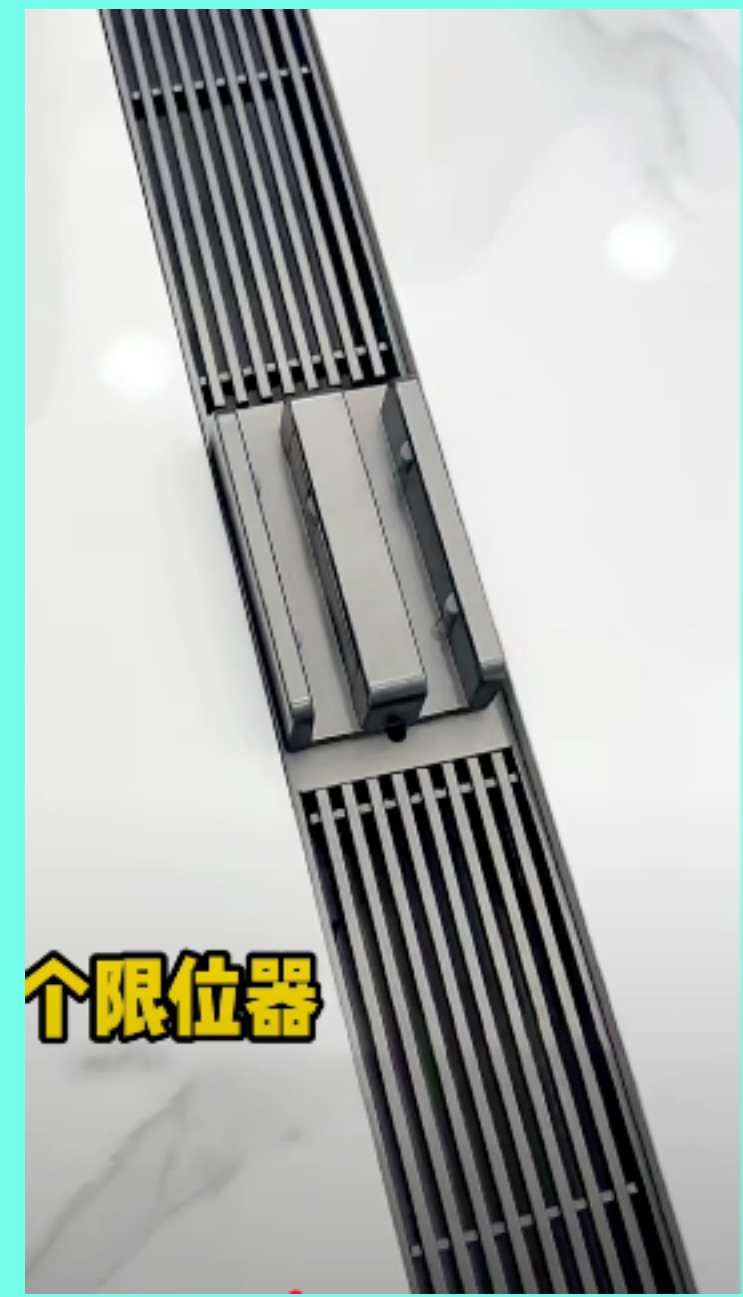

长条地漏可以跟淋浴门做在一起, 门是上吊滑门, 地面是与地漏整合的限位器

次卧- 4

阿姨日常使用為主，妹妹來訪時兼用。

- 1a: 高优先度
 - 需要有一张 1.8 米或 2 米的大床
 - 需要考虑之后换成护理床或是两张单人床.
 - 床柜上的插座在不同设定上不可以被挡住
 - 如有阅读灯, 同样需要考虑在不同设定上的位置
- 1b: 中高优先度（倾向安装）
 - 无

- 1c: 一般优先度（有疑问）
 - 无
- 1d: 低优先度（倾向不安装）
 - 无
- 1e: 黑名单
 - 电视