



大致分区

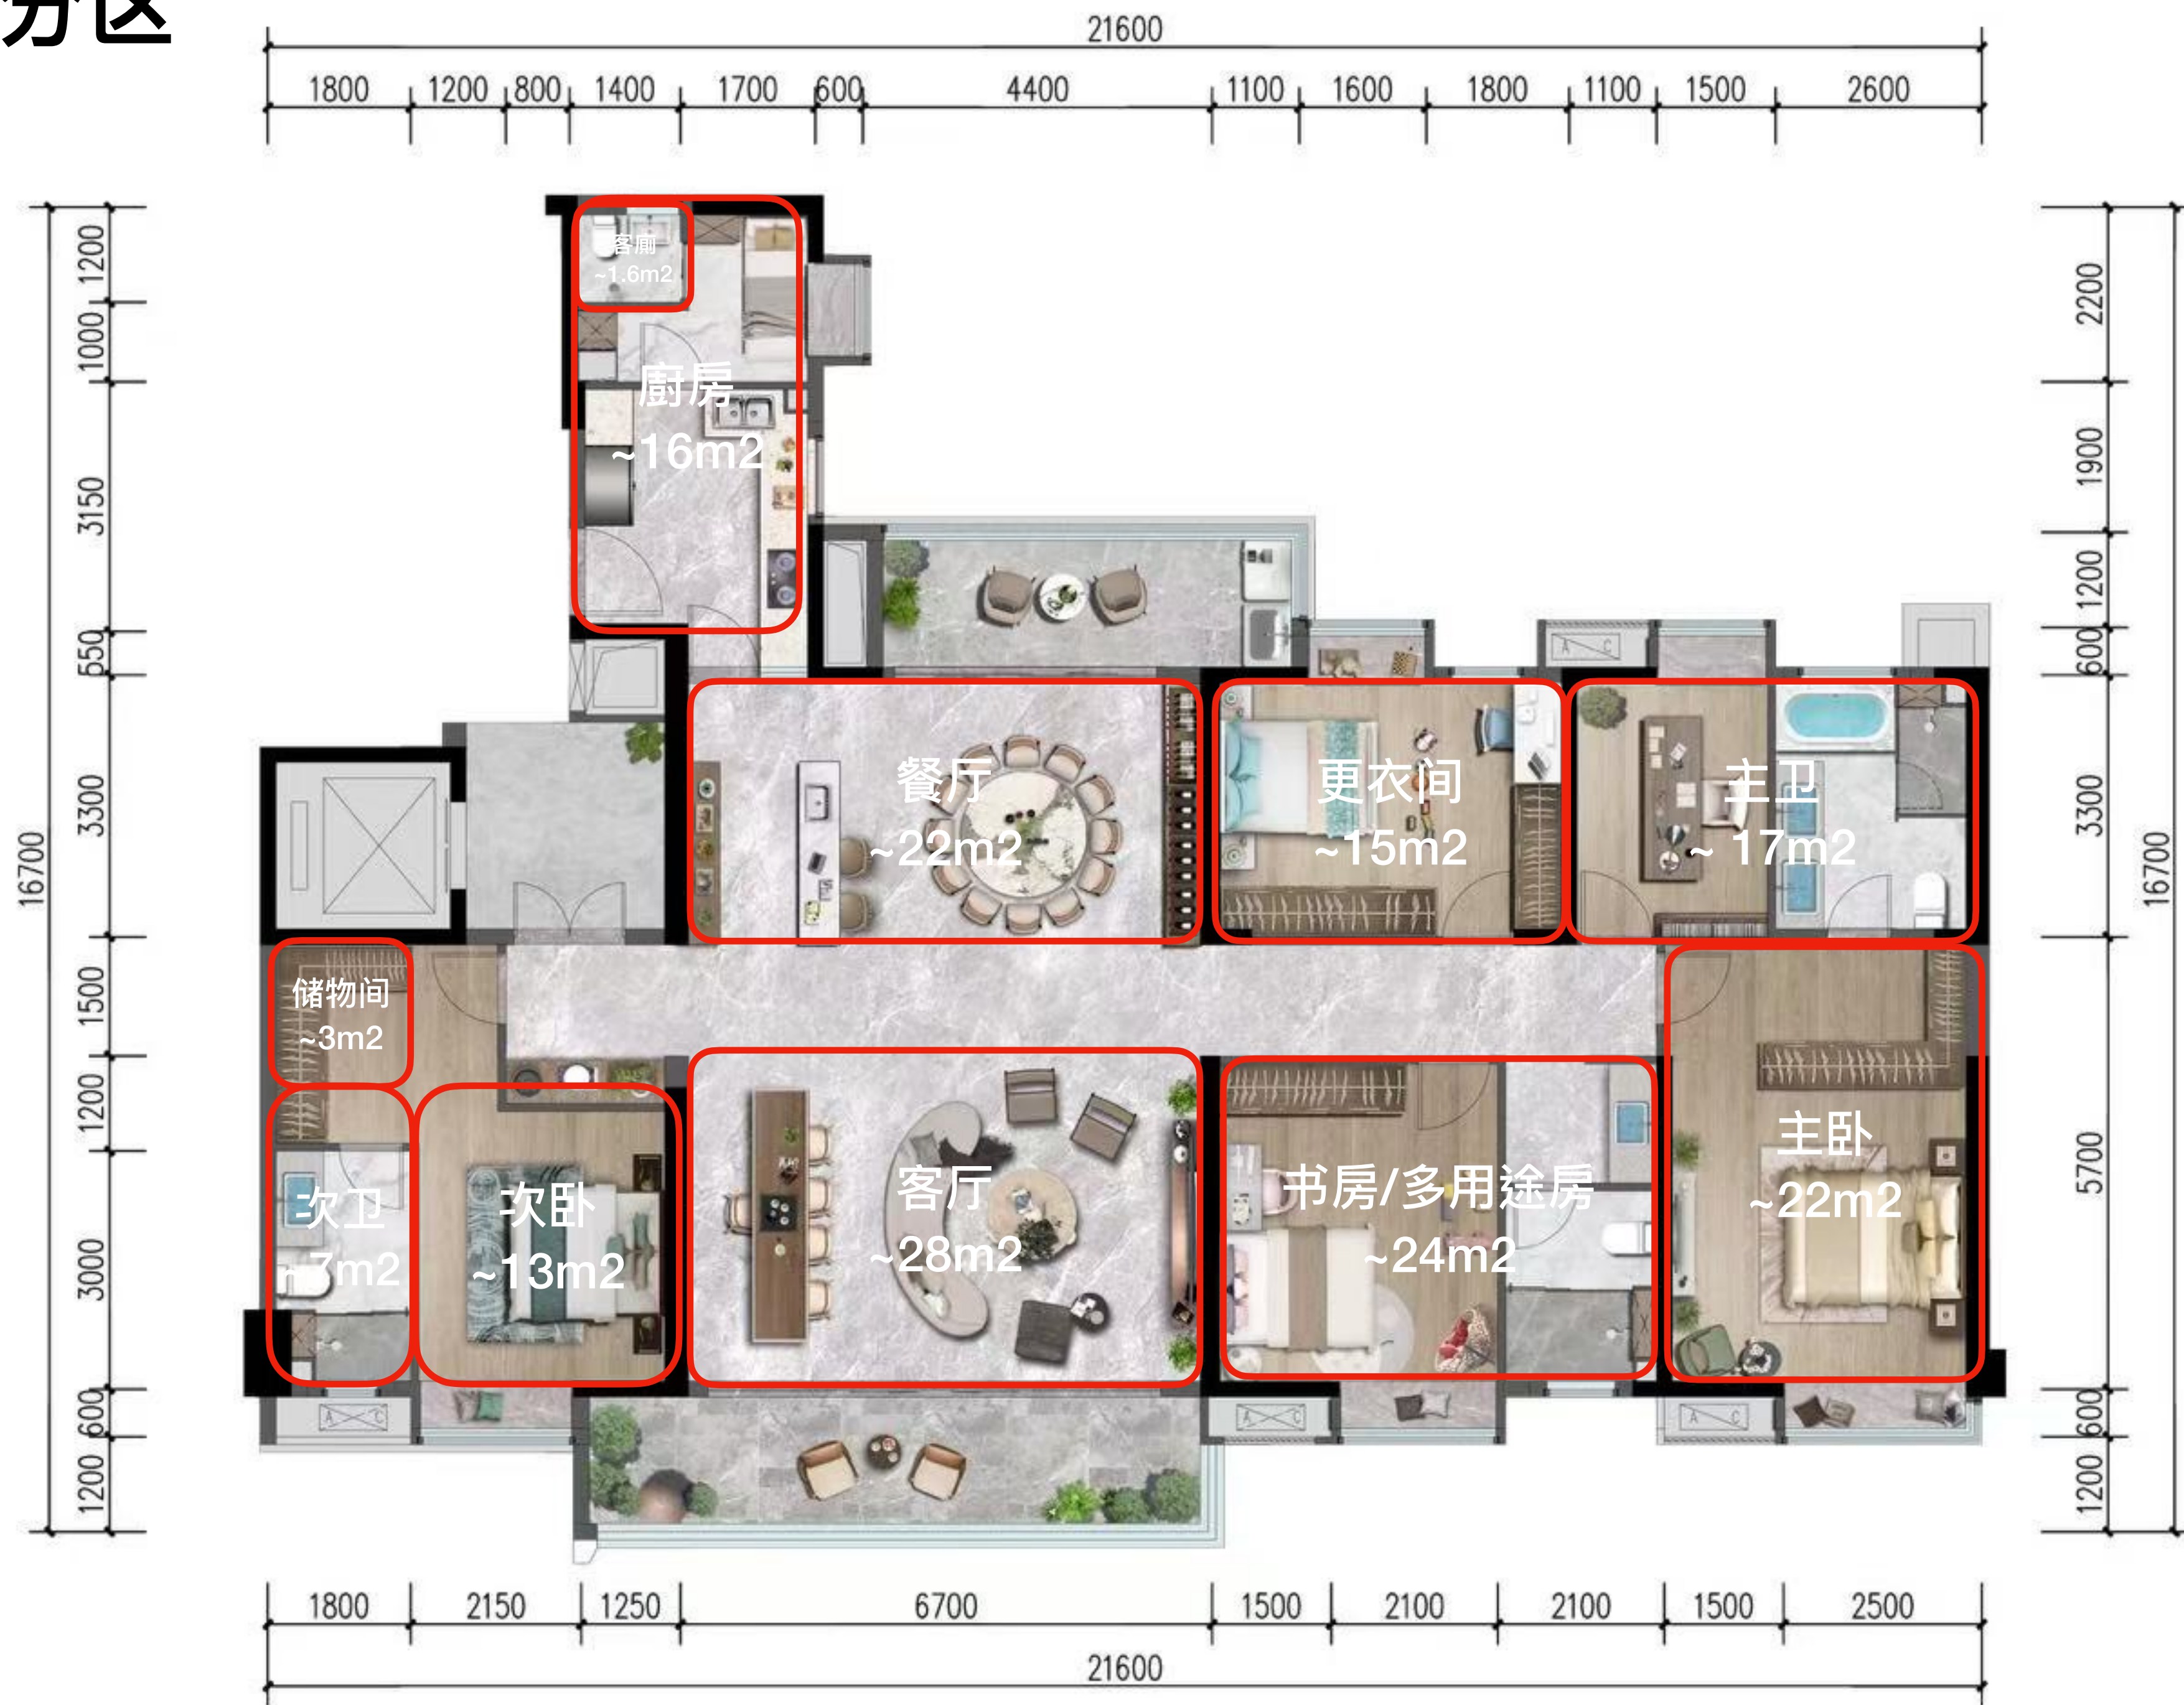


套内实际面积约 210 平米

主要变更:

- 入口处隔了一间储物间
- 中厨打通, 但留一个客厕/家政用水空间
- 将中间朝南卧室与相邻的浴室合并作为书房
- 将主卫与隔壁的书房合并作为巨型主卫

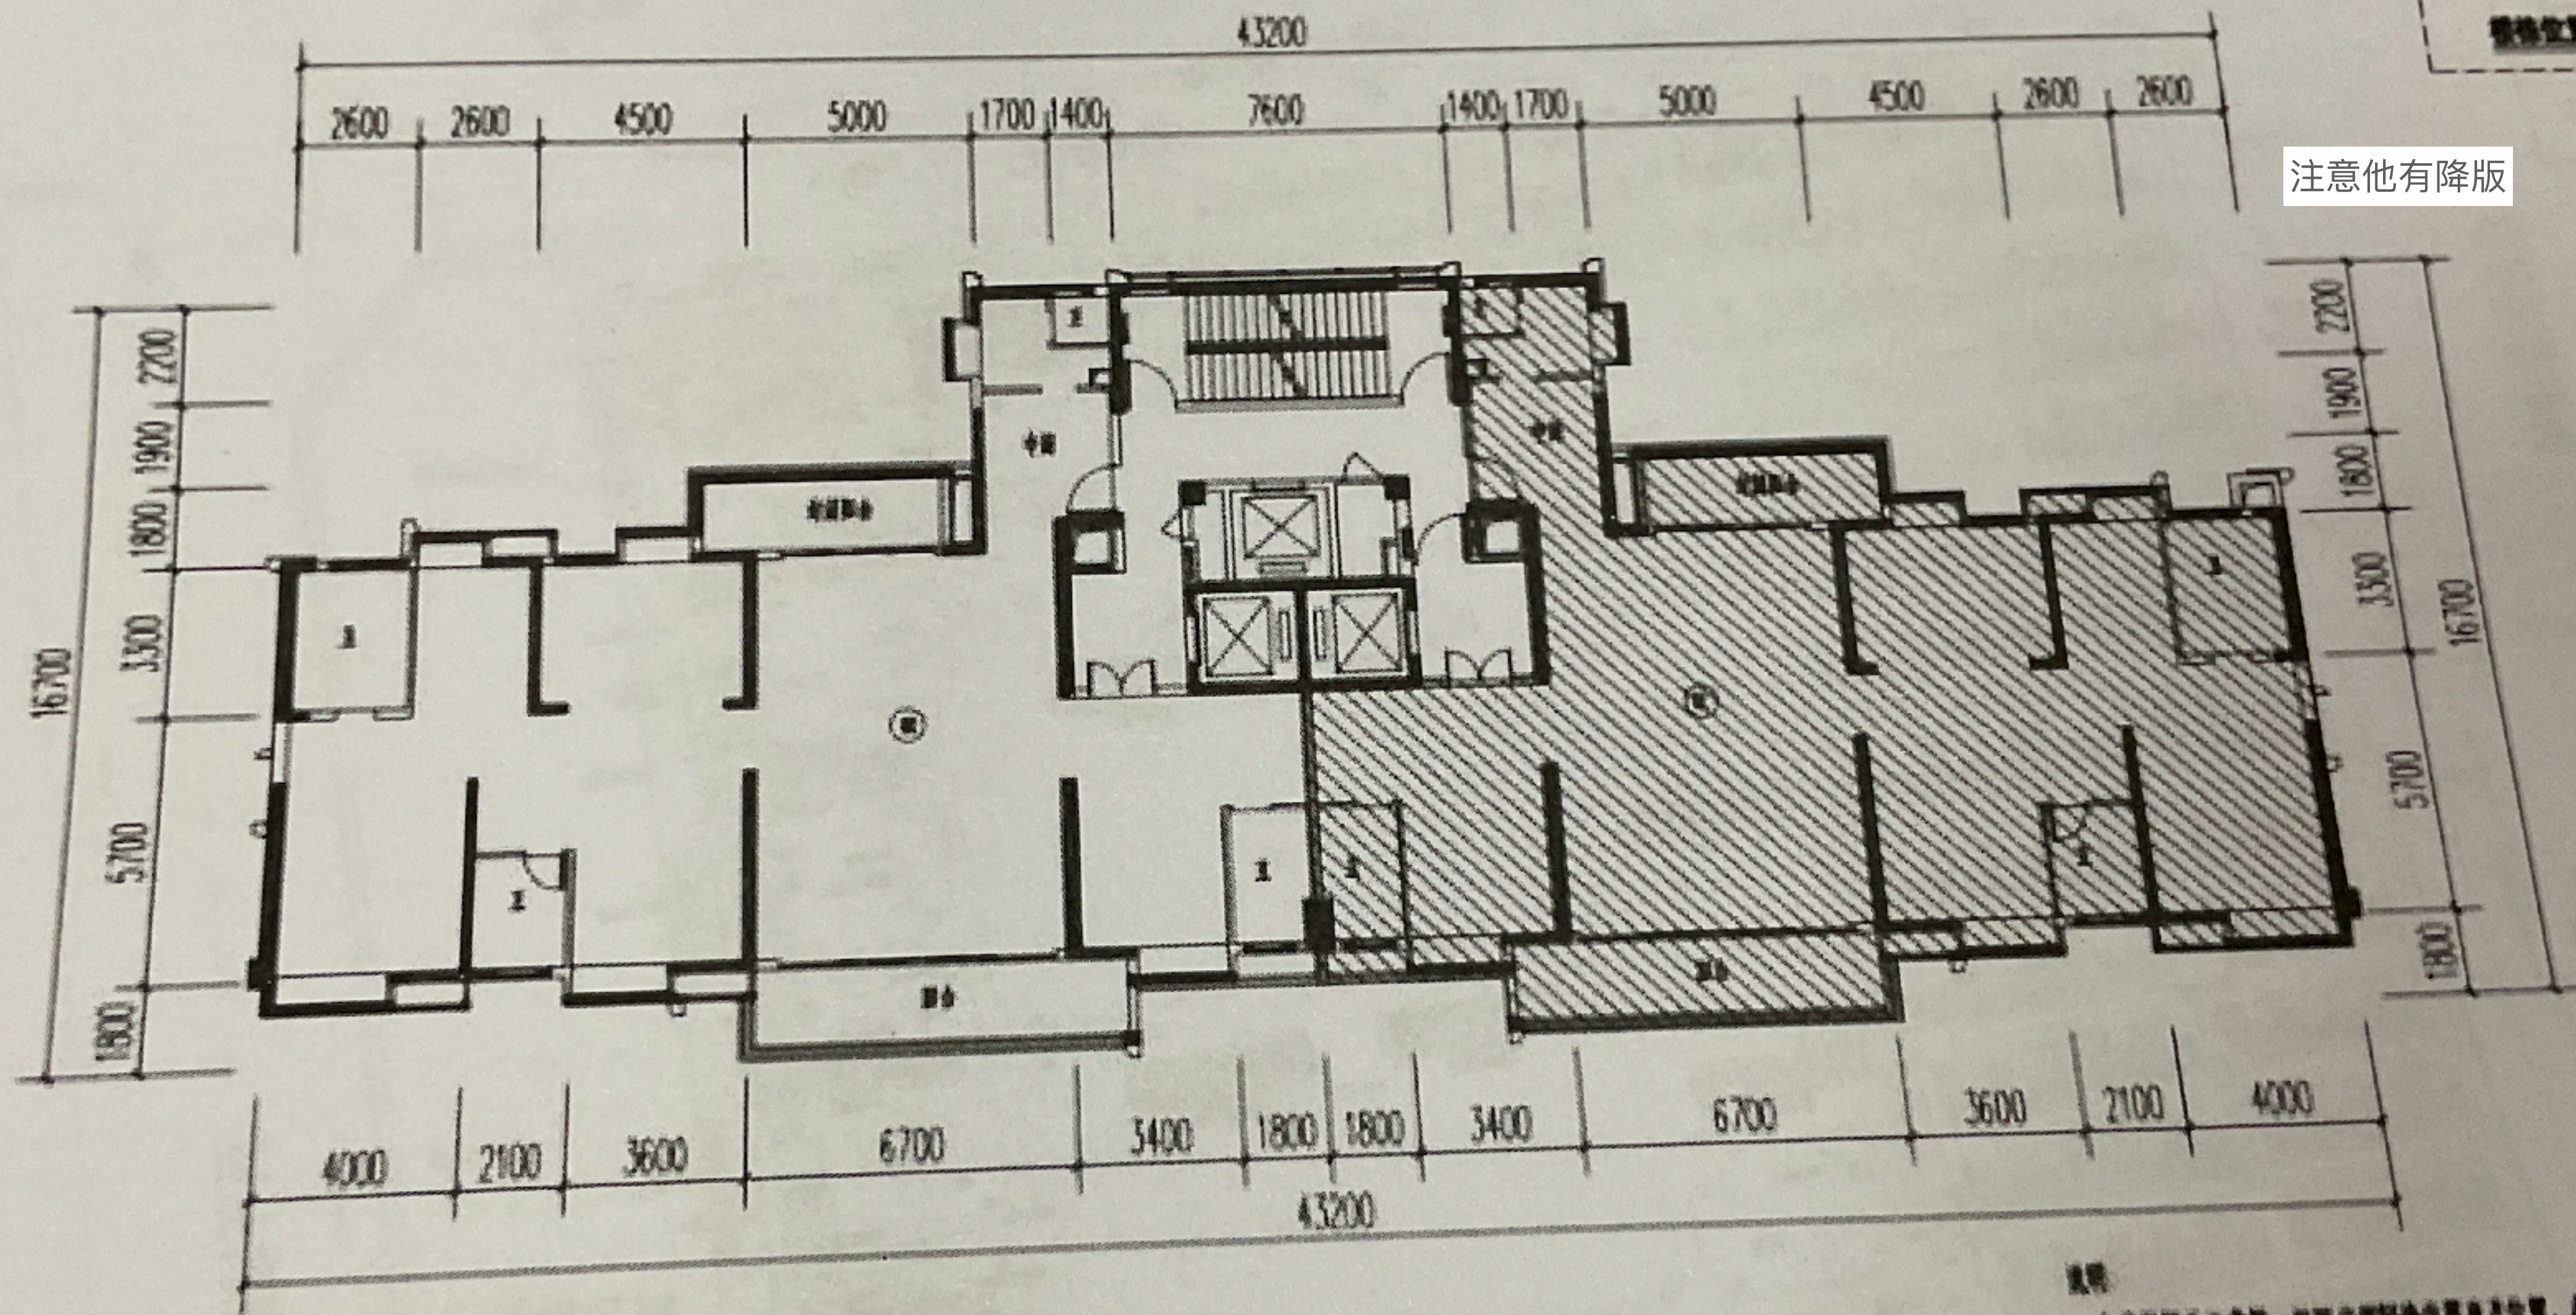

注意他有降版

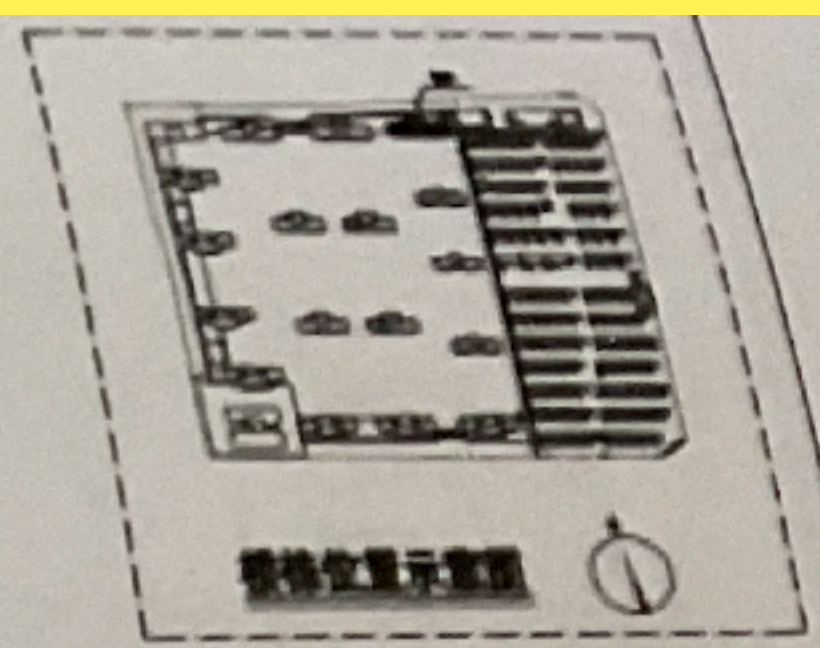

5#楼四~二十九层平面图

说明:
1. 本平面图为示意图, 详细户型结构及位置、名称、朝向、层数、使用面积、
及面积等数据, 均以实际为准, 仅供参考, 不作为法律依据。
2. 图中的尺寸均为建筑完成尺寸, 施工过程中可能因工艺、材料等因素
造成尺寸偏差, 最终以实际为准。