
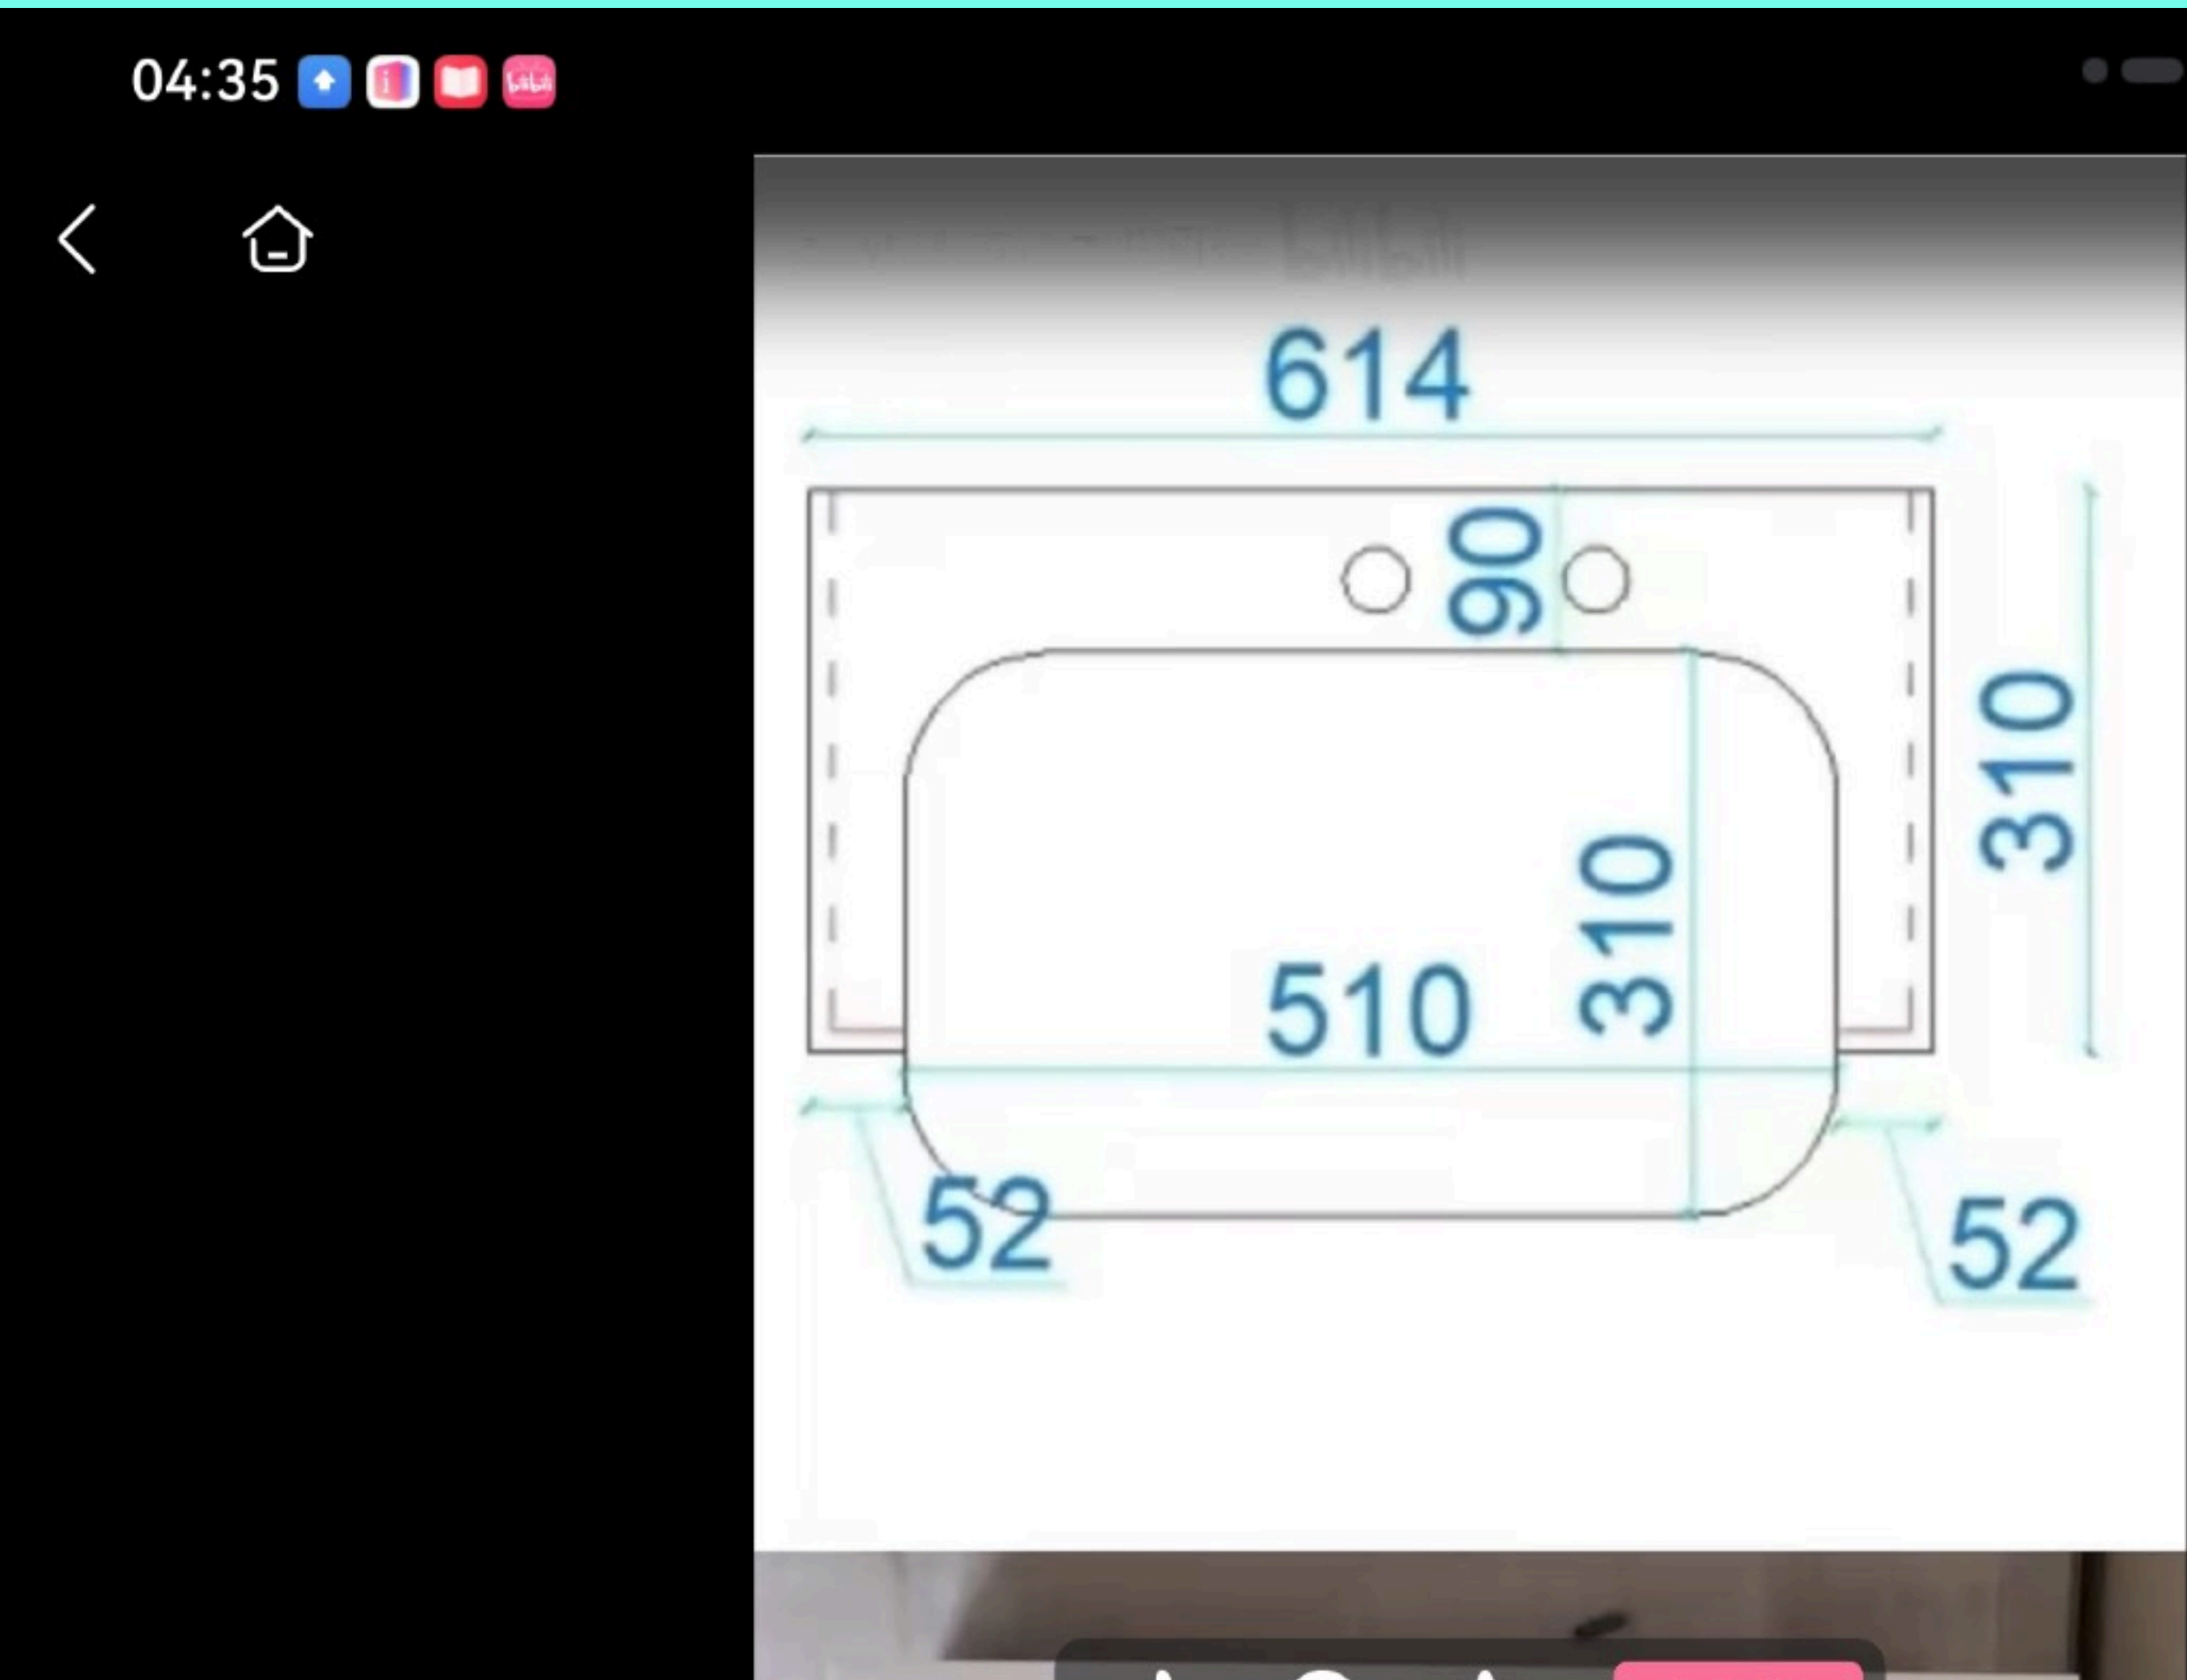


家政区 - 11c1

洗手台利用烟道的墙壁, 这样所需空间最小. 注意不要在烟道上钉镜柜. 只是单存的利用空间放洗手台

利用烟道的墙面作为洗手台墙. 注意我们不要钉钉子
避免破坏烟道. 另外使用这种大肚盆节省空间

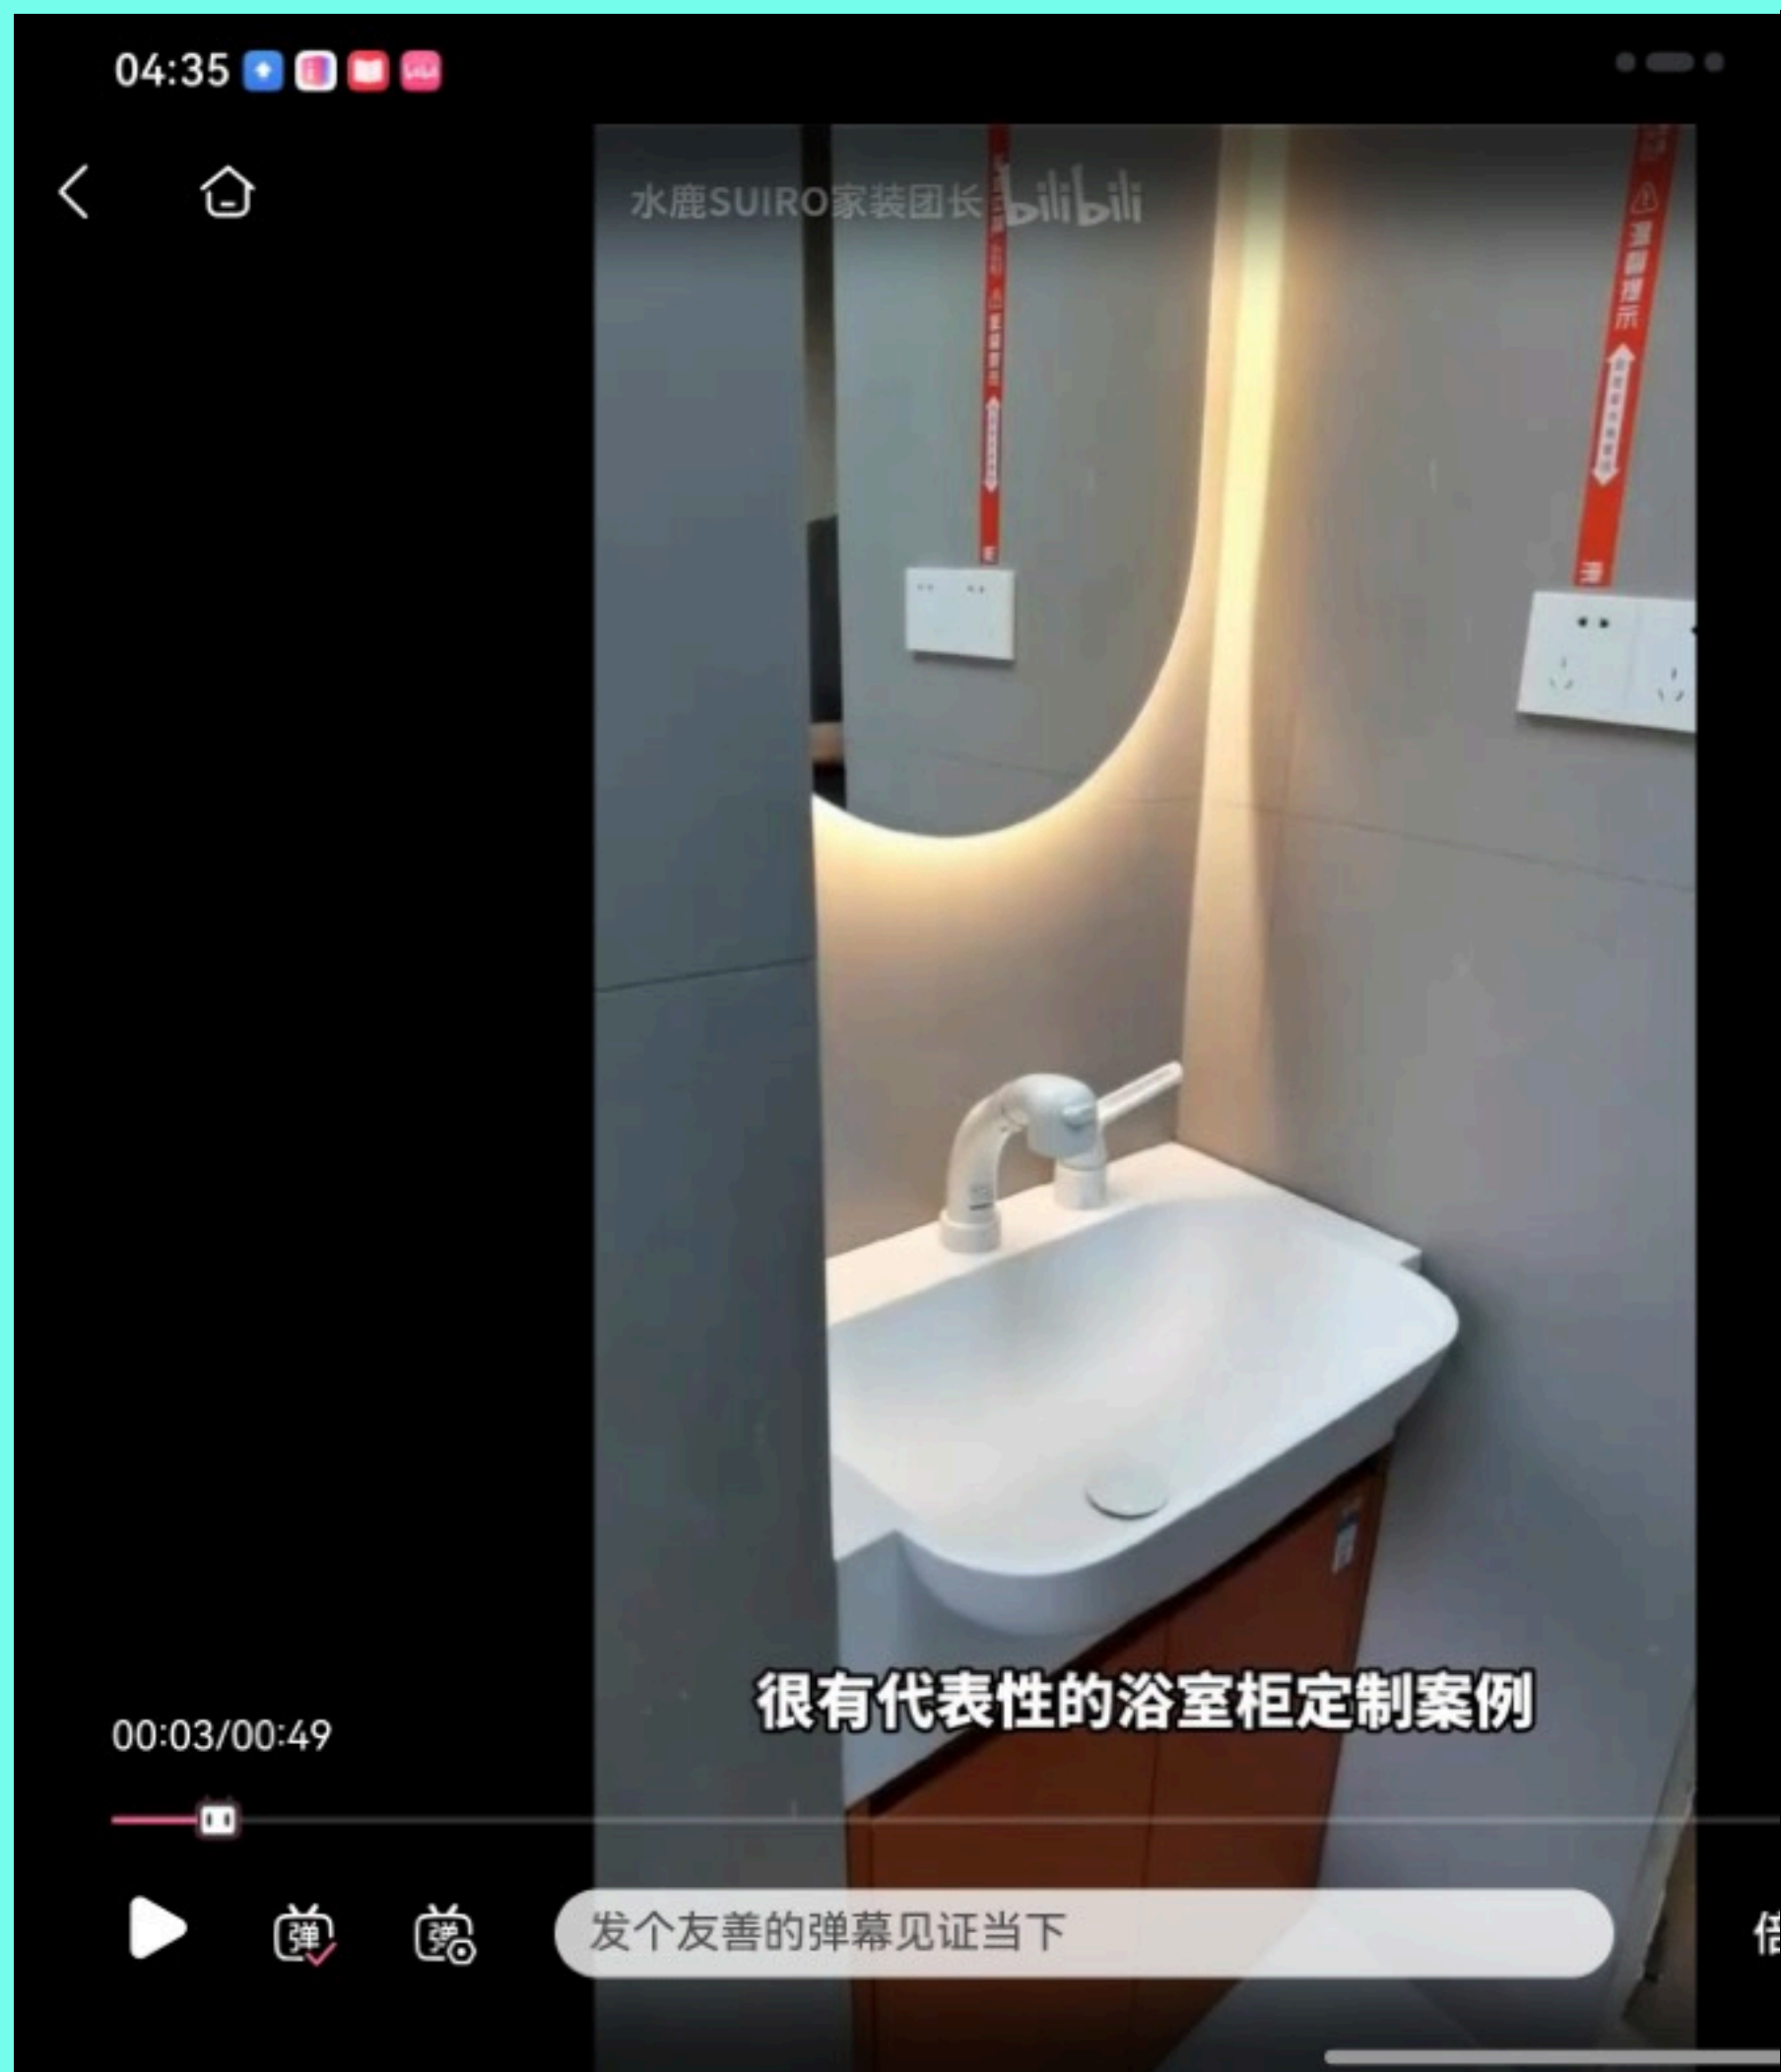

书房