


功能区平面方案

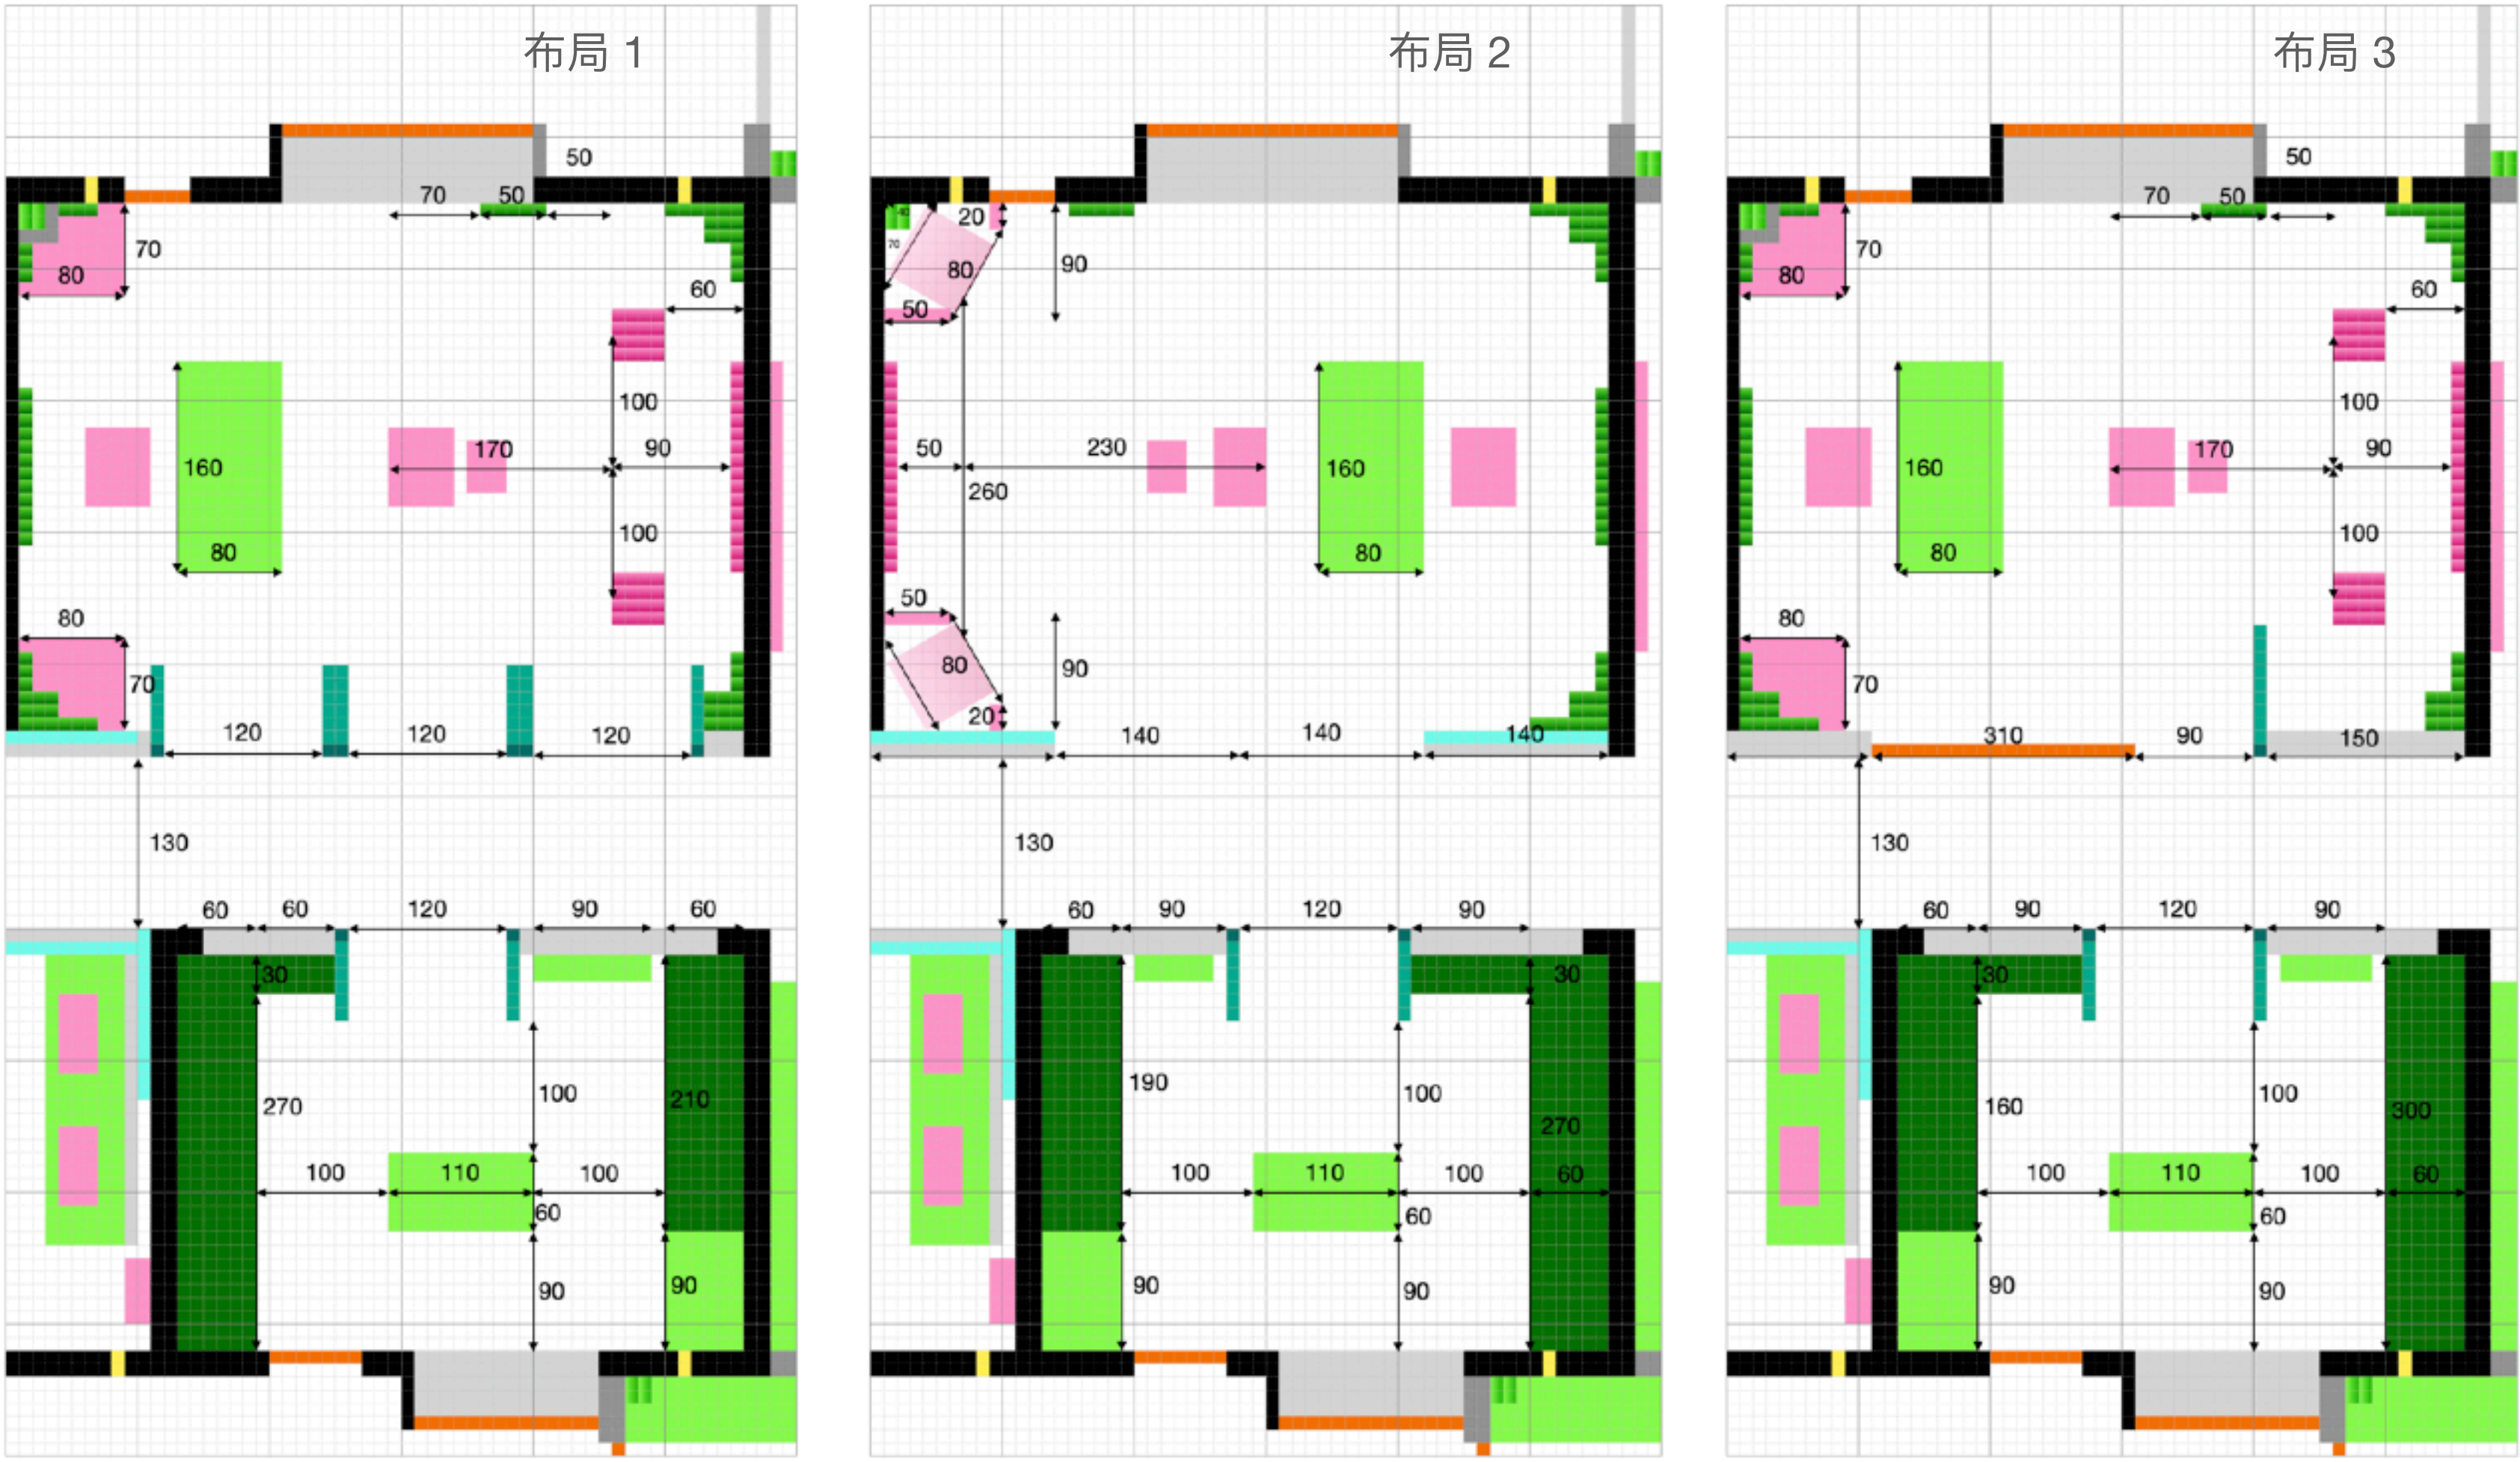

书房:

方案一：偏轴门

- 亮点：单扇 120 cm，三扇叠合可形成 360 cm 的“全景开口”，书房与更衣室门洞可精准对位，仪式感拉满。
- 隐忧：门扇间留缝，隔音是软肋。

方案二：双拉门

- 亮点：两扇 140 cm 拉门，总开口 280 cm，施工简单、造价友好。
- 隐忧：轨道间缝隙仍在，隔音依旧打折。

方案三：玻璃实墙，别墅“轻中式”

- 亮点：整面落地玻璃替代实墙，保留中式格栅或夹绢纹样，空间通透却仍有东方意韵；中空玻璃一关，隔音不再是痛点。
- 隐忧：玻璃需勤擦拭才能常保清透；格栅比例、色温、金属收边需与全屋木作、硬装细节反复校色，否则易显突兀。

更衣室

梳妆台与全身镜的位置，可以放在同一边，或是相反方向。另外根据书房门的选择，更衣室的门可能需要偏一边，或是居中。全身镜的大小与相对短进深的饰品装饰柜(如包包) 可以放在长边或是短边。另外衣柜可以选择壁挂系统，或是立柱系统。衣柜的照明也可以是由上往下，或是直接用背光系统。(如衣柜背板使用宣纸灯箱)


音箱可以用音响架放在客厅方向，或是利用柜子然后放在柜子上(优先考虑)




特殊区域布局 (目前选择)

更衣室不使用推拉门是因为推拉最大的好处是开阔的开门。不过这样在客厅就能看到更衣室的衣服。因为我们不用柜门，所以这是需要避免的。

替代方案是使用与书房一样的偏轴门. 这样除了对称, 双开门也比普通单开大的多, 另外我目前只设一对双开门, 他其实有空间做第二扇. (但会损失吊衣空间)

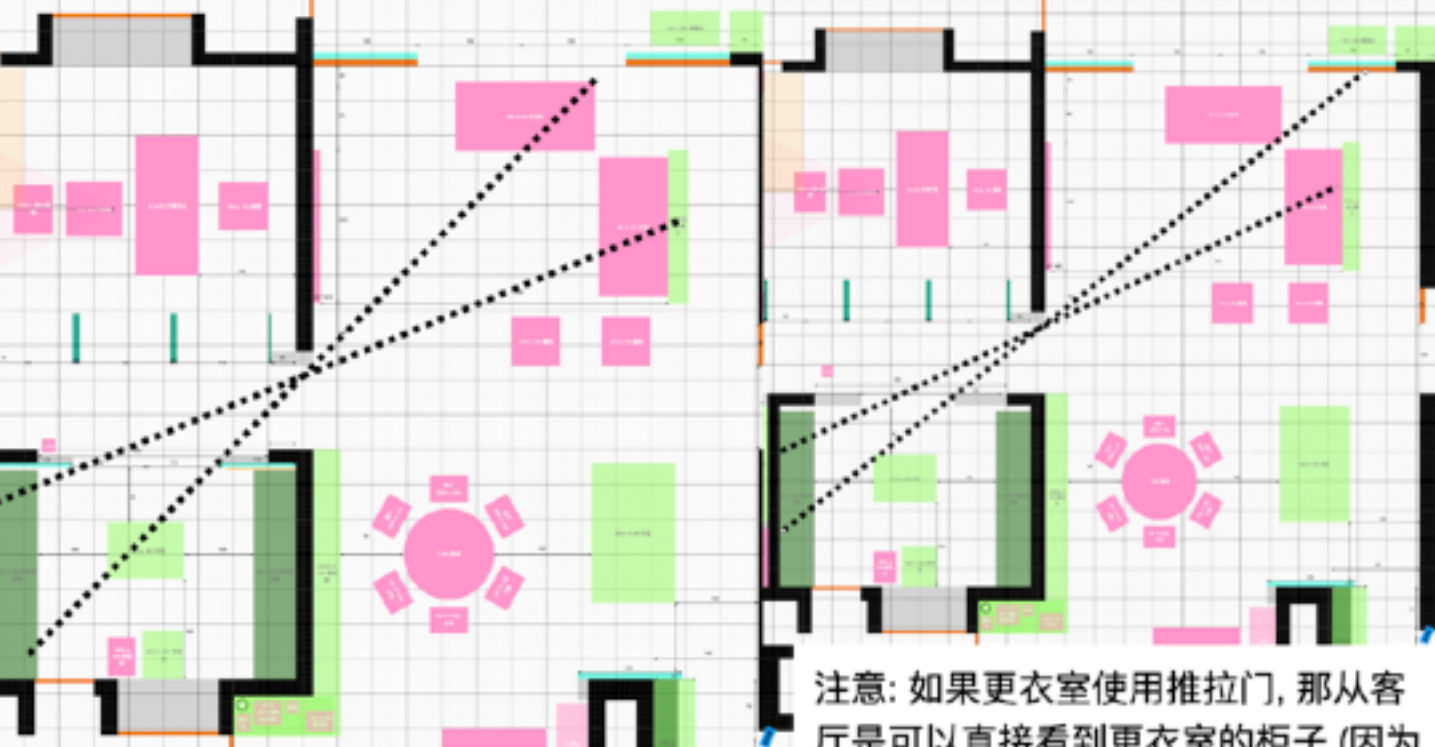

左右两图各自展示不同开间宽度的视线

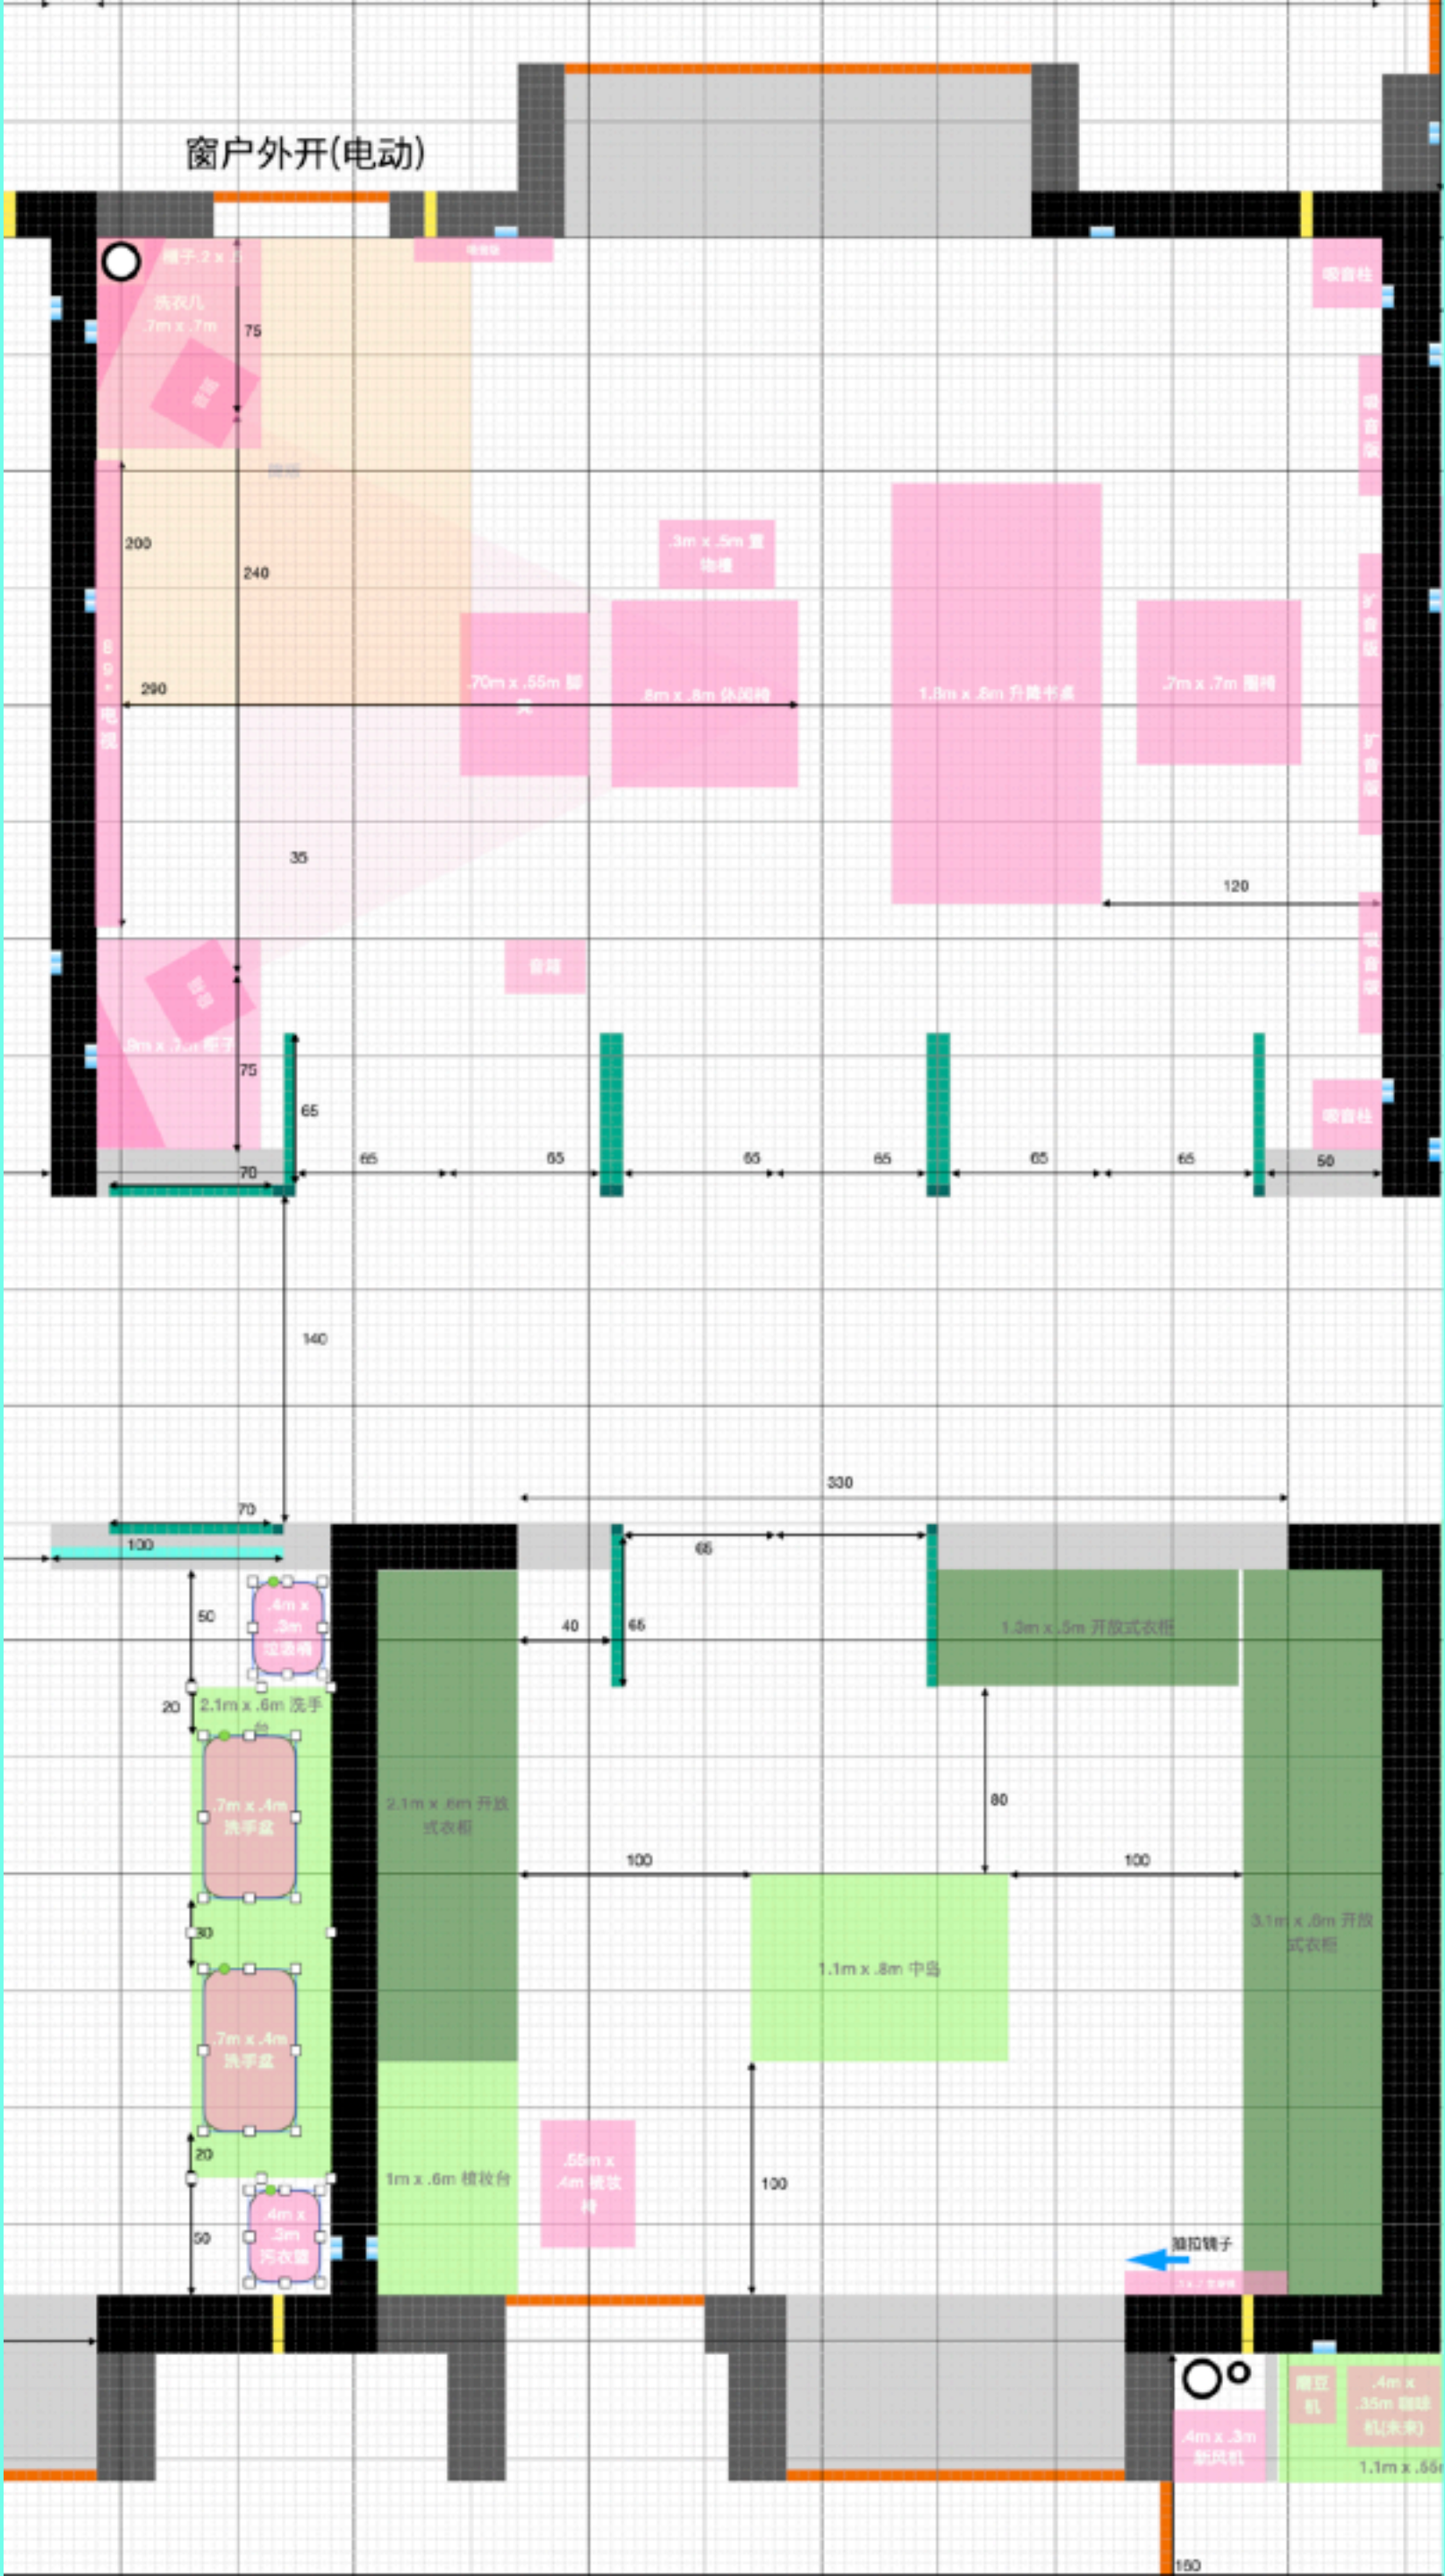

重点:

书房主要为单人使用

需要舒适的休闲椅

需要升降书桌(不需要对应的人体工学椅, 只要漂亮就行)

洗烘一体机放在柜子里, 两边柜子内部都是空的, 事后再找置物架. 另外柜子需要门. 门体傾向透氣設計)

使用洗烘一体的原因是烘的功能主要服务于梅雨季, 其他时间以晾晒为主.

注意柜子上还会在角落安装三角形吸音柱来盖住下水管(根据计算,一片60cm 宽的吸音板应该够遮住下水管)

更衣室

需要中岛,走道应该尽可能宽敞

需要梳妆台, 注意尽可能不要台面下的抽屉, 腿会比较好放, 且扶手不会与抽屉发生冲突. 梳妆台收纳可以坐在旁边的抽屉

中岛两侧应该做成开放格, 抽屉做在飘窗方向, 朝走道应该以美观为主

大型物件, 如冬季棉被, 优先考虑放在中岛. 四周全部都是开放式衣柜. 吊衣服为主, 可以有少量抽屉. 注意下面最好为开放式, 允许扫地机进入