
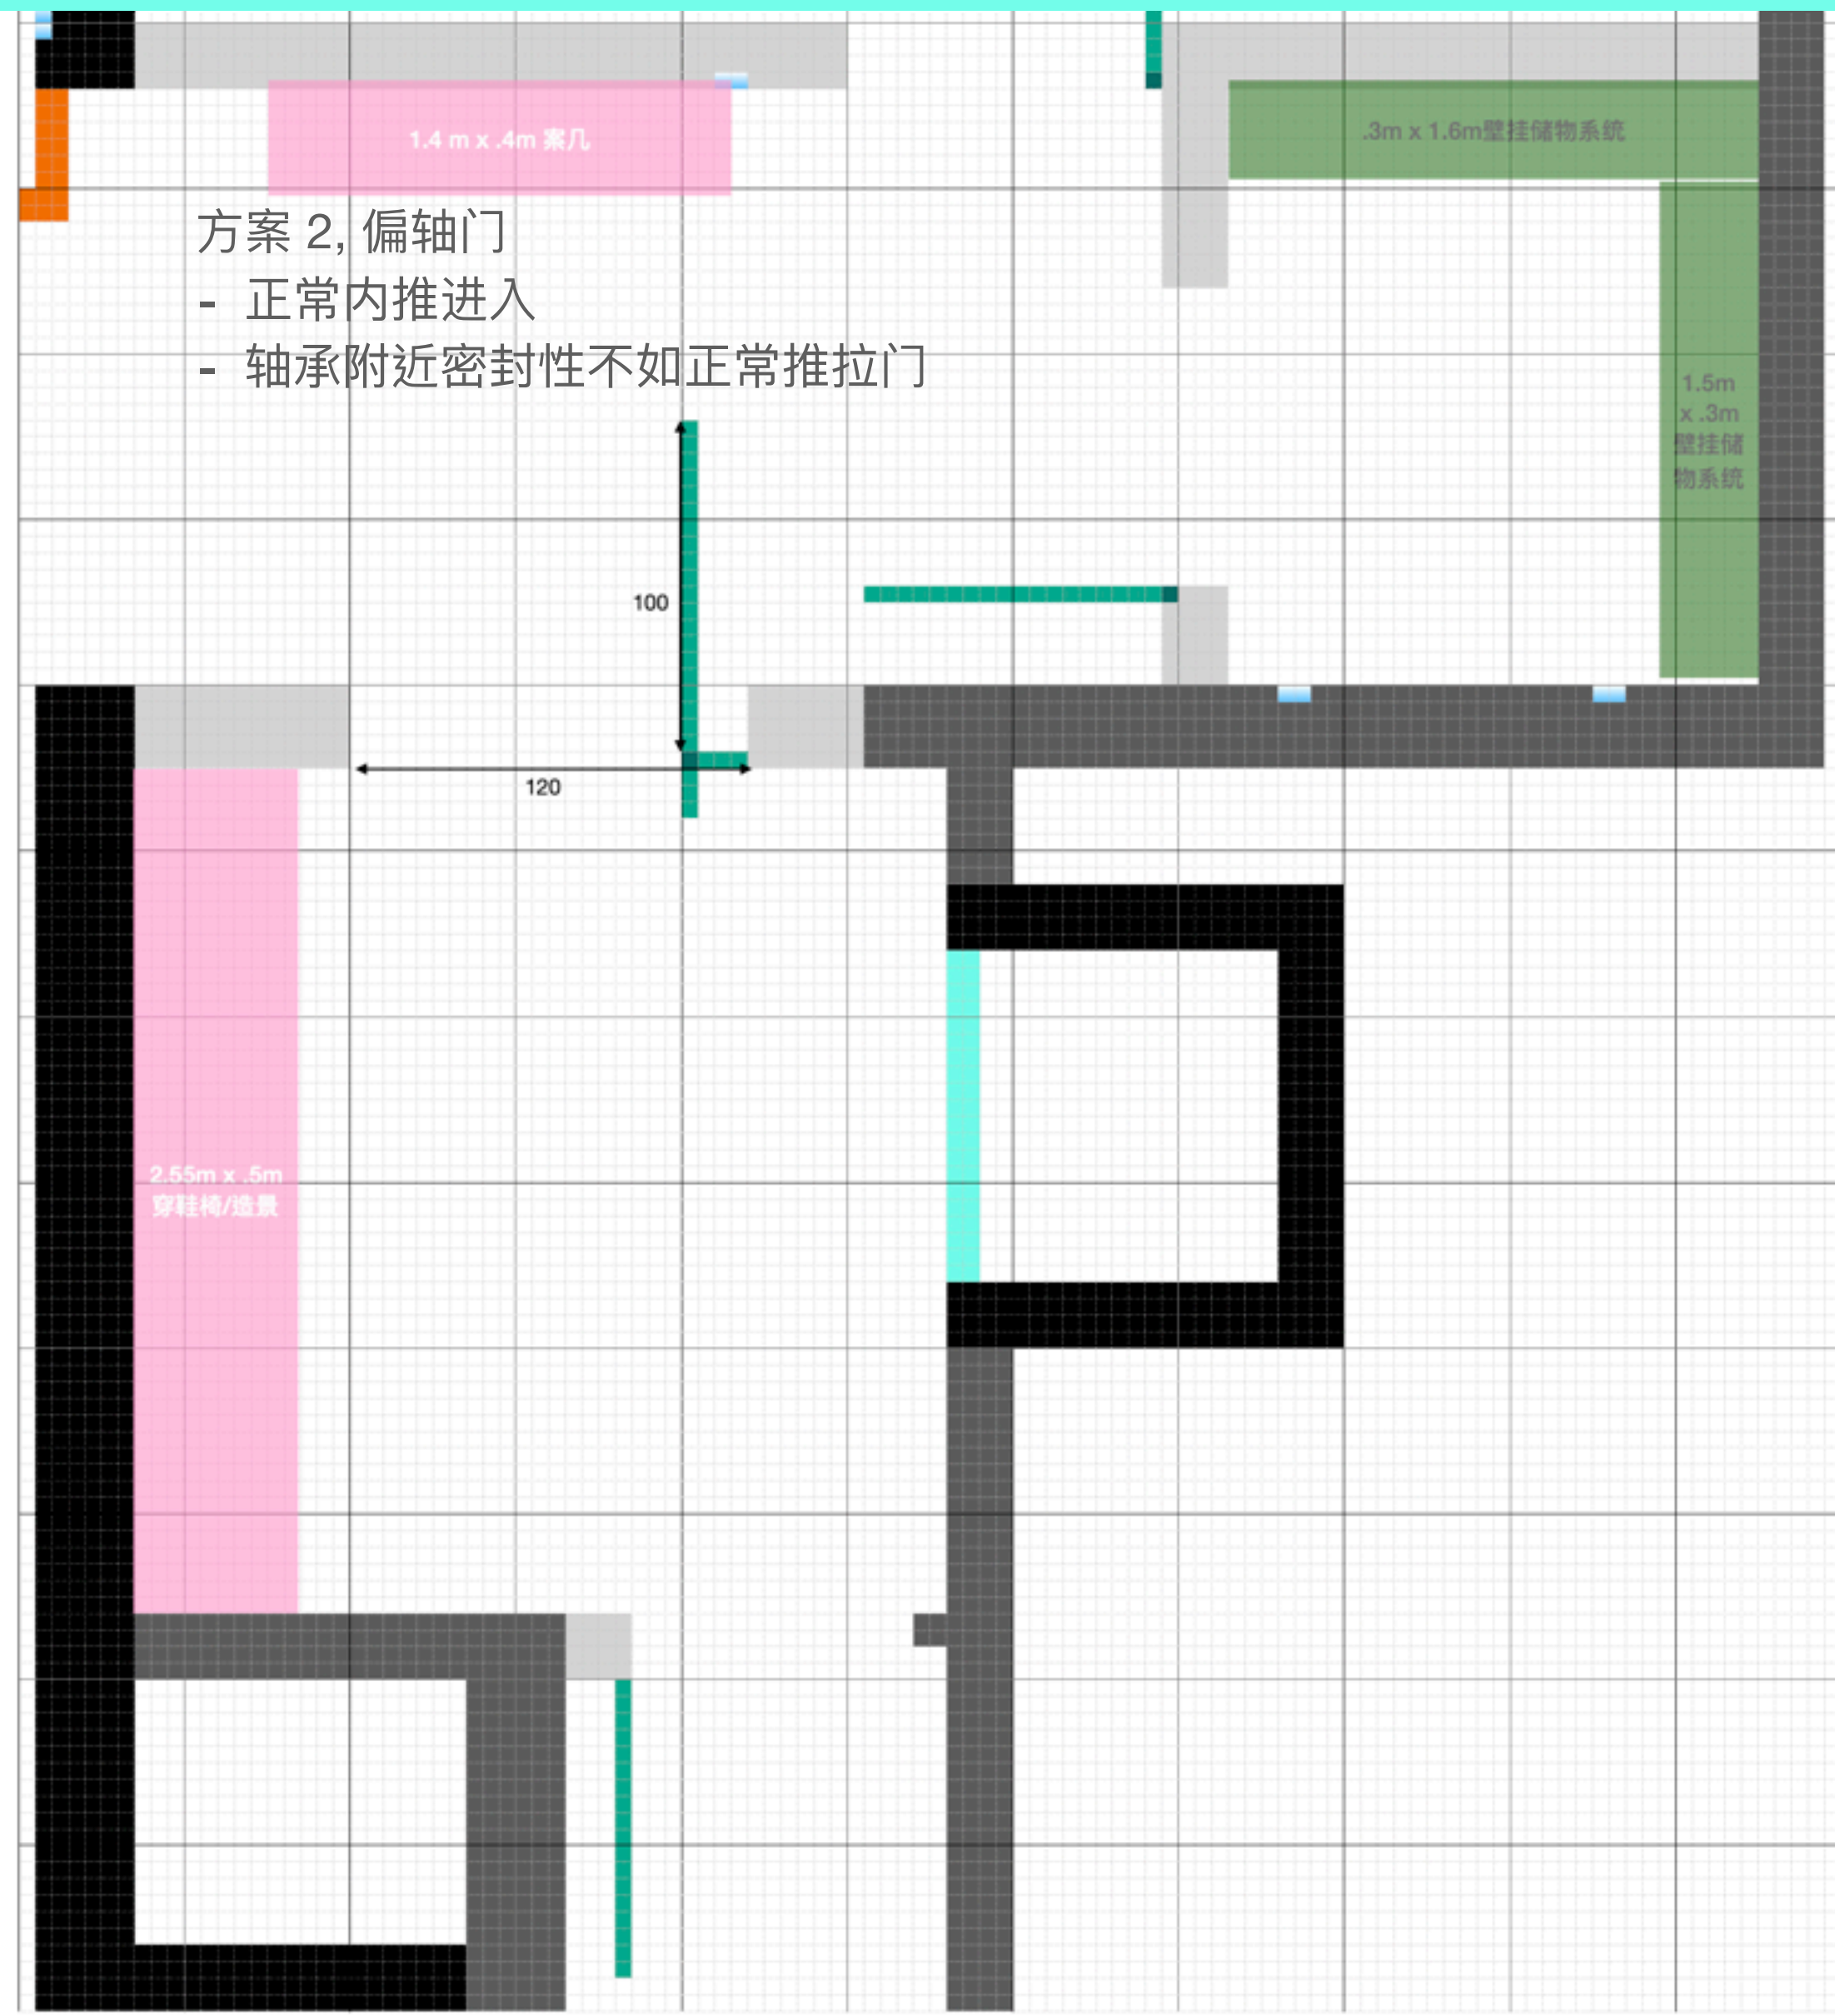


入户空间方案

因为开发商虽然给双开门, 但每扇只有 60cm. 一般来说门洞宽 120cm 通常用作子母门. 因为不喜欢子母门. 两个改造方案分别是:

1. 扩大门洞到 180cm 左右. 这样还是能保持一片正常 90cm 的门宽. 但靠近电梯那扇门是长关的 <- 目前倾向此方案
2. 使用偏轴门, 好处是大门本身一个完整的面板, 而不是如子母门般分成两截. 实际进入门宽度有可能大于 90cm

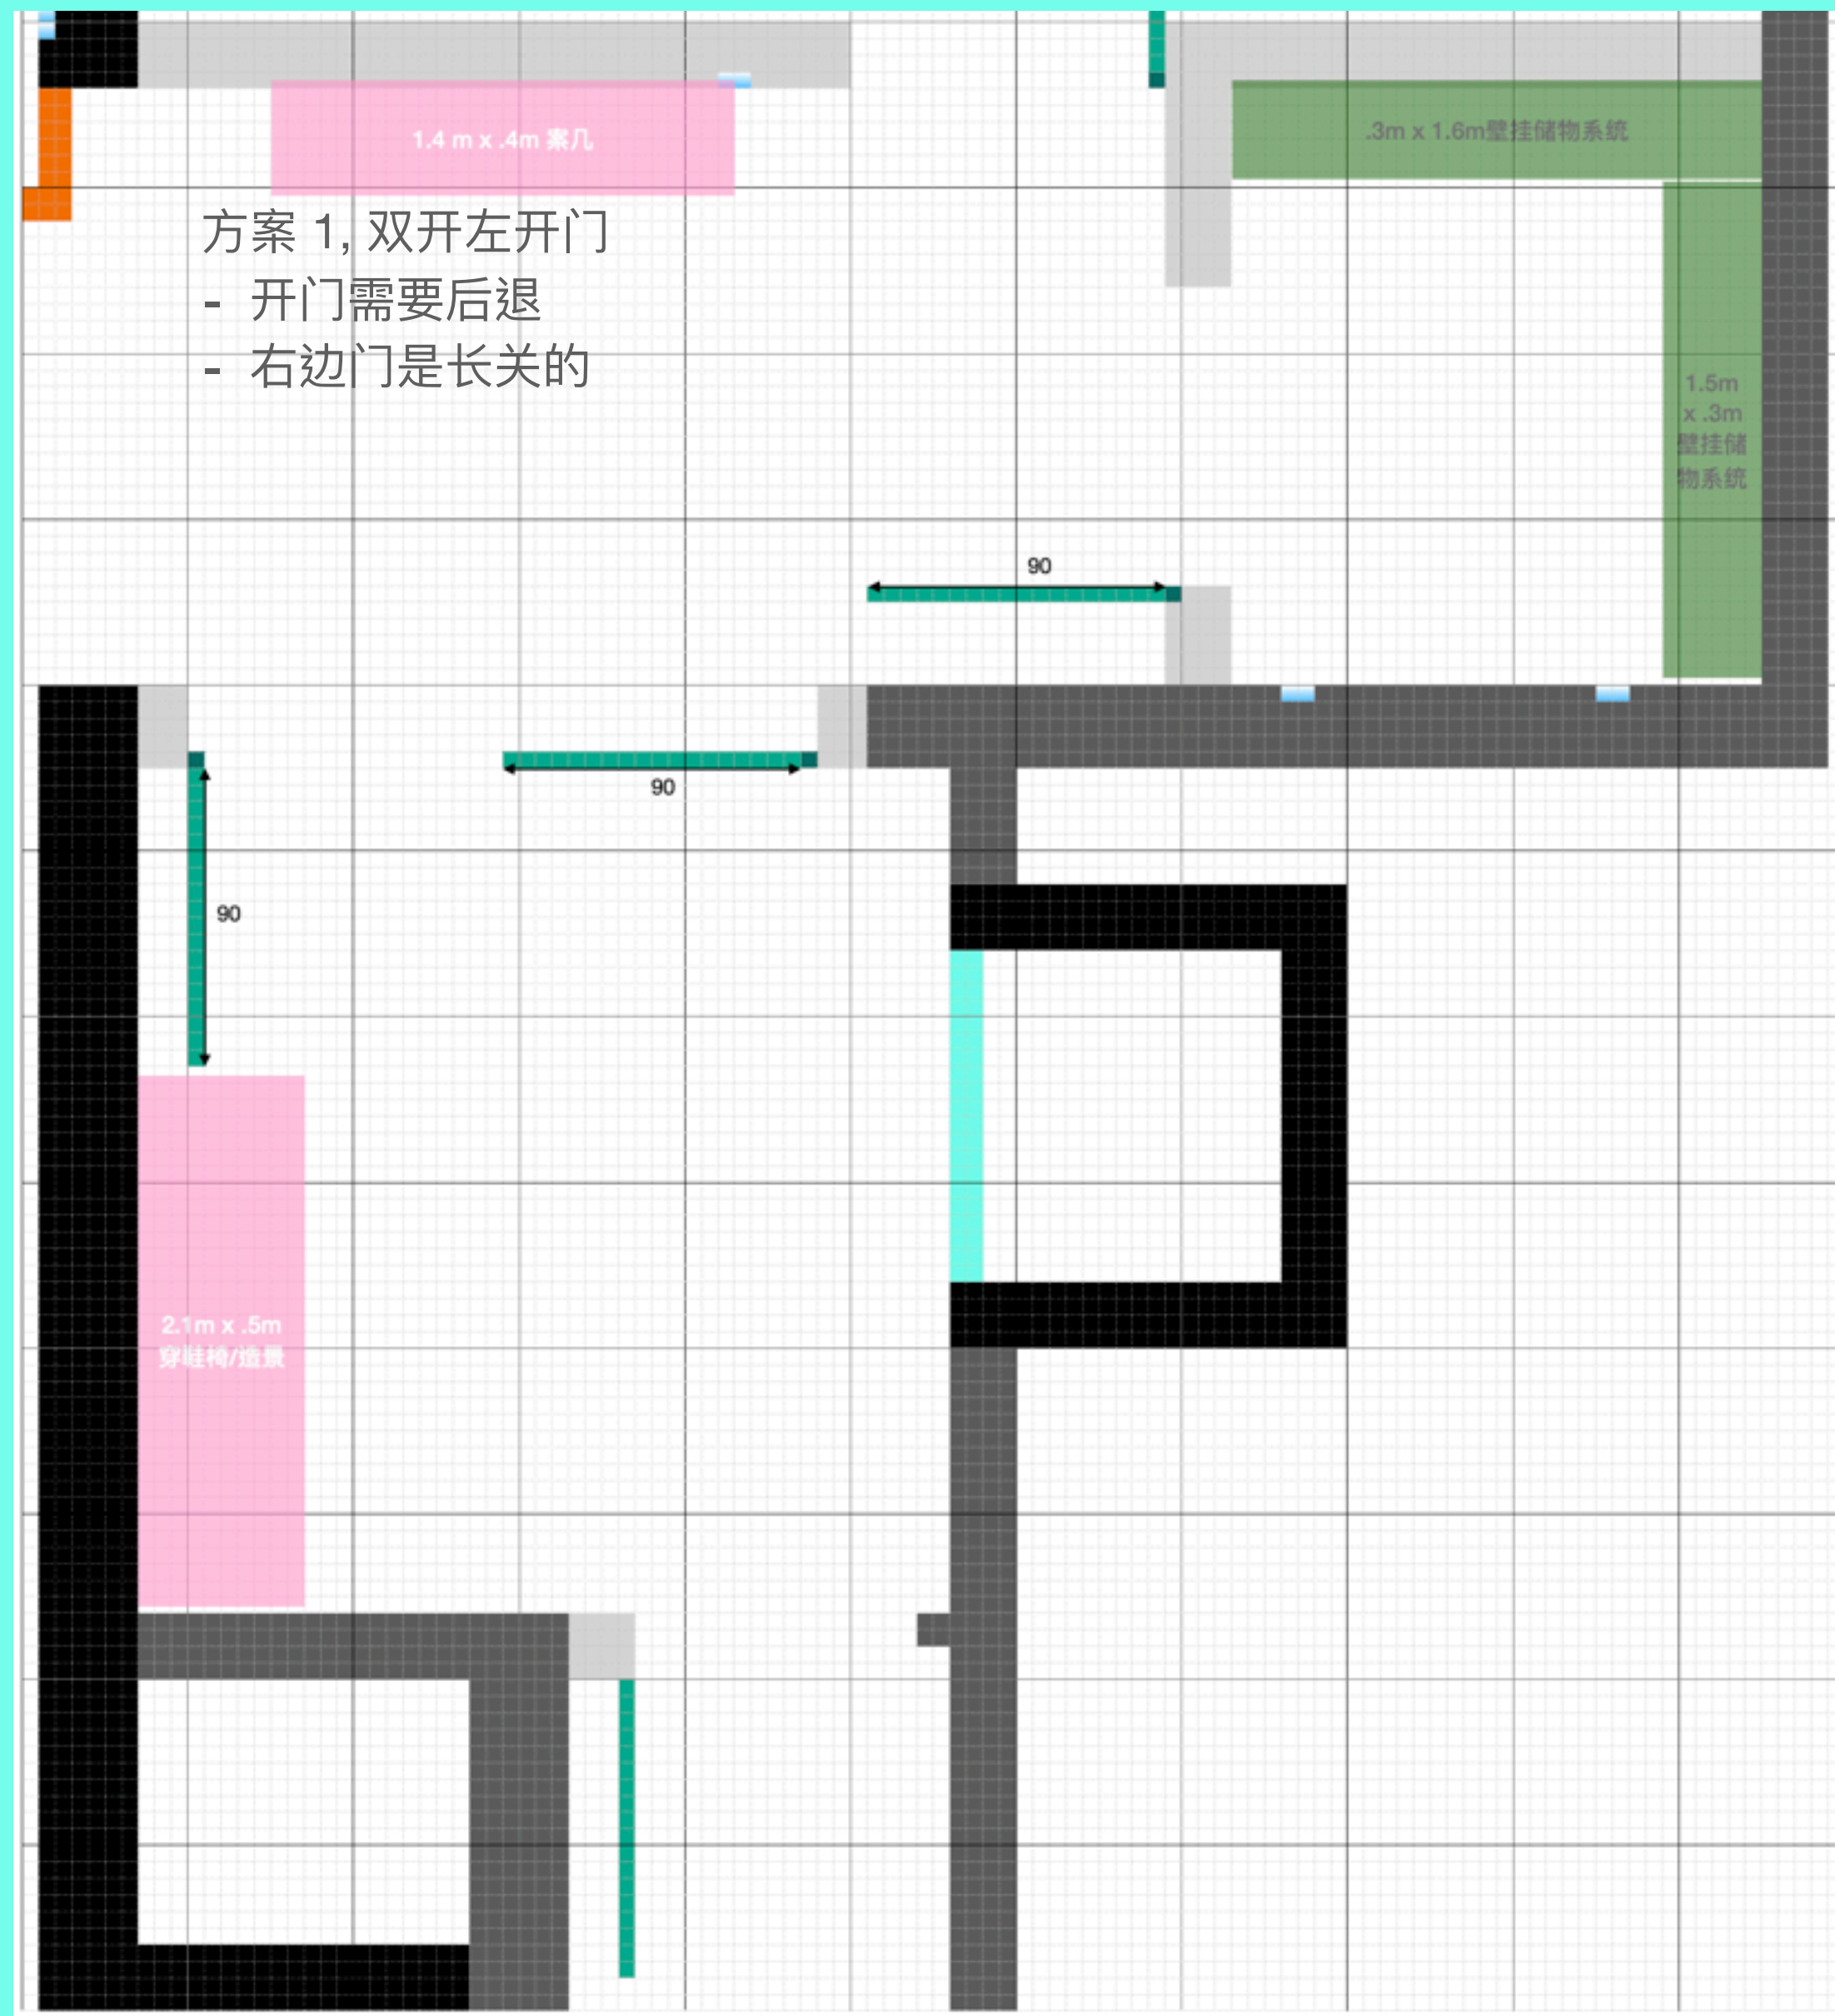

电梯厅 - 1

独立封闭电梯厅, 主要用于换穿室外鞋. 必须有换鞋凳. 只需考虑最多放置三双外出女鞋与一双男鞋. 需要考虑鞋子通风与散味. 必须要有监控. 其他功能如放置潮湿雨伞, 收纳外出折叠小推车等. 都只是加分项. 另外因为开发商给的是扇宽 60cm 的双开门, 不利后续使用. 考虑扩大门洞换更大的双开门, 或是单扇入户偏轴门(铝木门, 因为比铸铝门薄, 可以安装华为锁芯)

- 1a: 高优先度
 - 需要有穿鞋凳
 - 需要有外出鞋柜 (矮柜即可)
 - 不超过三双女用鞋
 - 留一双男生球鞋的位置
 - 需考虑鞋子通风与杀菌问题
 - 有放外出可能会用的东西如湿纸巾, 鞋套等的地方
 - 须保证电梯厅 24 小时都是光亮的. (小灯也行) 另加感应灯作为使用时的加强照明
- 1b: 中高优先度 (倾向安装)
 - 因为单扇门片只有 60cm, 考虑更换大门.
 - 双开门方案: 扩大门洞, 换更宽的门. 不过门锁可能用不了华为的智能门锁. 因为双开铸铝门通常较厚 (>10cm) 需要寻找能用华为门锁的双开入户门
 - 单扇偏轴入户门: 单扇 120cm 的偏轴入户木铝门是个替代方案. 门厚可以安装智能门锁. 缺点是隔音不如正常入户门. 另外一堵墙作为入户好像有点奇怪
 - 因为换大门会动到天花板, 考虑使用更加优化的照明(如灯带或灯箱) 除了天花造型, 不排斥在墙面做灯箱为辅助照明
- 1c: 一般优先度 (有疑问)
 - 放置潮湿雨伞的地方 (没有的话可以放在厨房的家政间)
 - 需有监控, 除了门锁自带的电子猫眼, 还需要一个吊在天花板的摄像头.
 - 衣柜, 需要询问物业, 如果电梯只能到自己楼层, 那可以考虑在这吊衣物, 否则不会在电梯间放置衣物
- 1d: 低优先度 (倾向不安装)
 - 空间允许下规划放(折叠)小推车的位置, 方便由楼下取重物上楼, 沒有的話可以放在儲物間或是通往后门的地方. 不过实际使用时机存疑.
- 1e: 黑名单
 - 无