


专用特殊空间

功能区平面方案

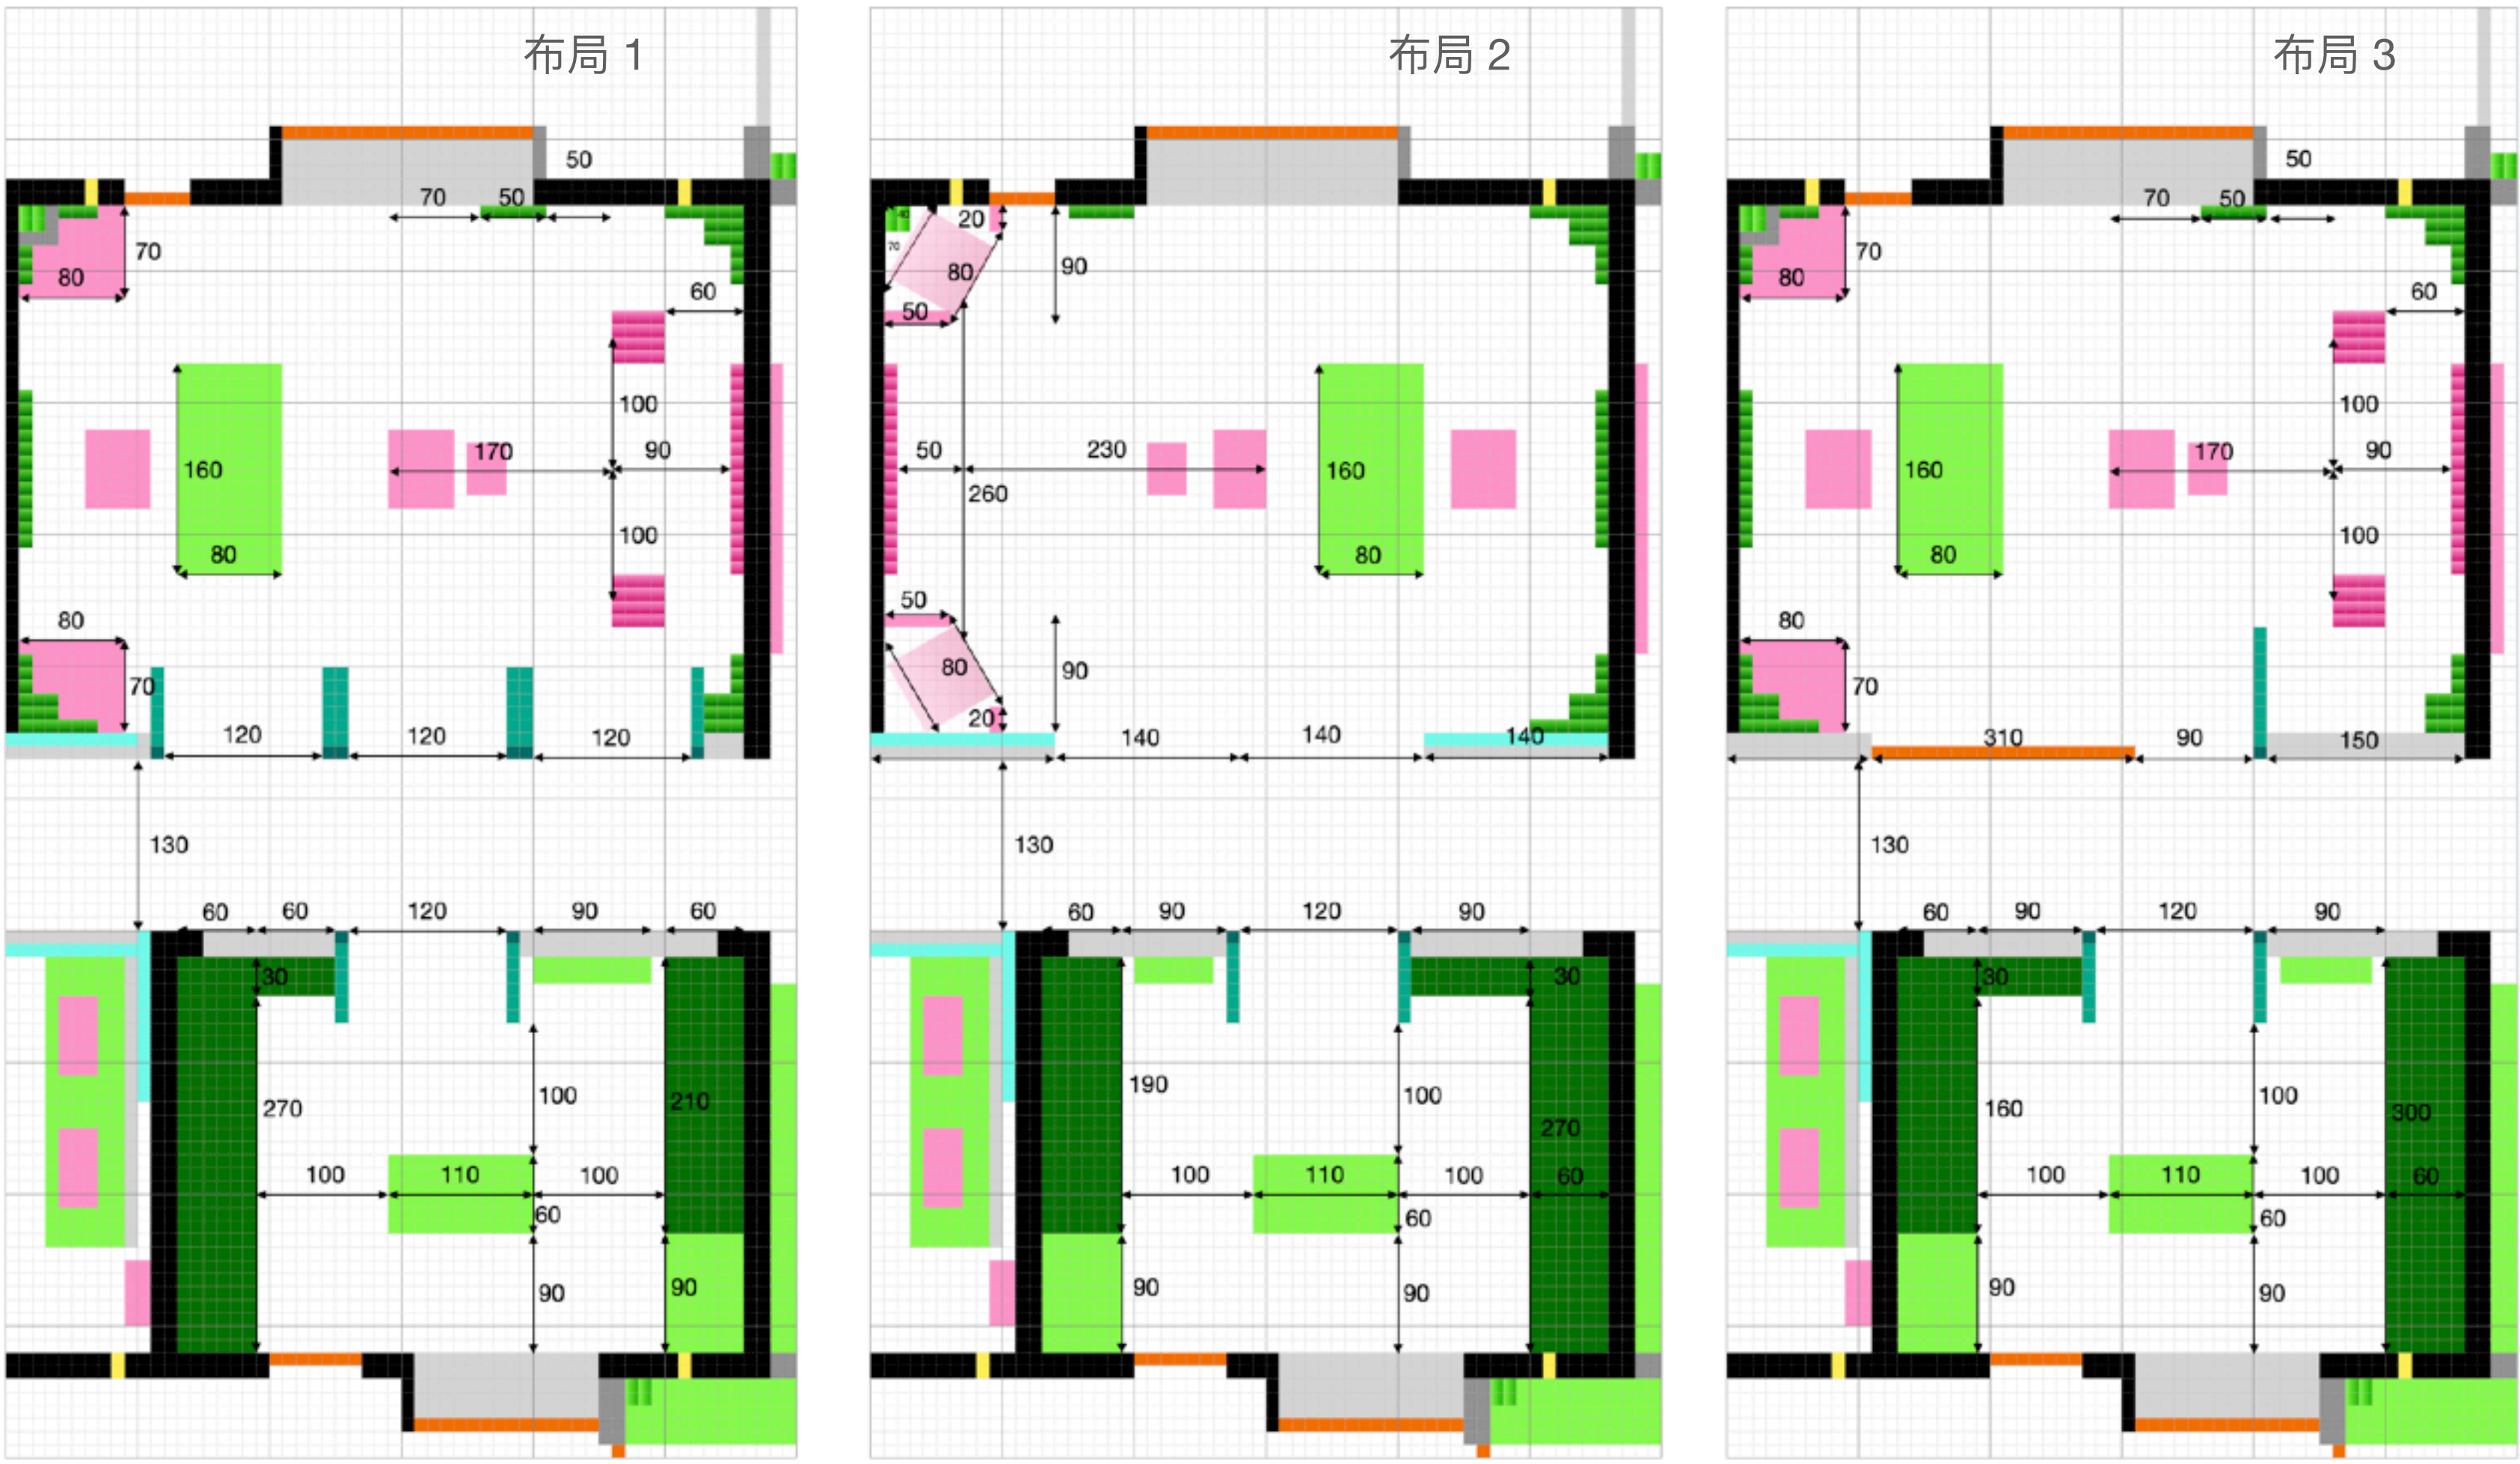

书房:

方案一：偏轴门

- 亮点：单扇 120 cm，三扇叠合可形成 360 cm 的“全景开口”，书房与更衣室门洞可精准对位，仪式感拉满。
- 隐忧：门扇间留缝，隔音是软肋。

方案二：双拉门

- 亮点：两扇 140 cm 拉门，总开口 280 cm，施工简单、造价友好。
- 隐忧：轨道间缝隙仍在，隔音依旧打折。

方案三：玻璃实墙，别墅“轻中式”

- 亮点：整面落地玻璃替代实墙，保留中式格栅或夹绢纹样，空间通透却仍有东方意韵；中空玻璃一关，隔音不再是痛点。
- 隐忧：玻璃需勤擦拭才能常保清透；格栅比例、色温、金属收边需与全屋木作、硬装细节反复校色，否则易显突兀。

更衣室

梳妆台与全身镜的位置，可以放在同一边，或是相反方向。另外根据书房门的选择，更衣室的门可能需要偏一边，或是居中。全身镜的大小与相对短进深的饰品装饰柜(如包包) 可以放在长边或是短边。另外衣柜可以选择壁挂系统，或是立柱系统。衣柜的照明也可以是由上往下，或是直接用背光系统。(如衣柜背板使用宣纸灯箱)

音箱可以用音响架放在客厅方向，或是利用柜子然后放在柜子上(优先考虑)



布局 2
(纯示意)

布局 3
(纯示意)