

主卧佈局方案

****原方案（方案一）****的亮点在于房间拥有良好的回游动线，整体走廊长度较短，空间动线紧凑。然而，其缺点在于主卫浴格局受限，浴缸摆放位置受到较大限制，灵活性较低。

方案二将床旋转180度，显著提升了视野开阔度。虽然该方案在走道空间上有所牺牲，但洗手台因此获得了更灵活的摆放方向。不过，两个空间之间的采光面积较原方案减少了一半（原方案为110+110=220，方案二为120）。




此外，由于马桶孔距为30或40公分，理论上我们可将相关墙面往主卧方向外推，从而扩大厕所与淋浴间的使用空间。

同时，**T字形隔间设计**可最大化入口空间的利用效率，门体可重叠设置于同一墙面，提升空间利用率。

方案二还可在卧室方向增设一道拉门，不仅增强睡眠时的私密性与隔离感，也能有效避免淋浴时水蒸气大量扩散至卧室区域，提升居住舒适度。

方案三采用南北向床位的布局，将中间通道作为卧室与浴室的过渡区域。该方案的主要局限在于床位朝向问题——床脚正对窗户，且缺乏床头柜的摆放空间。可以考虑将床朝飘窗移动, 多出来的空间做一个矮柜. 由于设置双重通道，对走廊的开间尺寸提出了较高要求。(只满足 90cm 最小要求, 但是最好应有 100cm) 浴室设计方面，可将飘窗整合为淋浴区，实现坐浴功能，但浴缸的进出便利性欠佳（常规使用需从长边进入）。

==
另外主卧套間的門可以使用方案 1 的口袋門 (收在洗手台後面) 或是方案 2, 利用特殊五金做成類似人防門的造型. (打開時完全嵌入牆面).

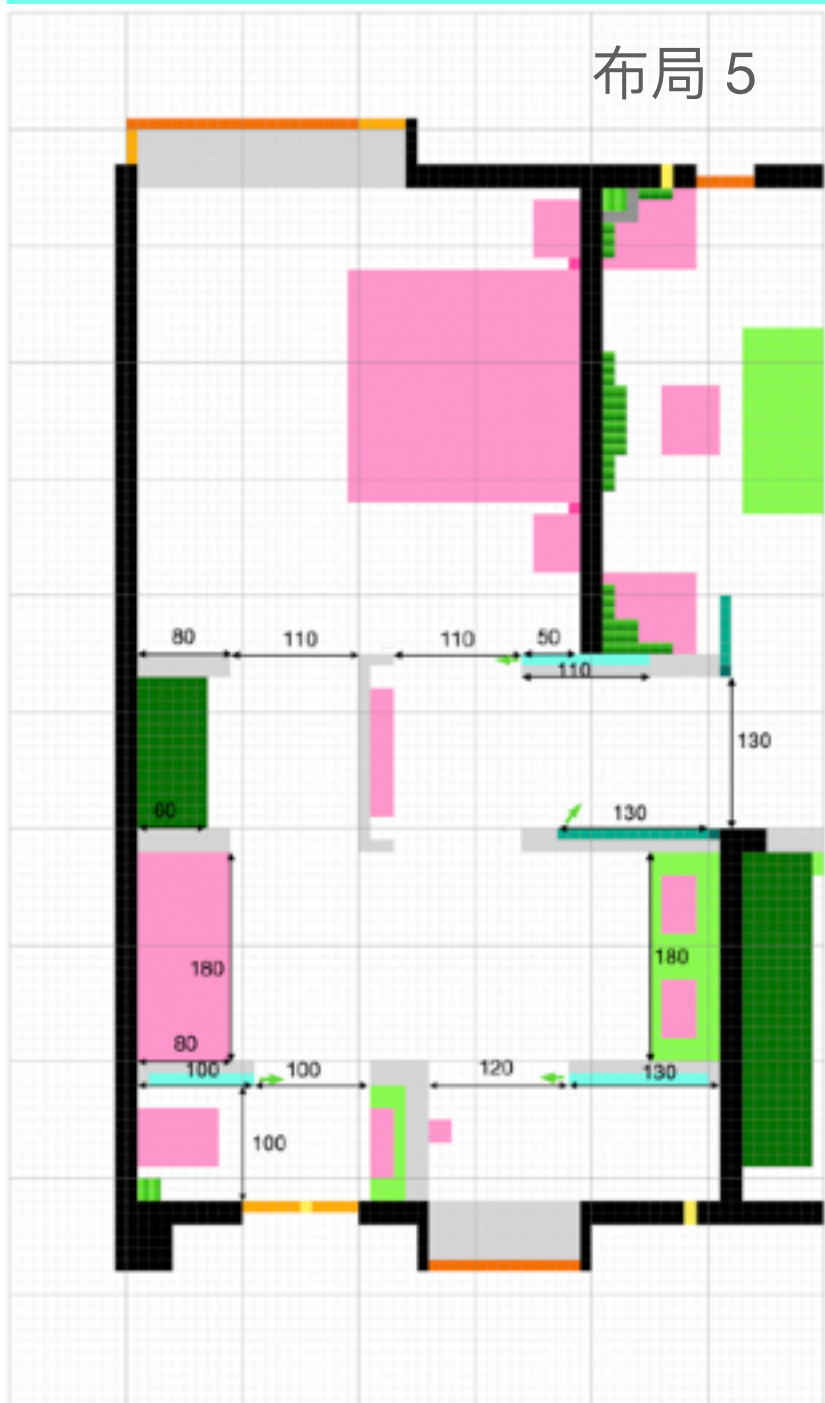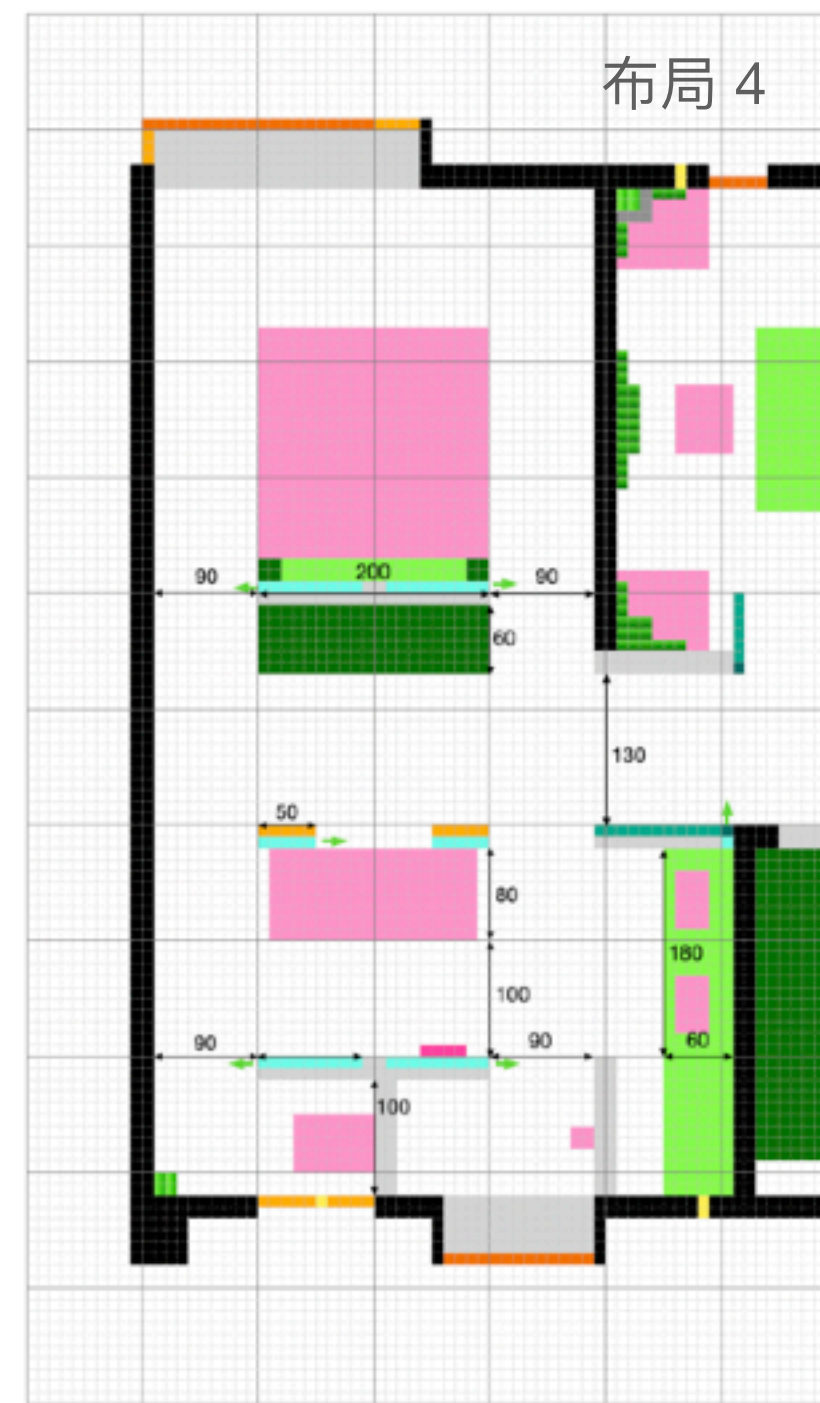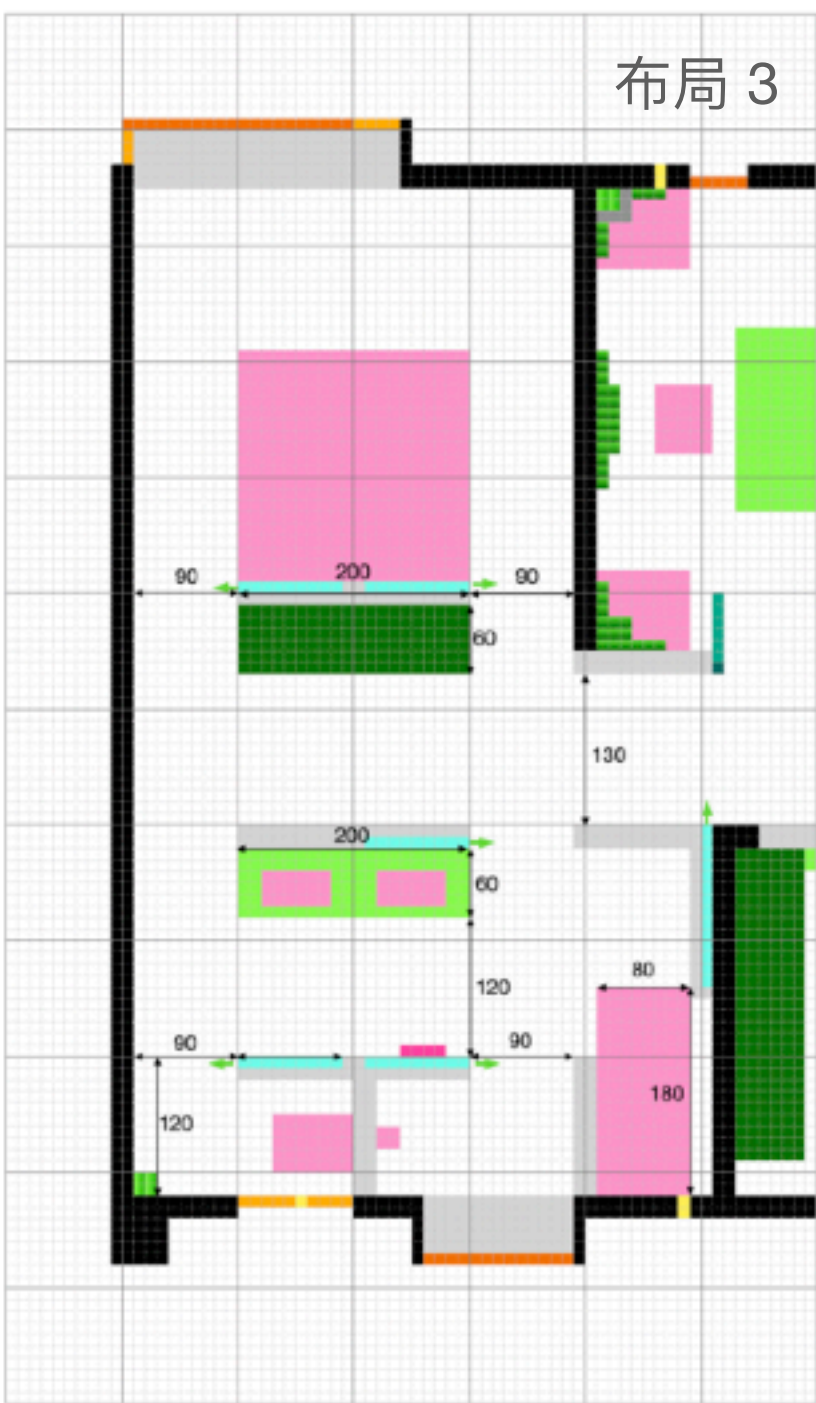

方案四在方案三基础上进行优化，通过调换洗手台与浴缸的位置关系，有效释放了浴缸与更衣区的联动空间（类似酒店套房设计）。此方案需配置独立式浴缸，但存在安全隐患考量。另外，洗手台北墙(图下方)的空间难以有效利用。

方案五融合了以上几个方案, 保留回游动线, 然后浴缸安排在东墙, 这样腾出了约 50cm 给床头部分做包覆. 不过这个方案了淋浴间太长. 可以参考方案四的方法. (因为尺寸不准)

我们还是用了中国传统的人字顶

A modern hotel room featuring two twin beds with white linens and dark brown tufted headboards. A large, rectangular mirror is mounted on the wall above the beds, reflecting the room's interior. The room has a light-colored carpet with a large, stylized floral pattern in shades of purple and pink. A small table with a lamp and a vase of white flowers is visible in the foreground. The room is well-lit, with recessed ceiling lights and a warm, ambient glow.

A view of a bathroom area seen through a large wooden-framed mirror or window. The bathroom features a dark vanity with a sink, a bathtub, and a shower area. The room is illuminated by warm, yellow light.

除了玻璃外,我也住过完全开放式设计,不过这种实用度存疑